


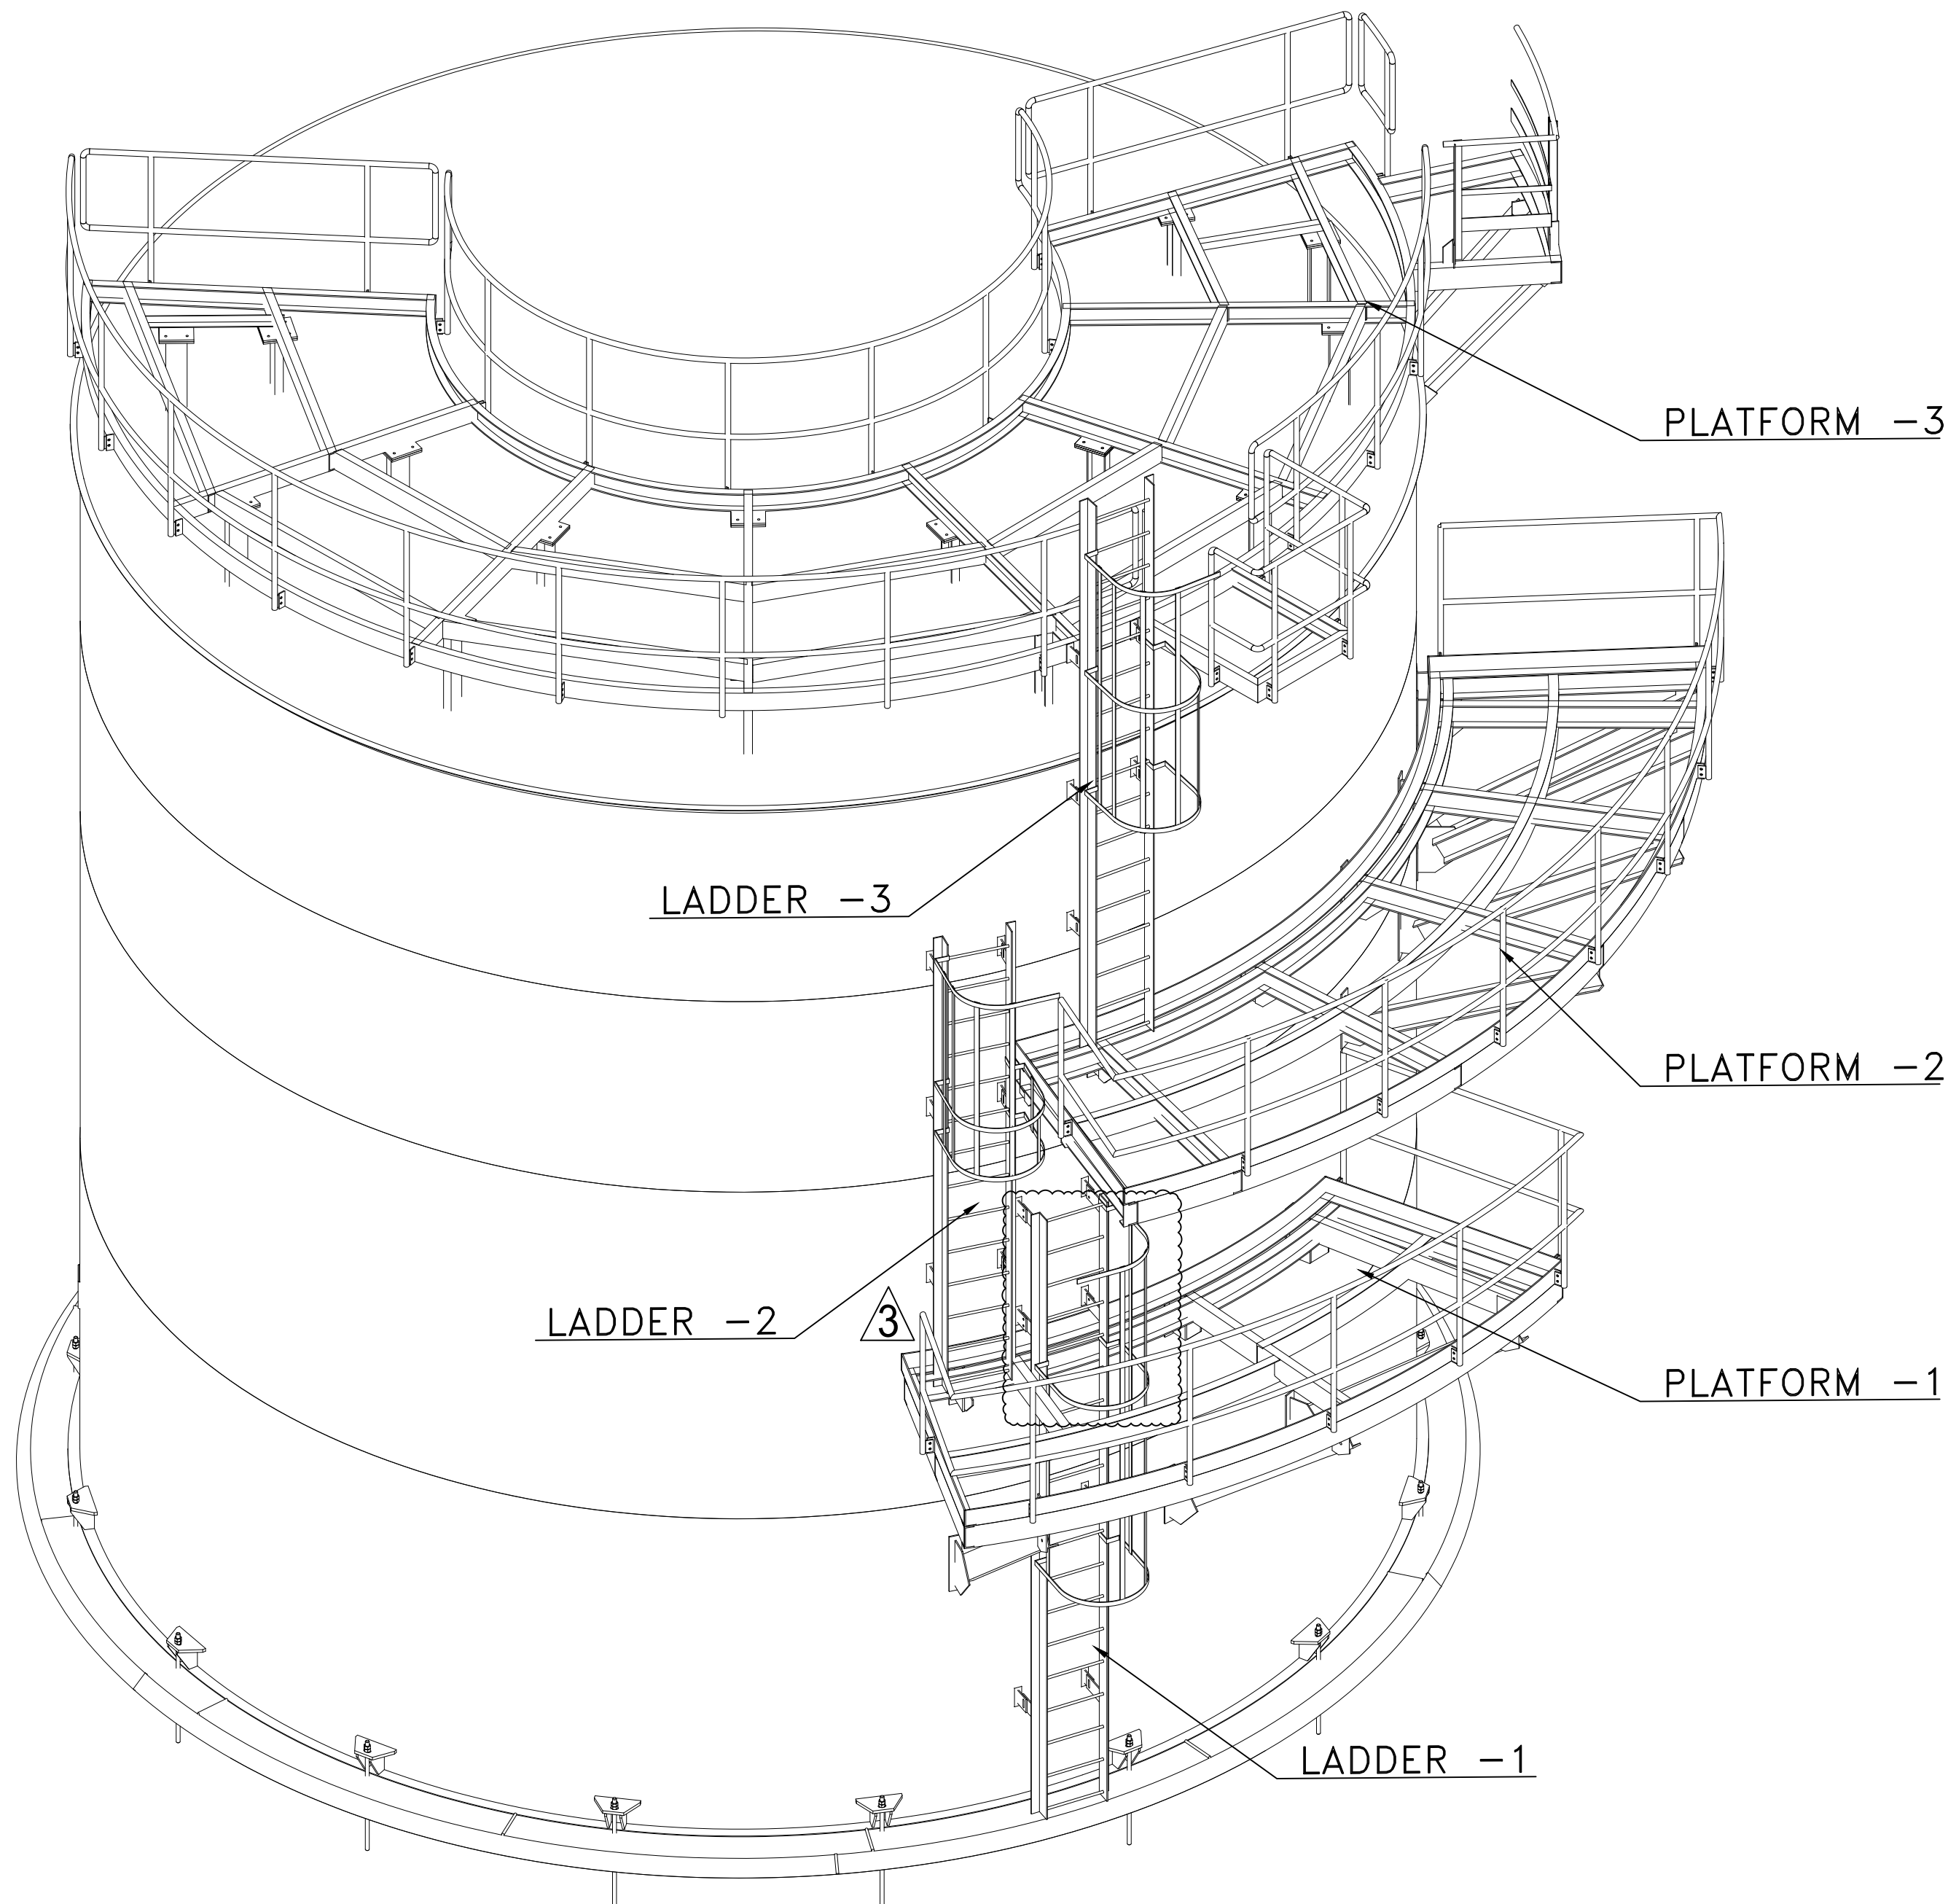

ISOMETRIC VIEW
ASSEMBLY DETAILS FOR LADDER CONNECTION


03	15/11/2025	IFC	ISSUED FOR CONSTRUCTION	CK	RJ	SP
02	23/10/2025	IFC	ISSUED FOR CONSTRUCTION	CK	RJ	SP
01	13/10/2025	IFC	ISSUED FOR CONSTRUCTION	CK	RJ	SP
00	03/10/2025	IFR	ISSUED FOR REVIEW	CK	RJ	SP
Rev.	Date	Status	Revision Description	Iss.	Check.	Appr.

This document is the property of the TOTAL GROUP and it shall not be disclosed to third parties or reproduced without the express written permission of the TOTAL GROUP.
This document has been generated by an Electronic Document Management System. When printed it shall be considered as "for information only". The controlled copy is the EDMS version and it is document holder's responsibility to make sure that latest version is in use.

Affiliate: IRAQ Site: AG1 Project Phase: DE

CENTRAL PROCESSING FACILITIES
EXTERNAL CAGE VERTICAL LADDER DETAIL DRAWING FOR
REJECT WATER TANK (TAG NO. B0-T-54-0006)

Discipline:	PVV	Doc. Type:	GEA	Sector:	B0	System:	7/77
Company Doc. N°:	IQ-AG1-B0-MIC3-000040			Class:	2	Scale:	1:500
Contractor Doc. N°:	MIC-01009.10-DRG-026			Format:	A1	Folio:	1 of 5

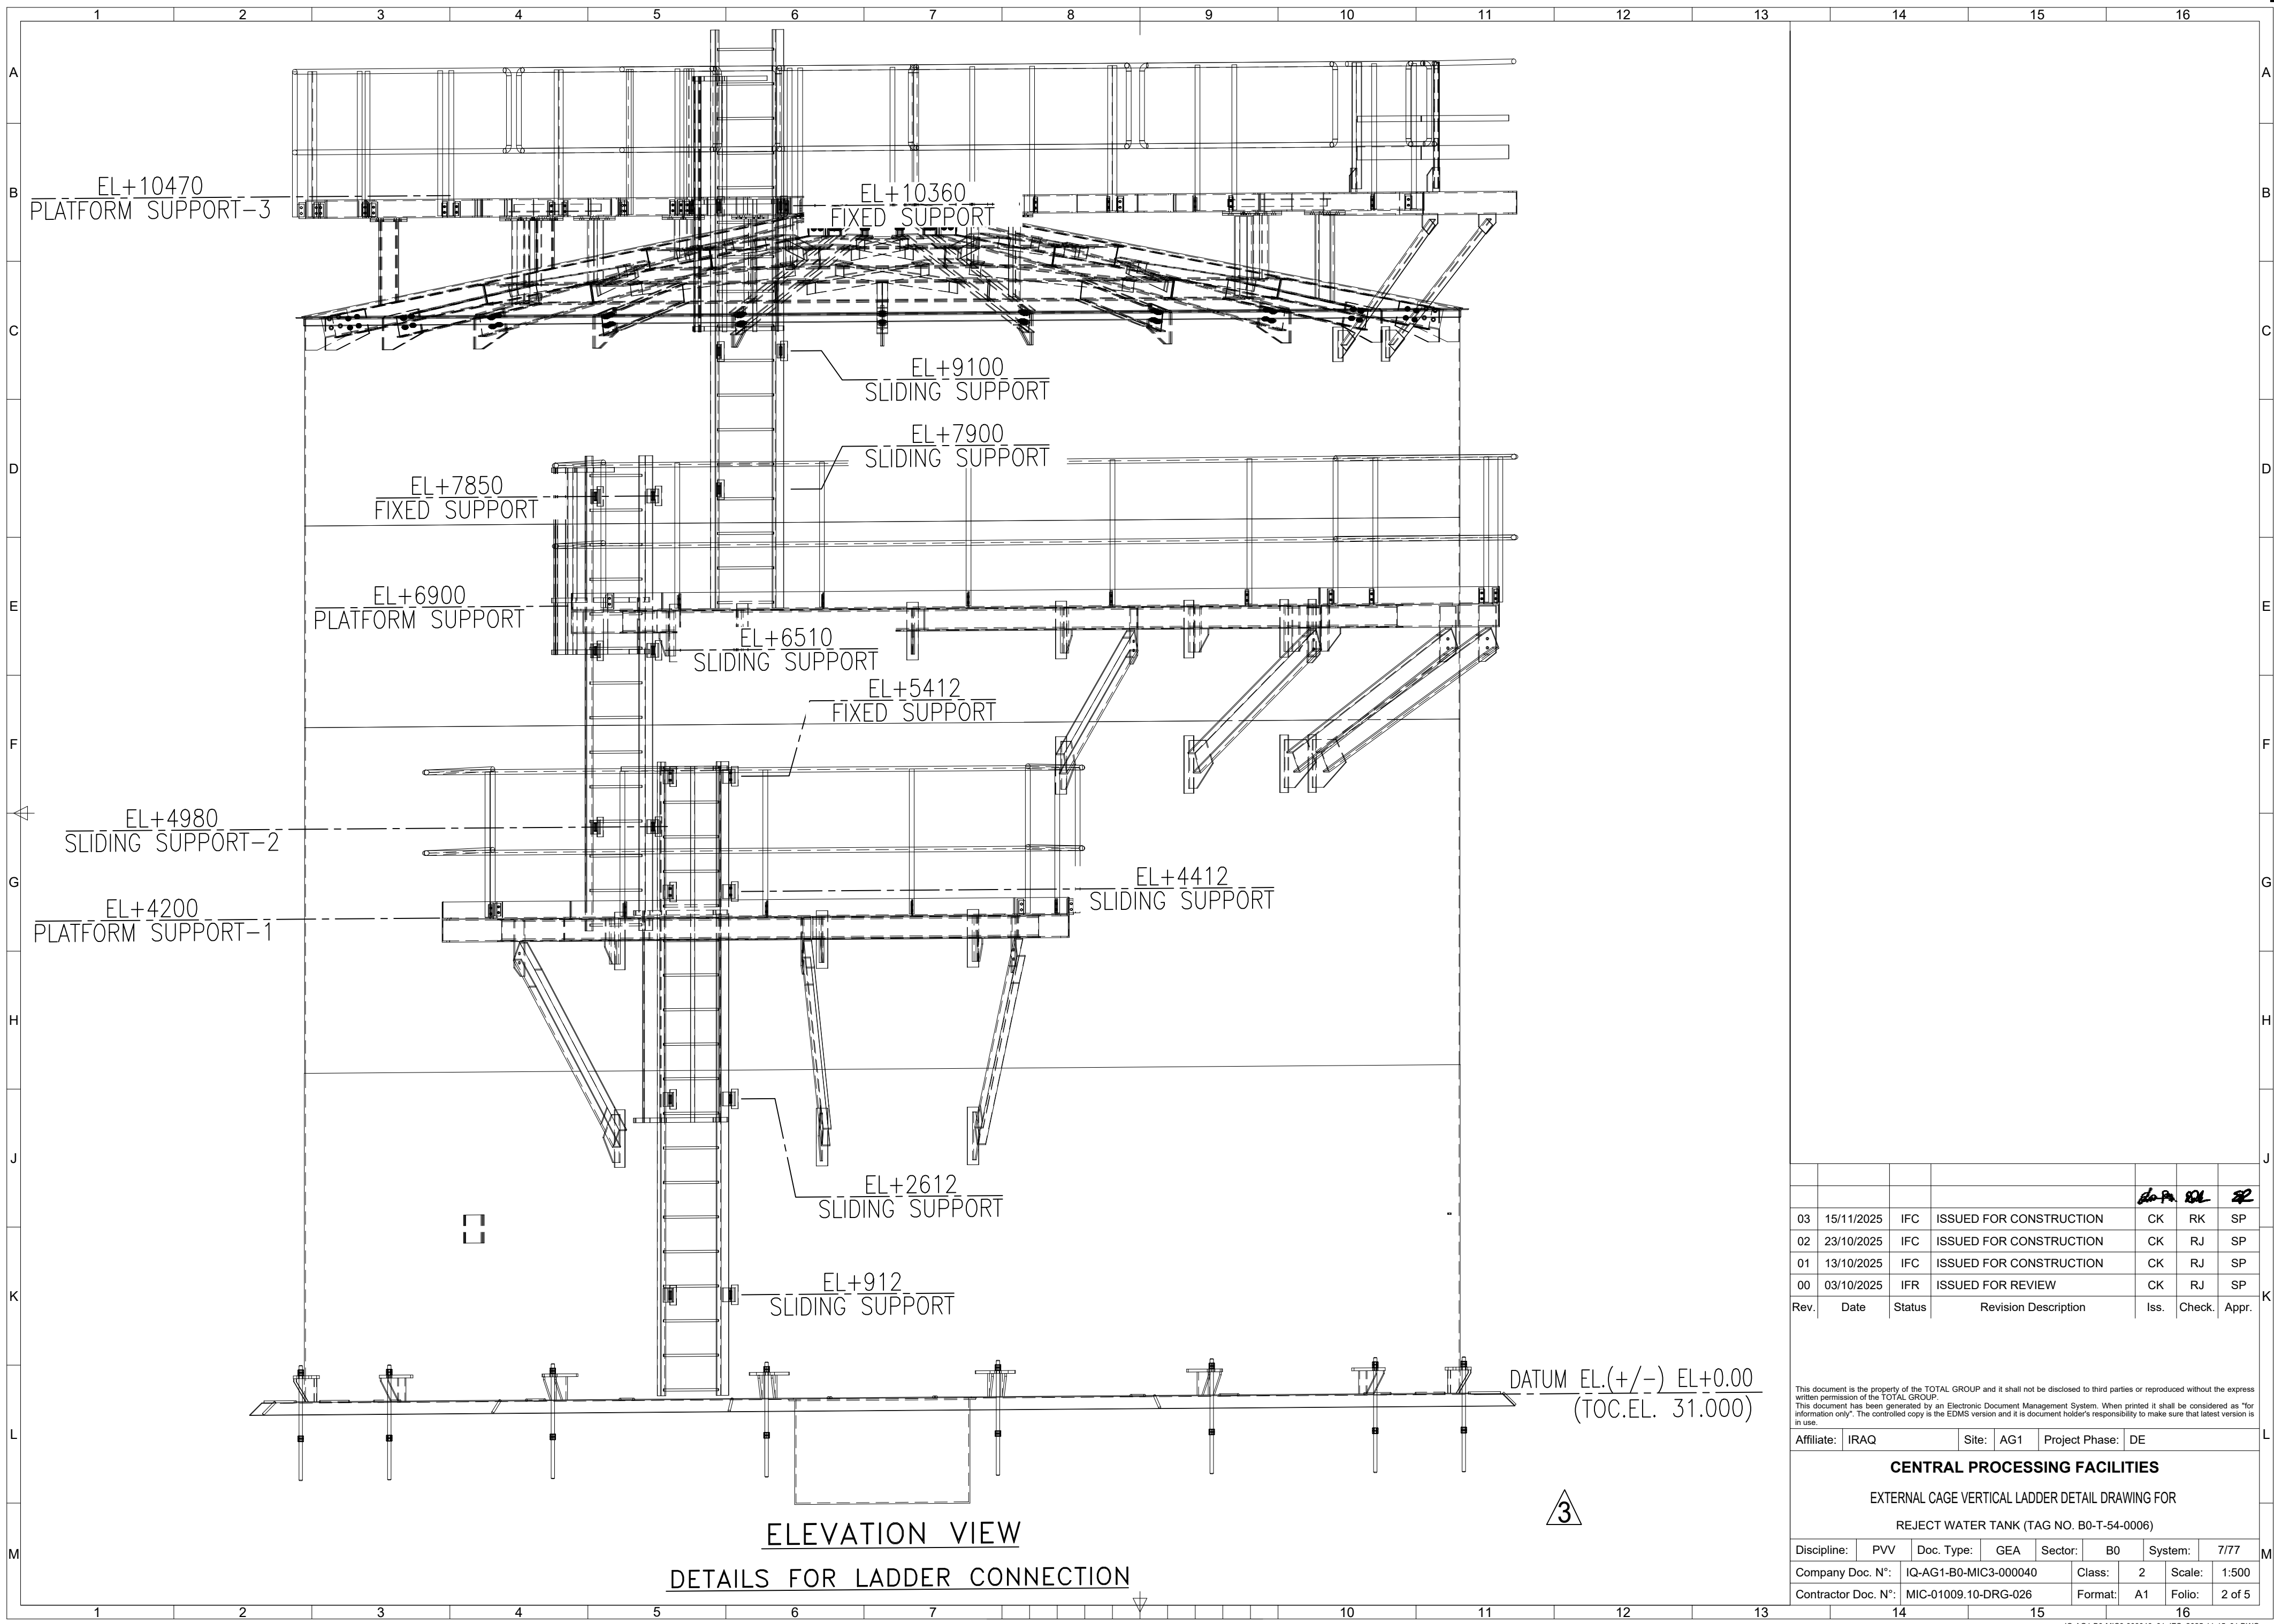


03	15/11/2025	IFC	ISSUED FOR CONSTRUCTION	CK	RK	SP
02	23/10/2025	IFC	ISSUED FOR CONSTRUCTION	CK	RJ	SP
01	13/10/2025	IFC	ISSUED FOR CONSTRUCTION	CK	RJ	SP
00	03/10/2025	IFR	ISSUED FOR REVIEW	CK	RJ	SP
Rev.	Date	Status	Revision Description	Iss.	Check.	Appr.

This document is the property of the TOTAL GROUP and it shall not be disclosed to third parties or reproduced without the express written permission of the TOTAL GROUP.
This document has been generated by an Electronic Document Management System. When printed it shall be considered as "for information only". The controlled copy is the EDMS version and it is document holder's responsibility to make sure that latest version is in use.

Affiliate: IRAQ Site: AG1 Project Phase: DE

CENTRAL PROCESSING FACILITIES
EXTERNAL CAGE VERTICAL LADDER DETAIL DRAWING FOR
REJECT WATER TANK (TAG NO. B0-T-54-0006)

Discipline:	PVV	Doc. Type:	GEA	Sector:	B0	System:	7/77
Company Doc. N°:	IQ-AG1-B0-MIC3-000040			Class:	2	Scale:	1:500
Contractor Doc. N°:	MIC-01009.10-DRG-026			Format:	A1	Folio:	2 of 5

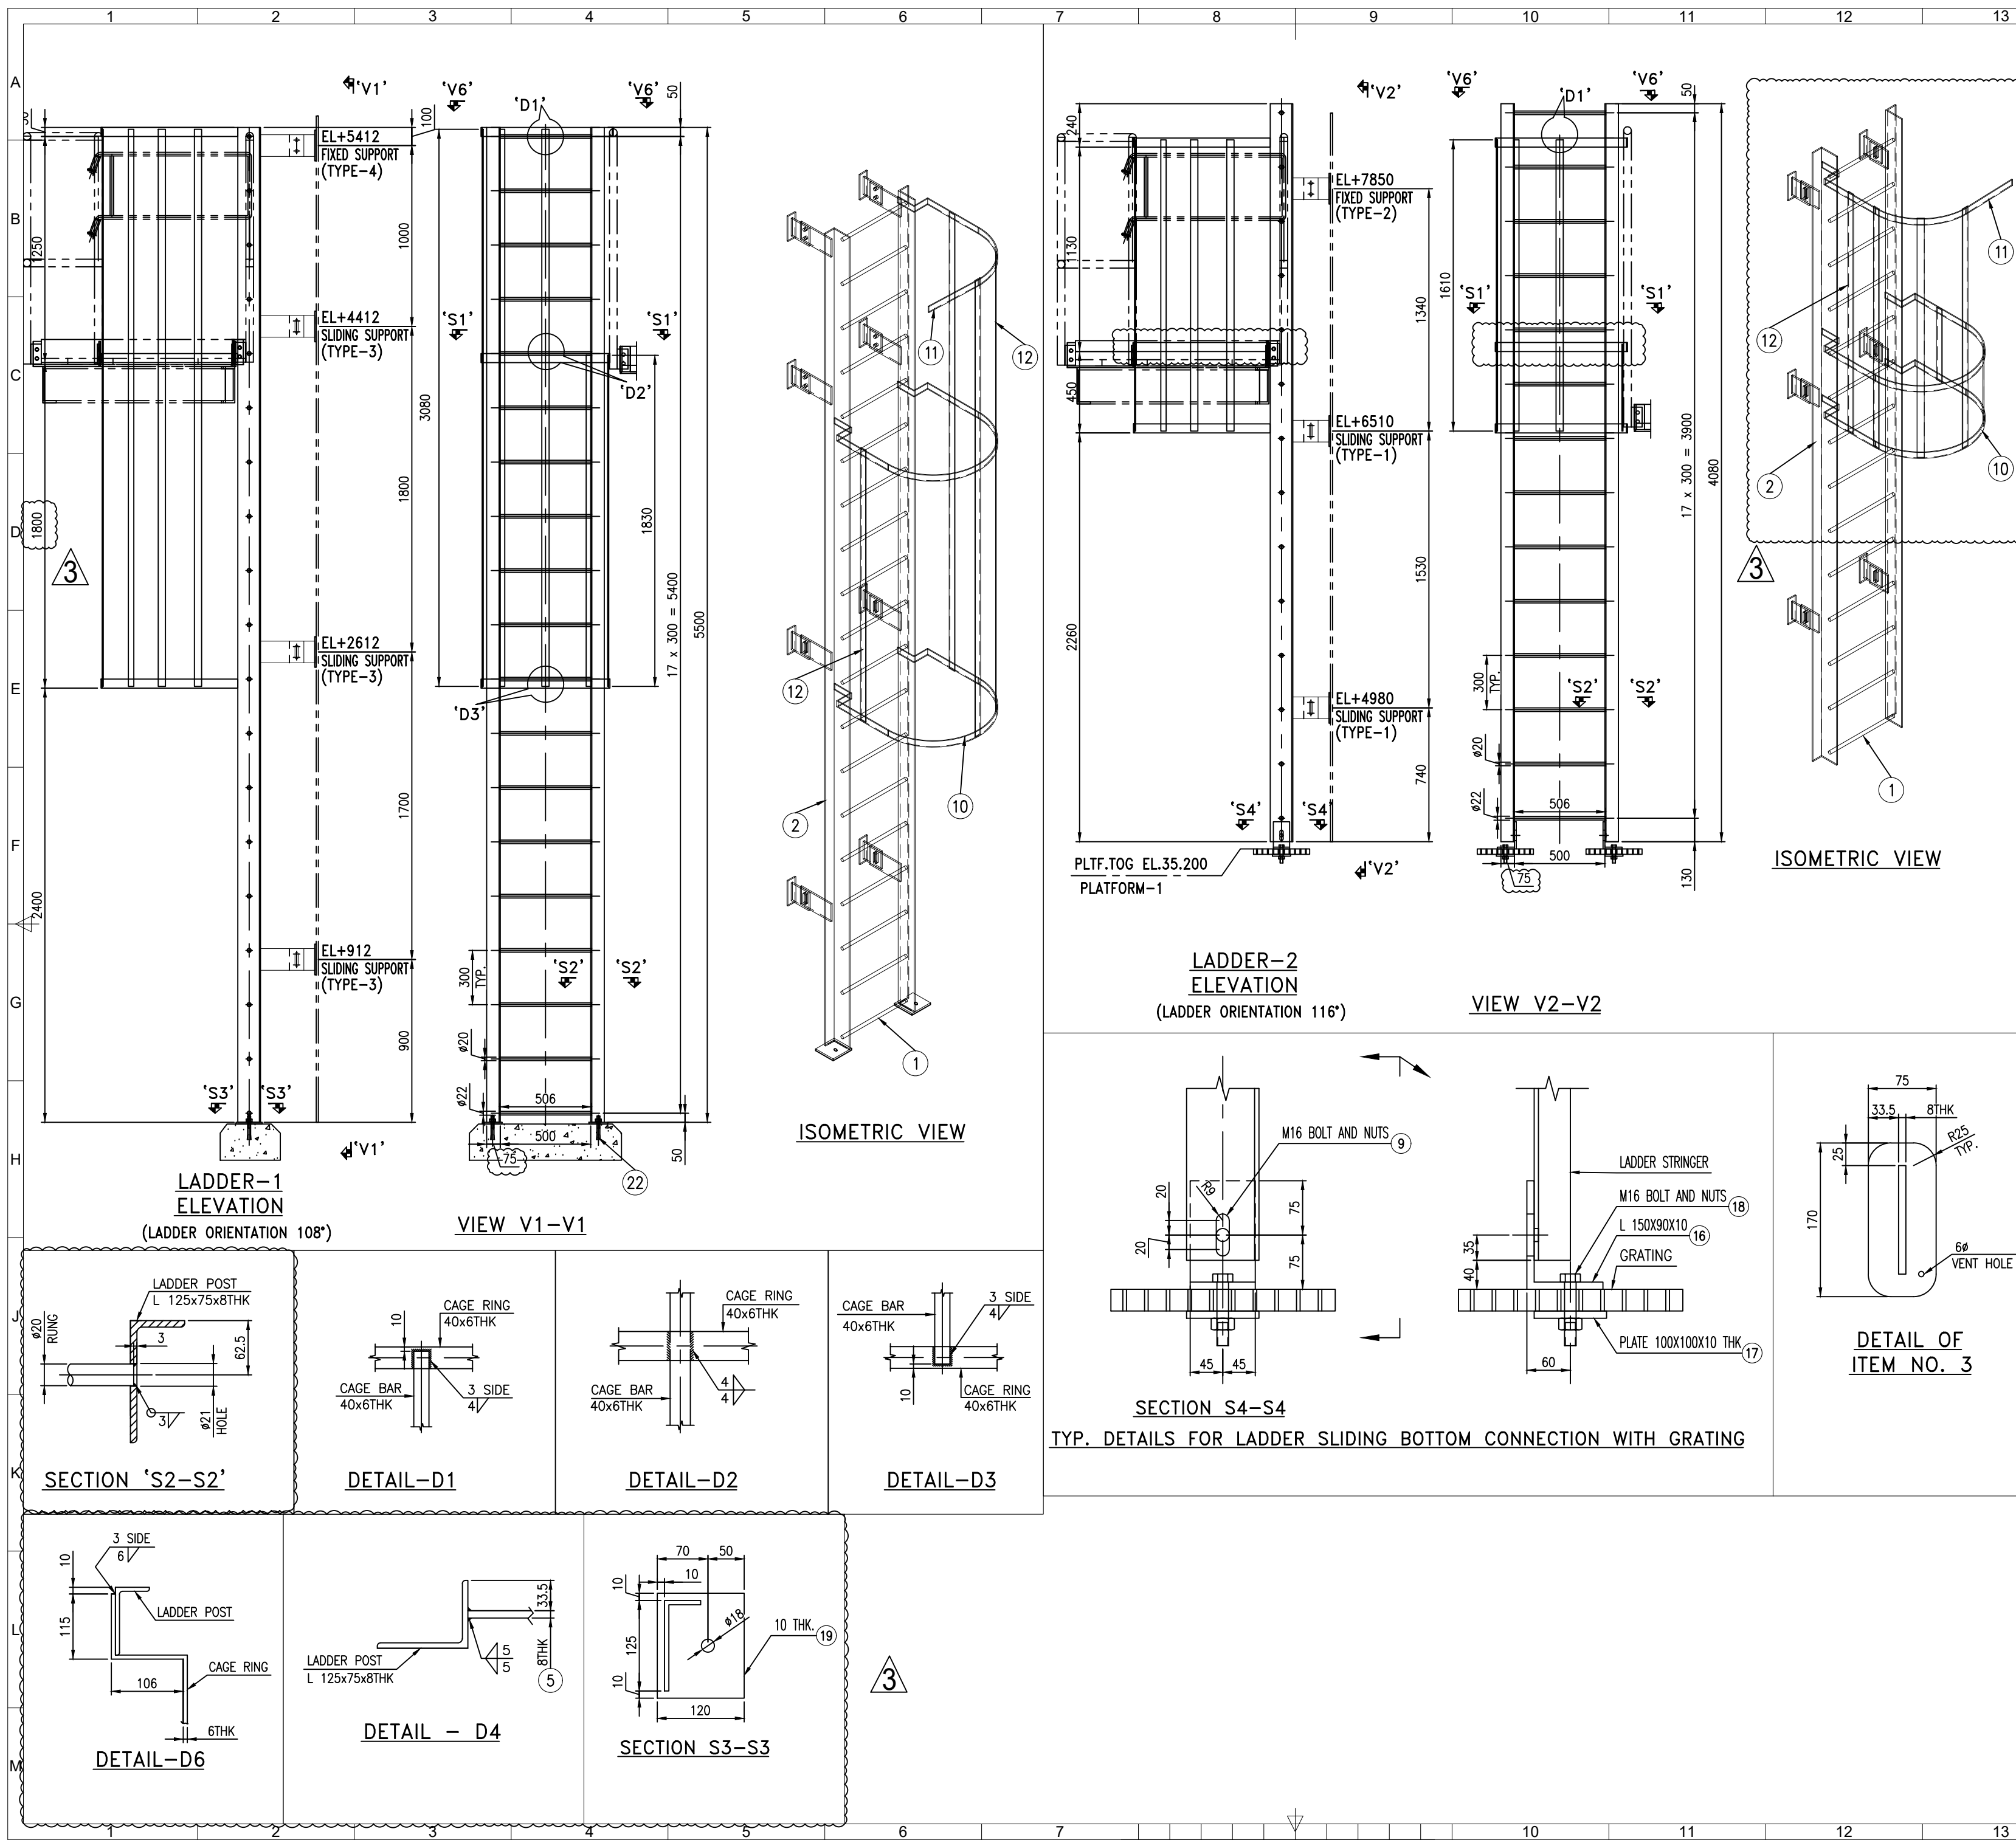

NOTES:

- ALL DIMENSIONS ARE IN MILLIMETERS UNLESS NOTED OTHERWISE.
- ALL FILLET WELDS SHALL BE 6MM UNLESS OTHERWISE SPECIFIED.
- ALL SHARP EDGES SHALL BE ROUNDED OFF.

REFERENCE DOCUMENT NUMBER		
S.NO	CLIENT DOC. NO.	DOCUMENT NAME
1	IQ-AG1B0-MIC3-000006	MECHANICAL DESIGN CALCULATION FOR REJECT WATER TANK (TAG NO. B0-T-54-0006)
2	IQ-AG1B0-MIC3-000008	MECHANICAL DATA SHEET FOR REJECT WATER TANK (TAG NO. B0-T-54-0006)
3	IQ-AG1B0-MIC3-000010	GENERAL ARRANGEMENT DRAWING FOR REJECT WATER TANK (TAG NO. B0-T-54-0006)
4	IQ-AG1B0-MIC3-000014	SHELL DEVELOPMENT DRAWING FOR REJECT WATER TANK (TAG NO. B0-T-54-0006)
5	IQ-AG1B0-MIC3-000020	SHELL NOZZLE DETAIL DRAWING FOR REJECT WATER TANK (TAG NO. B0-T-54-0006)
6	IQ-AG1B0-MIC3-000022	ROOF NOZZLE DETAIL DRAWING INCLUDES INTERNAL DIP PIPE AND ITS SUPPORTING ARRANGEMENTS FOR REJECT WATER TANK (TAG NO. B0-T-54-0006)
7	IQ-AG1B0-MIC3-000026	FOUNDATION / FOOTPRINT DRAWING ALONG WITH FOUNDATION LOADING DATA FOR REJECT WATER TANK (TAG NO. B0-T-54-0006)
8	IQ-AG1B0-MIC3-000038	NAME PLATE & BRACKET DRAWING FOR REJECT WATER TANK (TAG NO. B0-T-54-0006)
9	IQ-AG1B0-MIC3-000080	CATHODIC PROTECTION DRAWINGS REJECT WATER TANK (TAG NO. B0-T-54-0006)
10	IQ-AG1B0-MIC3-000024	DETAIL DRAWING FOR EXTERNAL ATTACHMENTS FOR REJECT WATER TANK (TAG NO. B0-T-54-0006)
11	IQ-AG1B0-MIC3-000044	EXTERNAL ROOF STRUCTURE DRAWING FOR REJECT WATER TANK (TAG NO. B0-T-54-0006)
12	IQ-AG1-A0-GHB1-133011	TYPICAL DETAILS OF LADDER

Rev.	Date	Status	Revision Description	Iss.	Check.	Appr.
03	15/11/2025	IFC	ISSUED FOR CONSTRUCTION	CK	RJ	SP
02	23/10/2025	IFC	ISSUED FOR CONSTRUCTION	CK	RJ	SP
01	13/10/2025	IFC	ISSUED FOR CONSTRUCTION	CK	RJ	SP
00	03/10/2025	IFR	ISSUED FOR REVIEW	CK	RJ	SP

PROJECT NAME & LOGO

CONTRACTOR NAME & LOGO

This document is the property of the TOTAL GROUP and it shall not be disclosed to third parties or reproduced without the express written permission of the TOTAL GROUP.
This document has been generated by an Electronic Document Management System. When printed it shall be considered as "for information only". The controlled copy is the EDMS version and it is document holder's responsibility to make sure that latest version is in use.












Affiliate: IRAQ Site: AG1 Project Phase: DE

CENTRAL PROCESSING FACILITIES

EXTERNAL CAGE VERTICAL LADDER DETAIL DRAWING FOR

REJECT WATER TANK (TAG NO. B0-T-54-0006)

Discipline:	PVV	Doc. Type:	GEA	Sector:	B0	System:	7/77
Company Doc. N°:	IQ-AG1-B0-MIC3-000040			Class:	2	Scale:	1:500
Contractor Doc. N°:	MIC-01009.10-DRG-026			Format:	A1	Folio:	3 of 5

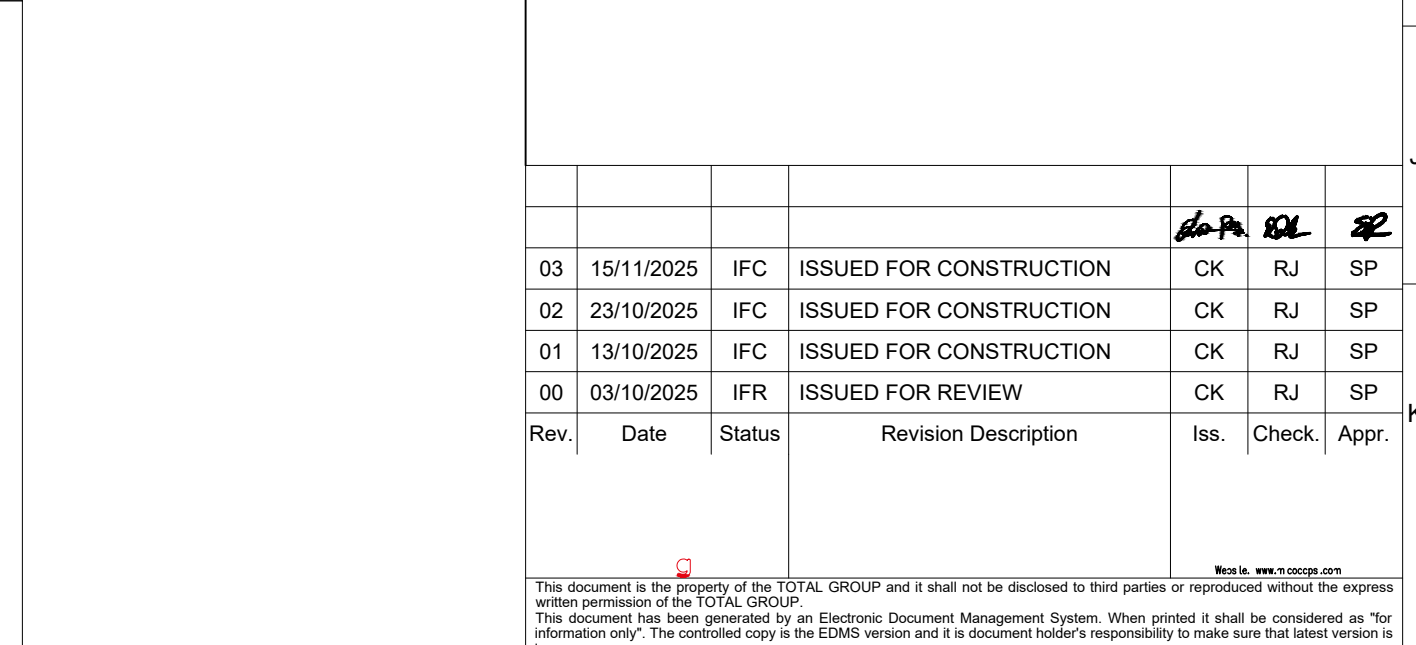 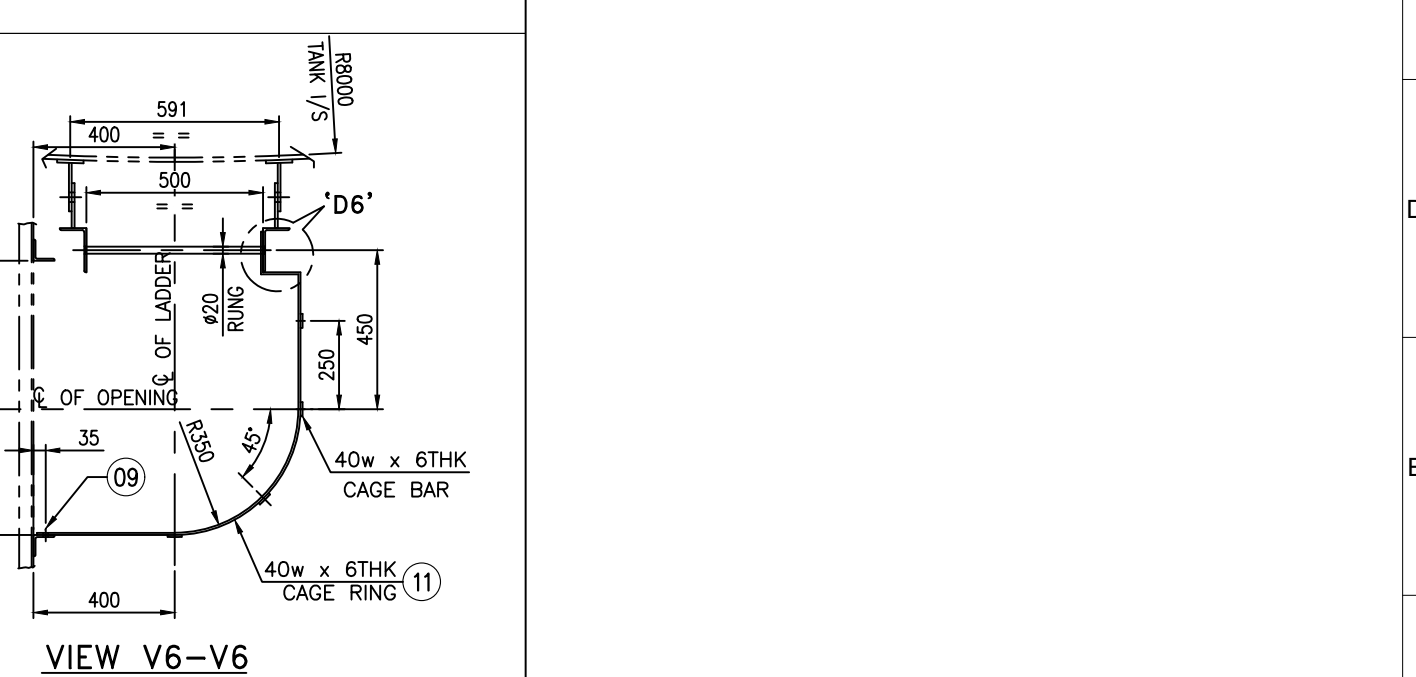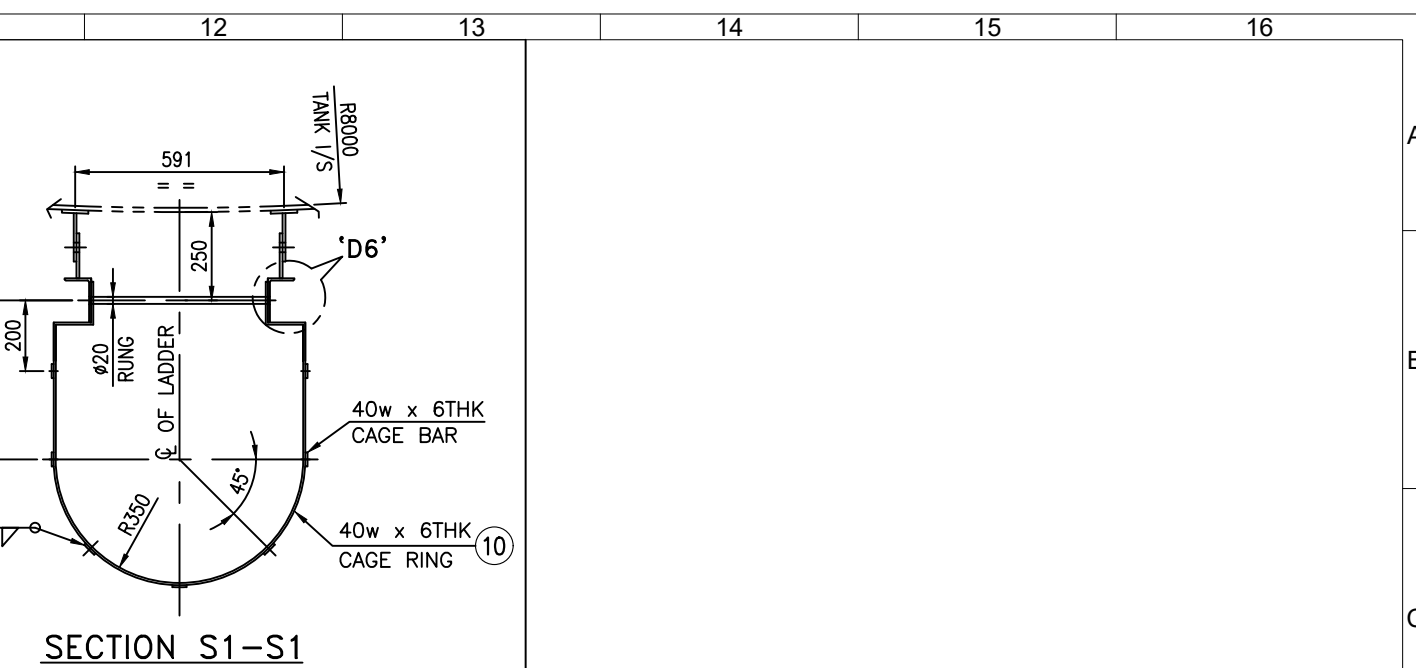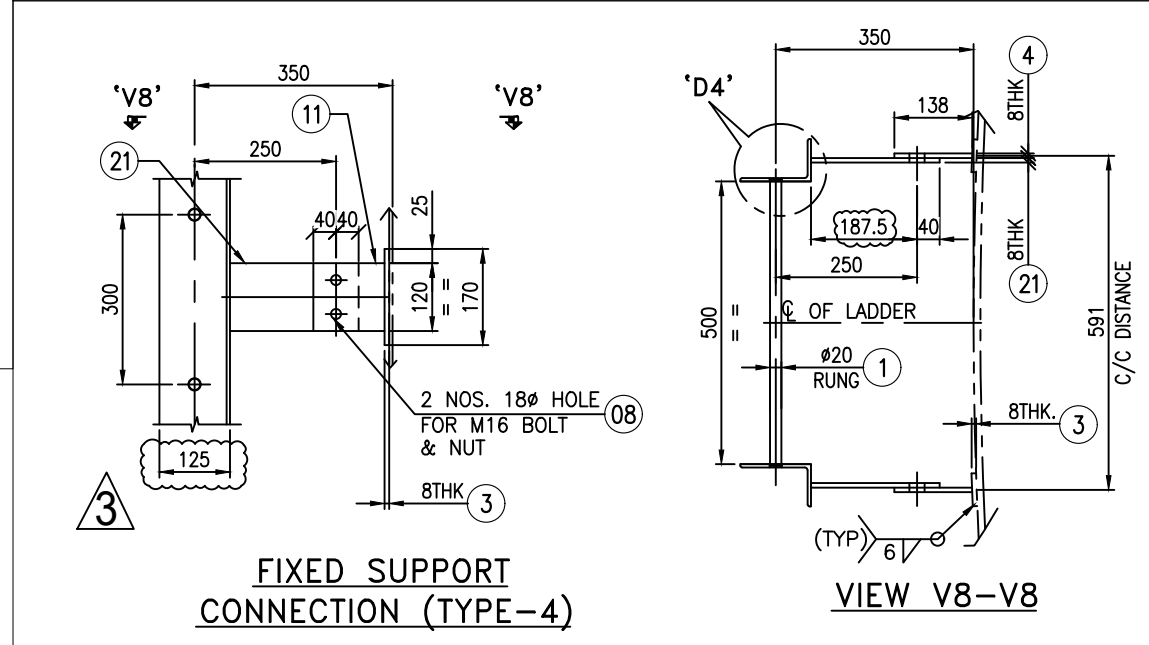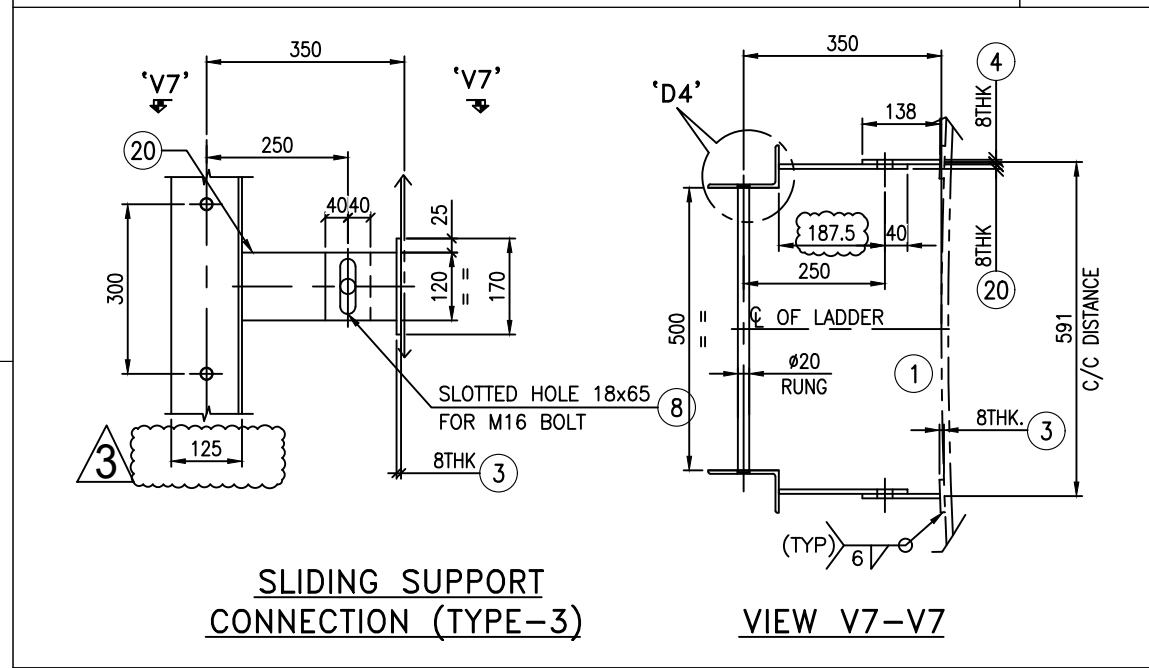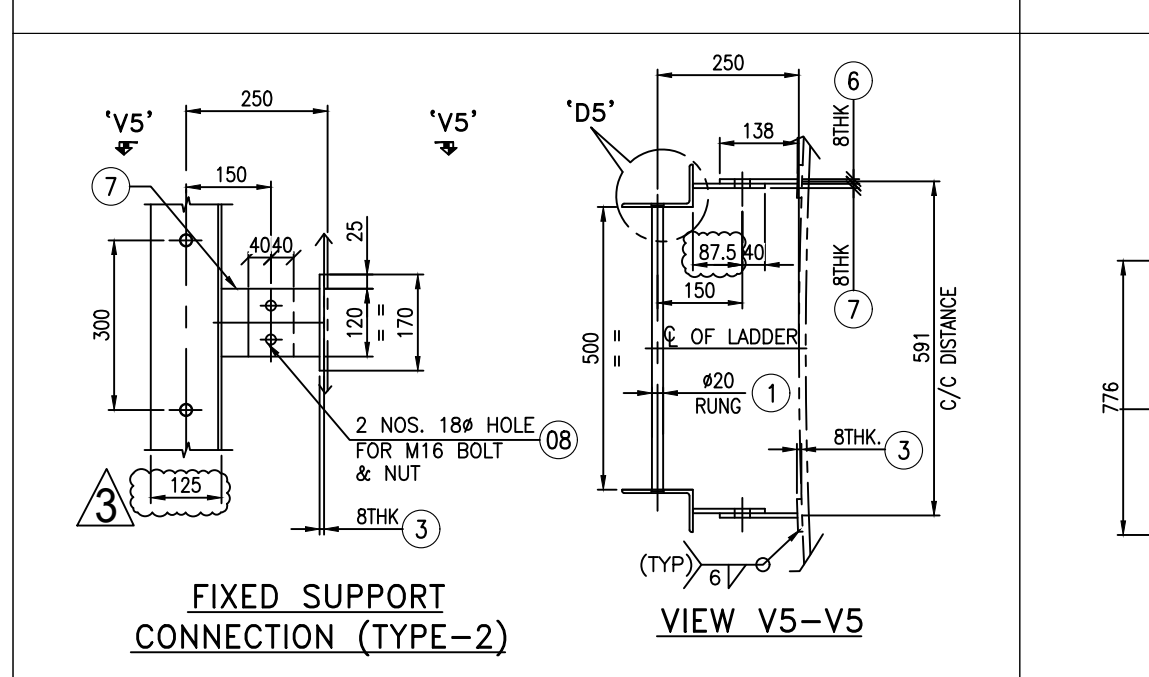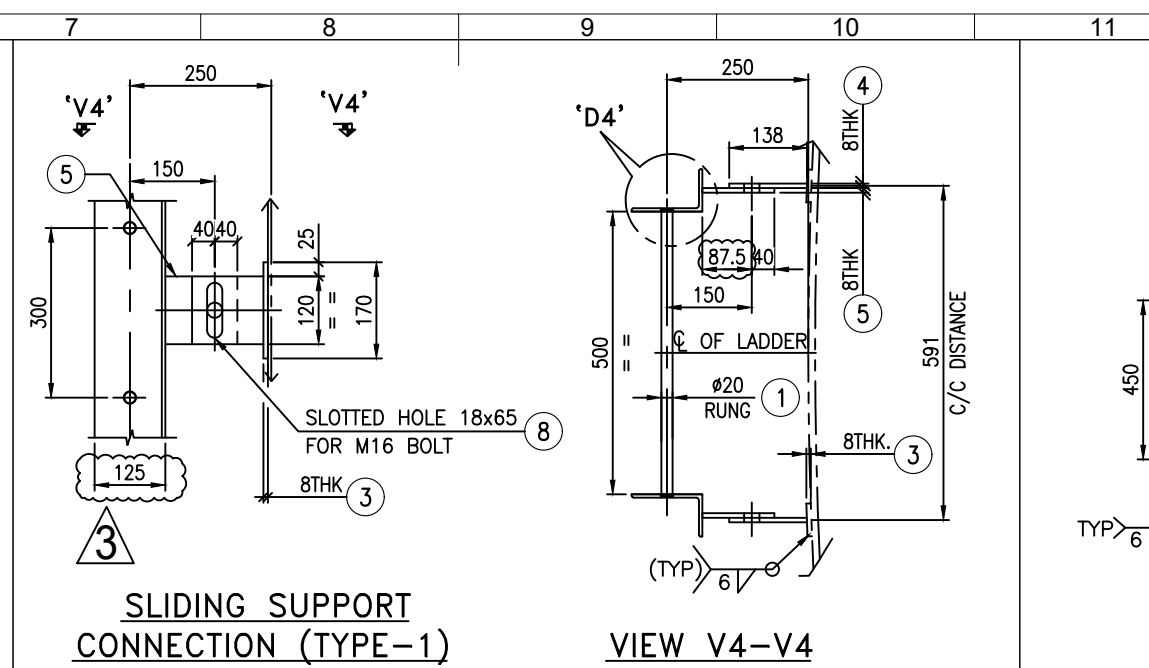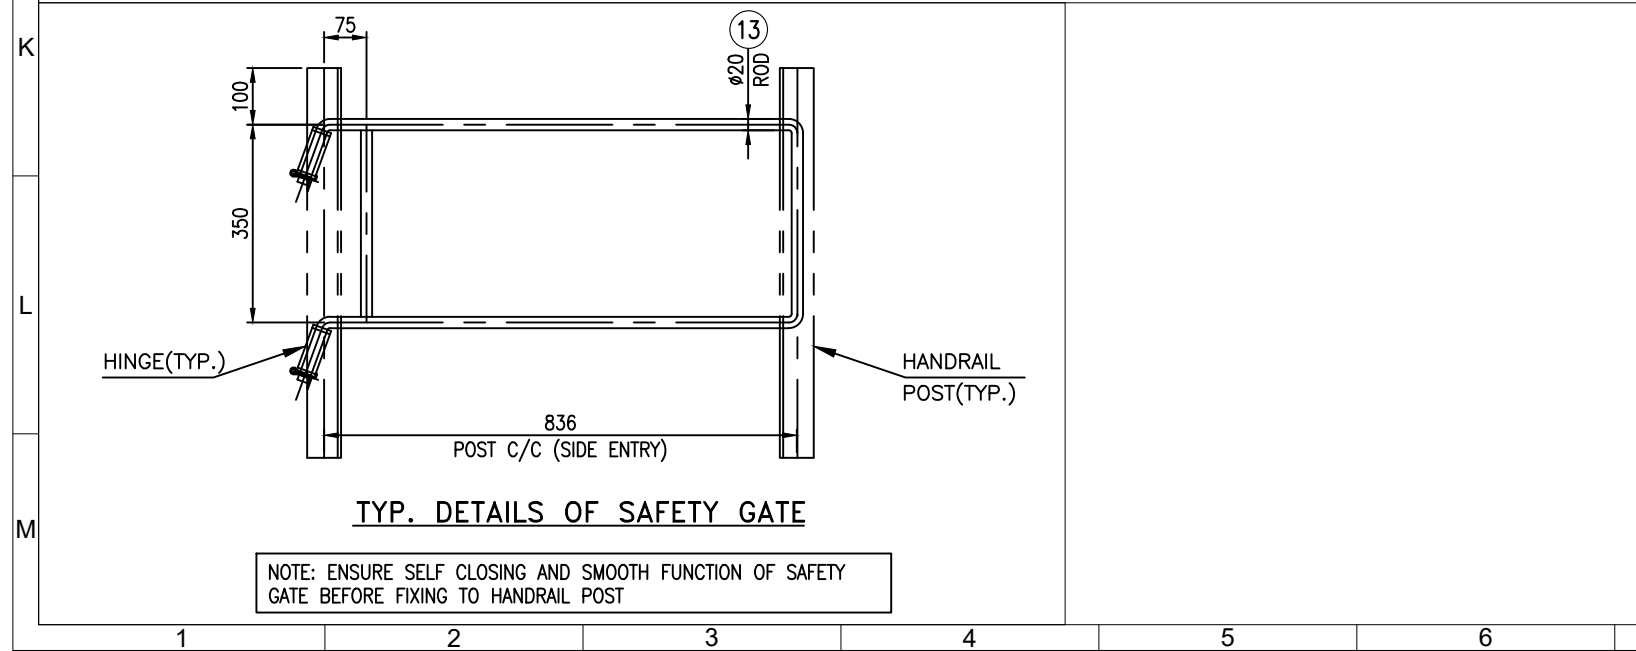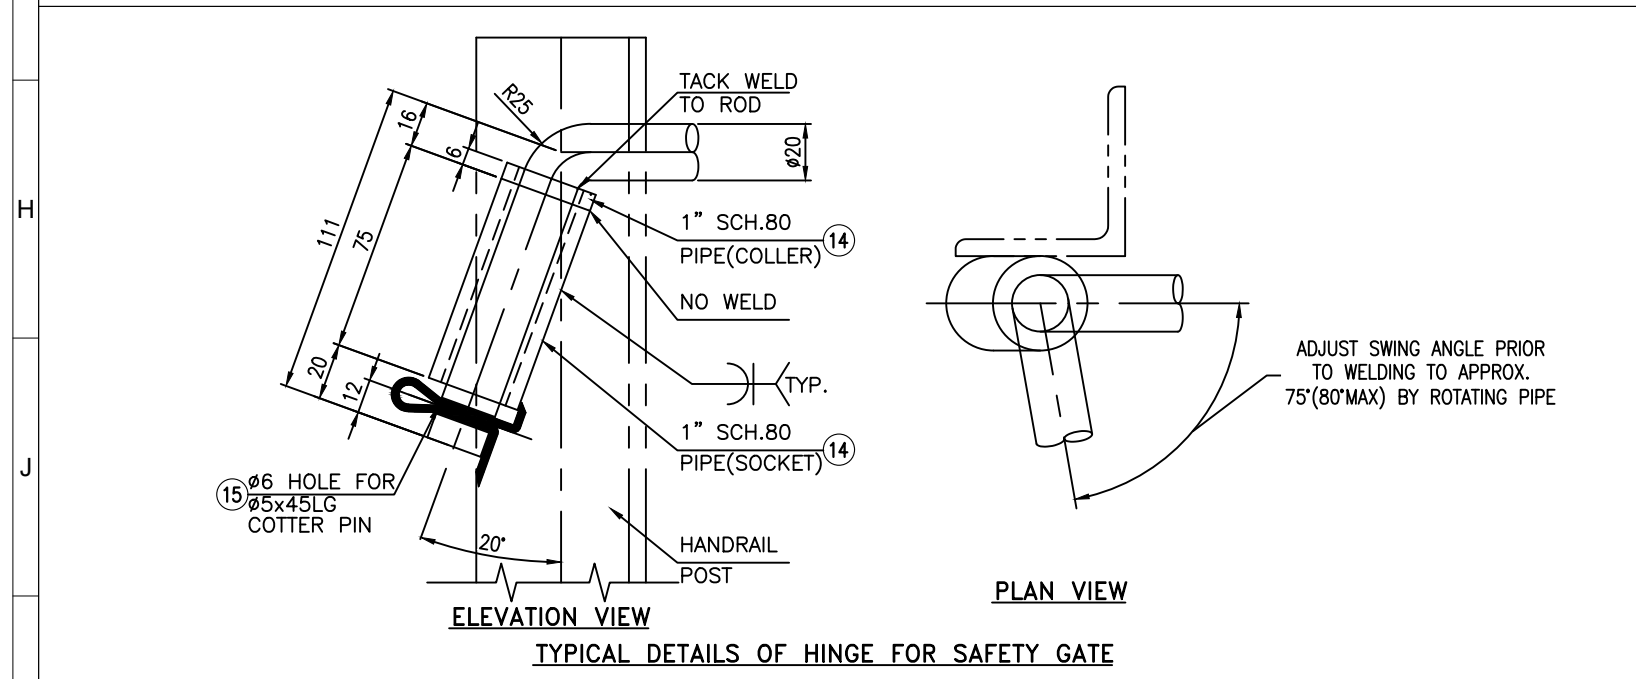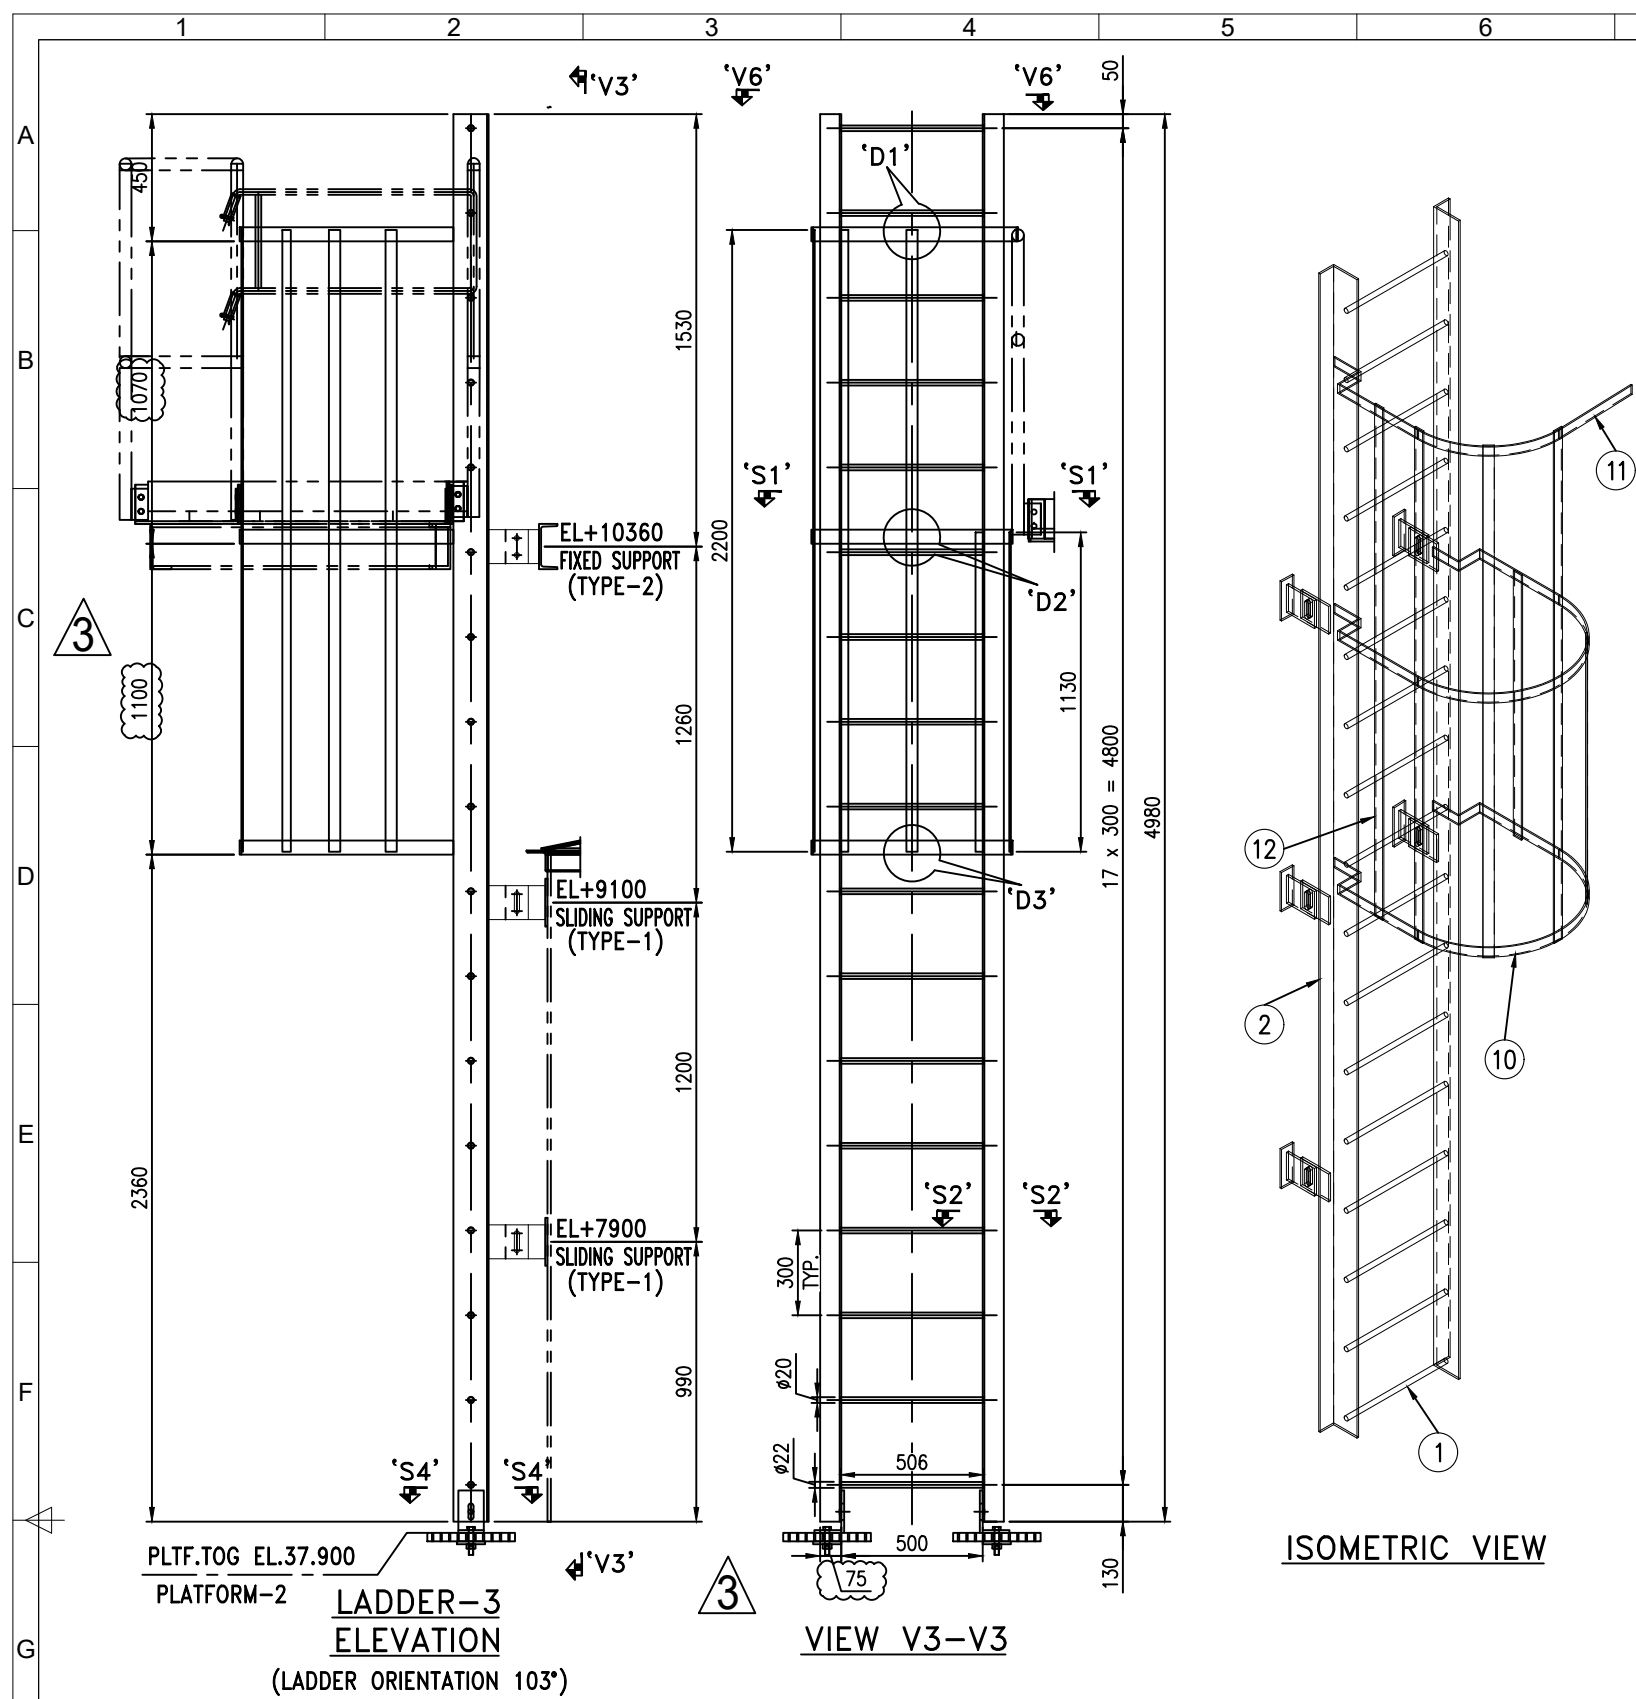

Rev.	Date	Status	Revision Description	Iss.	Check.	Appr.
03	15/11/2025	IFC	ISSUED FOR CONSTRUCTION	CK	RJ	SP
02	23/10/2025	IFC	ISSUED FOR CONSTRUCTION	CK	RJ	SP
01	13/10/2025	IFC	ISSUED FOR CONSTRUCTION	CK	RJ	SP
00	03/10/2025	IFR	ISSUED FOR REVIEW	CK	RJ	SP

This document is the property of the TOTAL GROUP and it shall not be disclosed to third parties or reproduced without the express written permission of the TOTAL GROUP.						
This document has been generated by an Electronic Document Management System. When printed it shall be considered as "for information only". The controlled copy is the EDMS version and it is document holder's responsibility to make sure that latest version is in use.						
Affiliate:	IRAQ	Site:	AG1	Project Phase:	DE	
CENTRAL PROCESSING FACILITIES						
EXTERNAL CAGE VERTICAL LADDER DETAIL DRAWING FOR						
REJECT WATER TANK (TAG NO. B0-T-54-0006)						
Discipline:	PVV	Doc. Type:	GEA	Sector:	B0	System:
Company Doc. N°:	IQ-AG1-B0-MIC3-000040	Class:	2	Scale:	1:500	7/77
Contractor Doc. N°:	MIC-01009.10-DRG-026	Format:	A1	Folio:	4 of 5	

[illegible]