




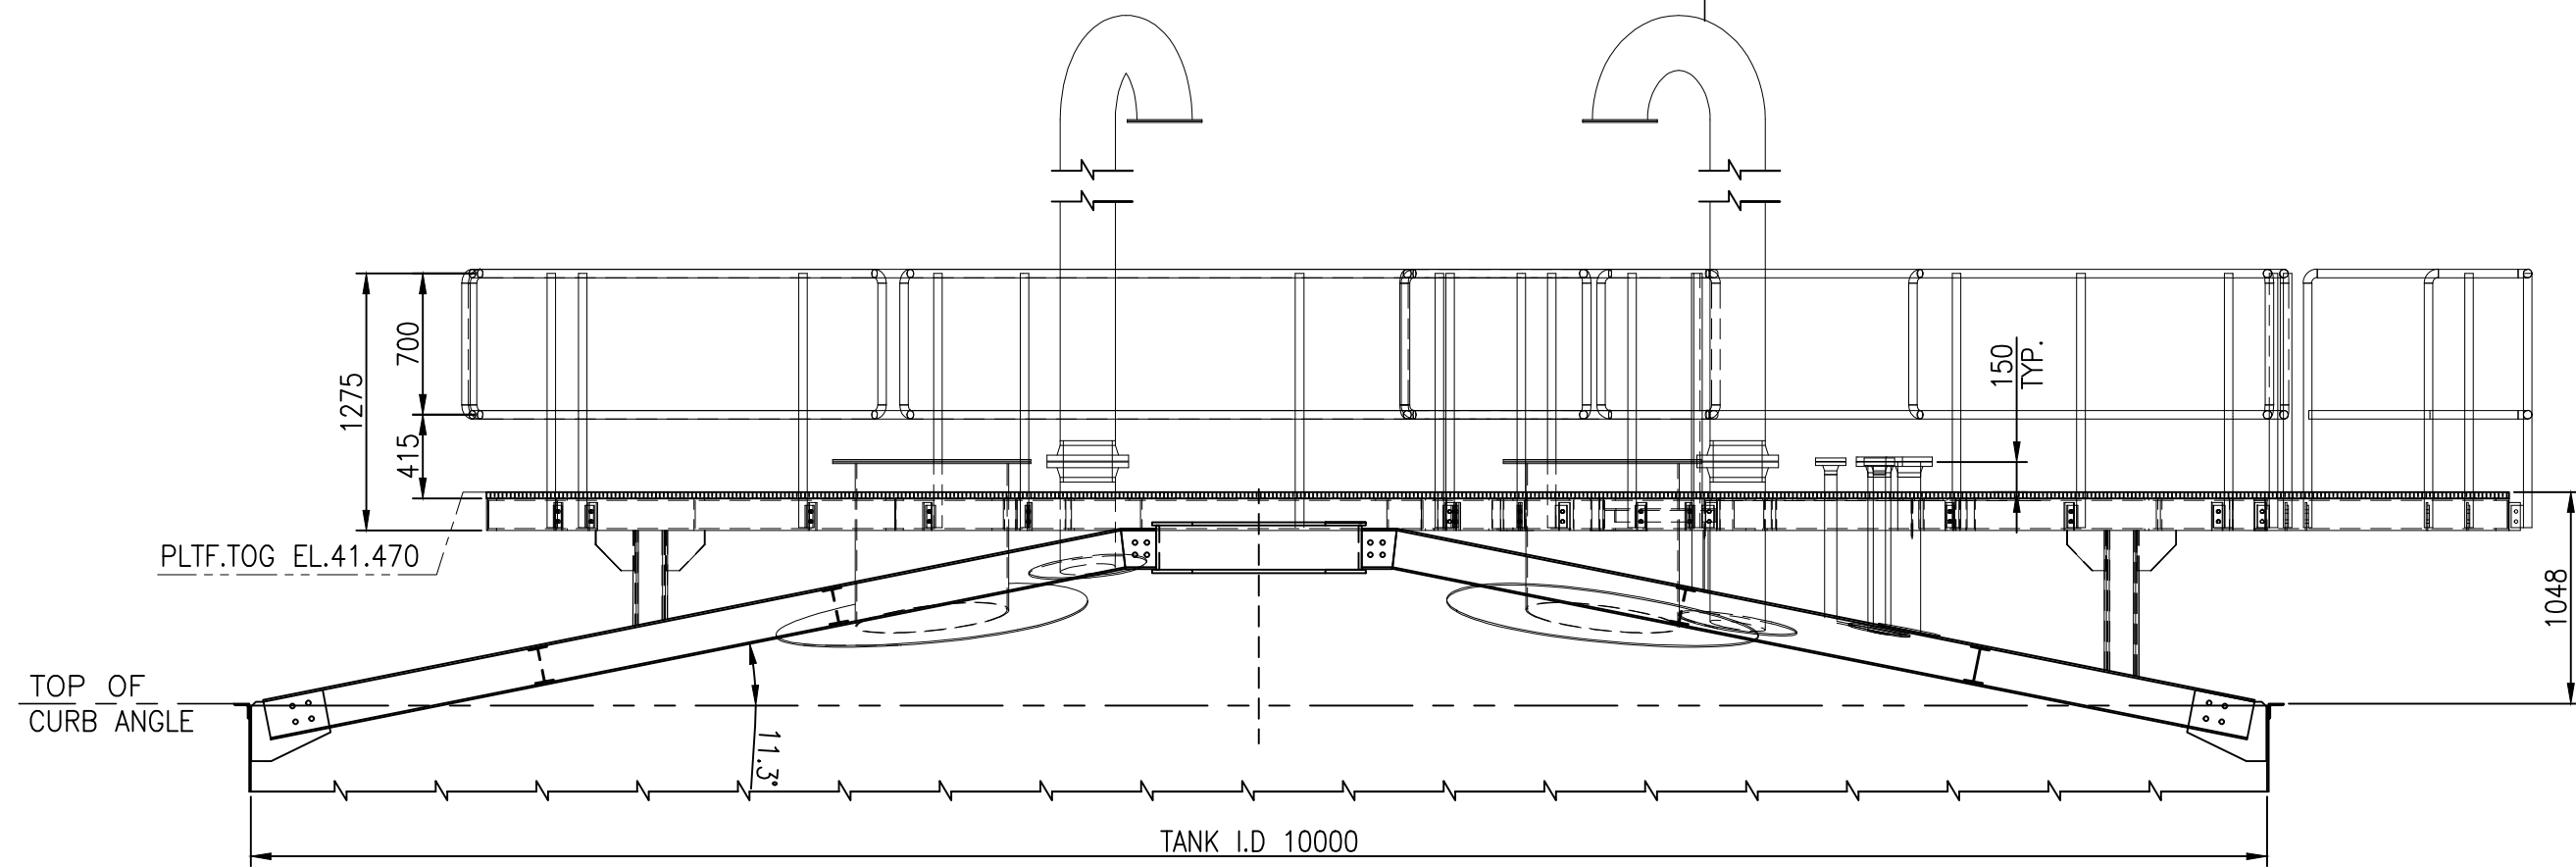

ELEVATION VIEW

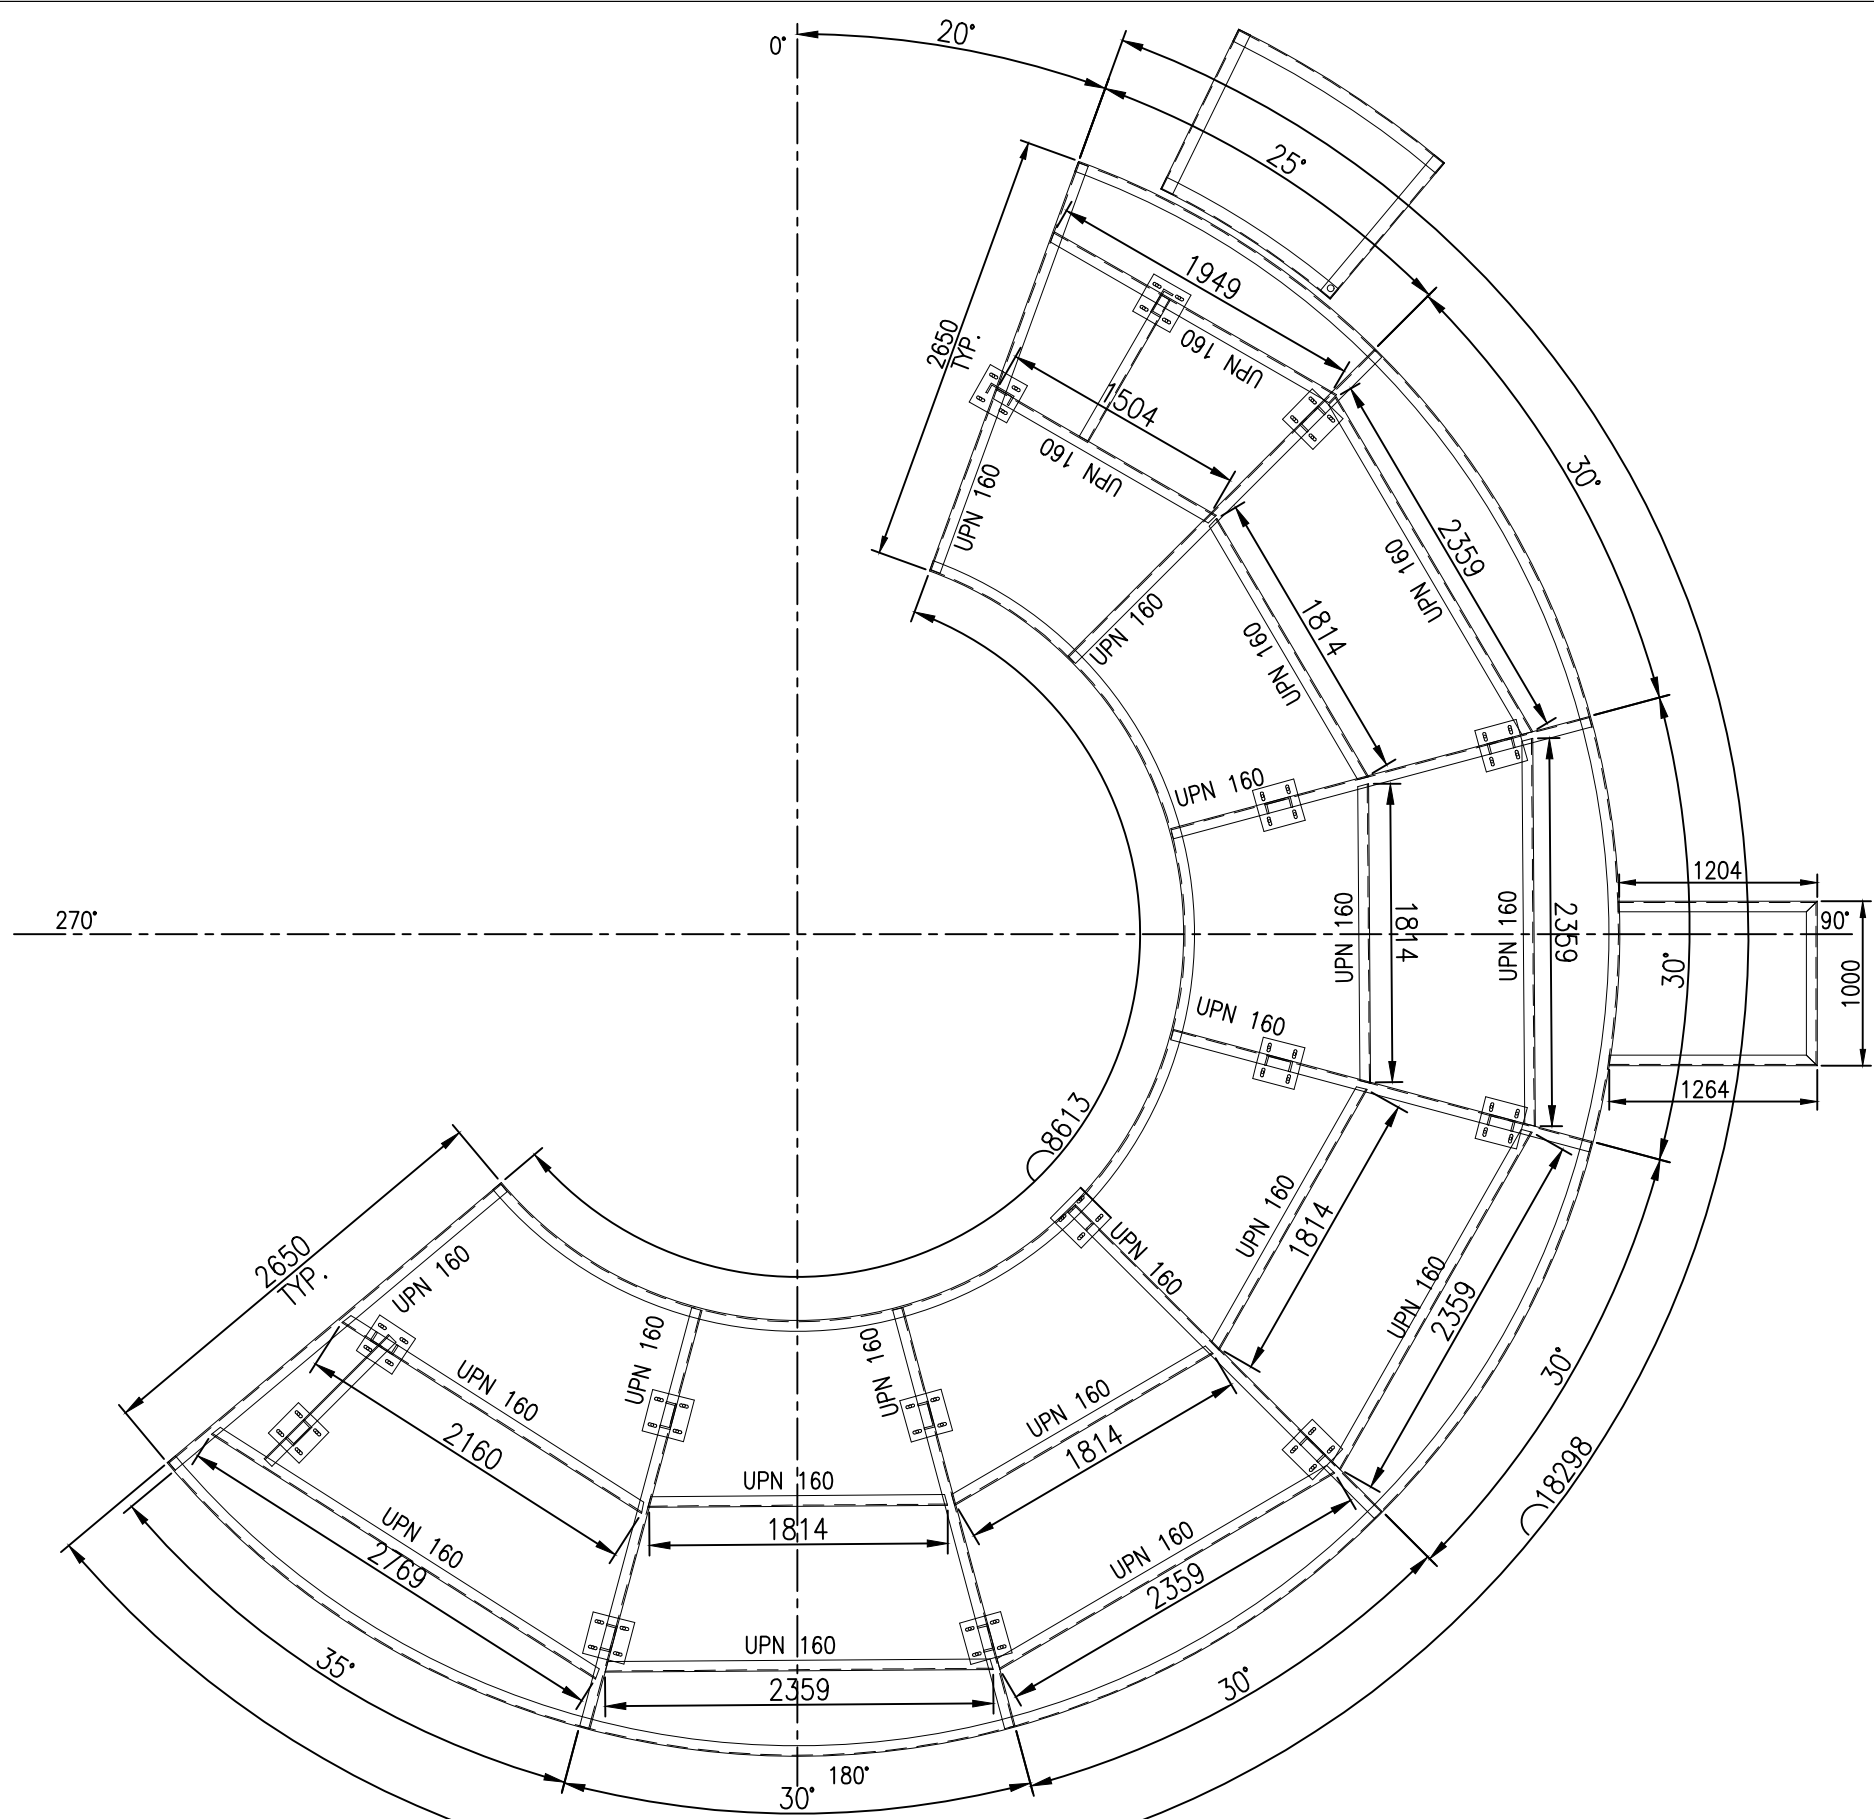

PLAN VIEW
PRIMARY & SECONDARY MEMBER DETAILS (PLATFORM-3)

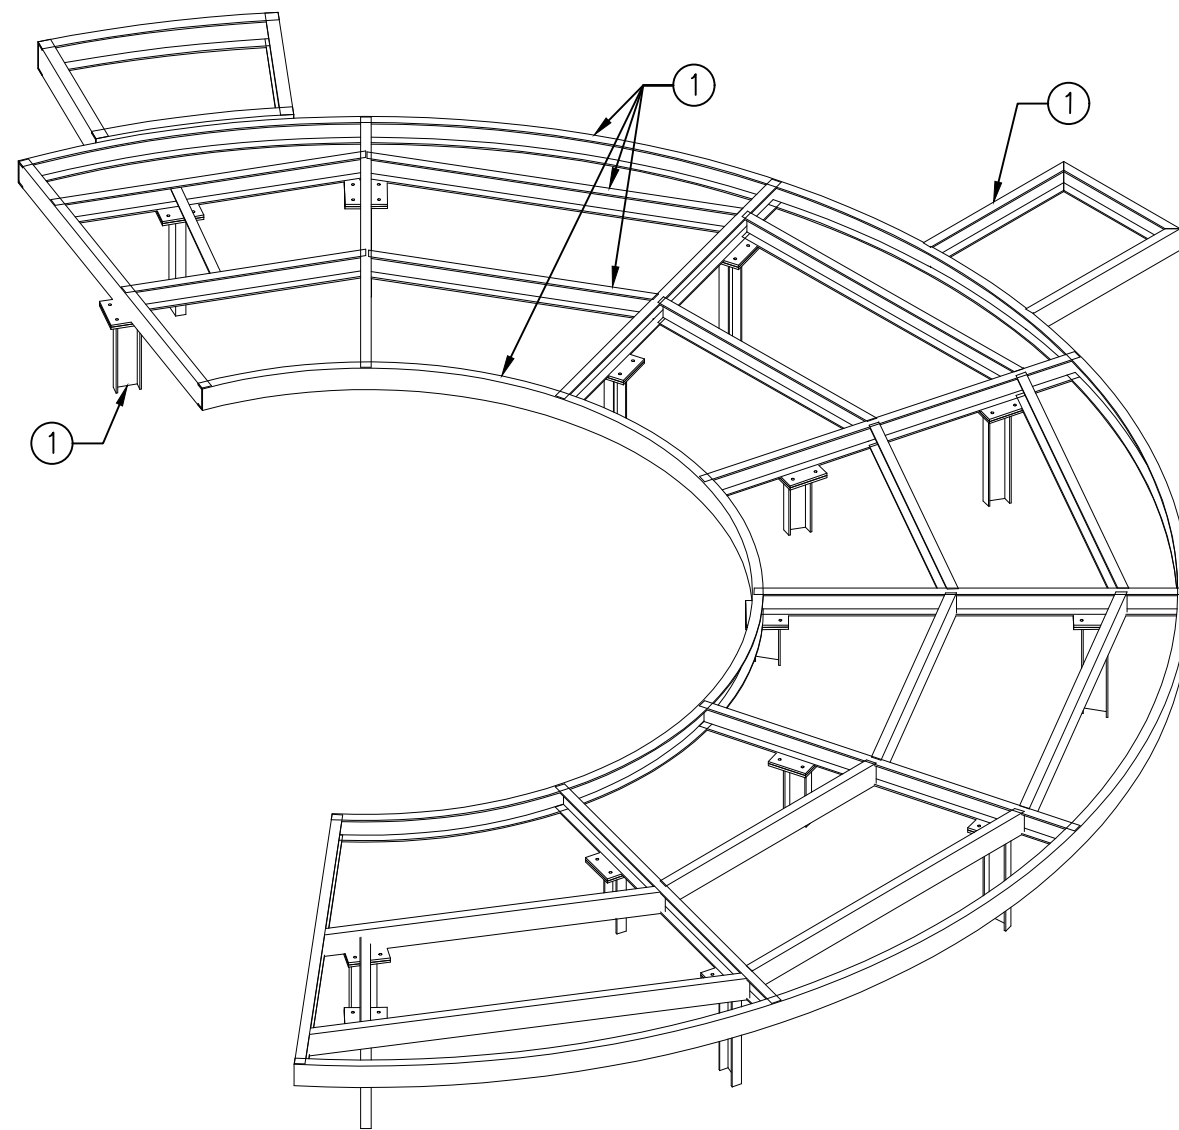

ISOMETRIC VIEW
PLATFORM - 3

00	07/10/2025	IFR	ISSUED FOR REVIEW			SR	RJ	SP
Rev.	Date	Status	Revision Description			Iss.	Check.	Appr.

This document is the property of the TOTAL GROUP and it shall not be disclosed to third parties or reproduced without the express written permission of the TOTAL GROUP.
This document has been generated by an Electronic Document Management System. When printed it shall be considered as "for information only". The controlled copy is the EDMS version and it is document holder's responsibility to make sure that latest version is in use.

Affiliate:	IRAQ	Site:	AG1	Project Phase:	DE
------------	------	-------	-----	----------------	----






CENTRAL PROCESSING FACILITIES

ROOF WALKWAY WITH HANDRAIL DETAIL DRAWING FOR









REJECT WATER TANK (TAG NO. B0-T-54-0006)

Discipline:	PVV	Doc. Type:	GEA	Sector:	B0	System:	7/77
Company Doc. N°:	IQ-AG1-B0-MIC3-000042			Class:	2	Scale:	1:500
Contractor Doc. N°:	MIC-01009.10-DRG-028			Format:	A1	Folio:	1 of 6


	14		15		16
--	----	--	----	--	----

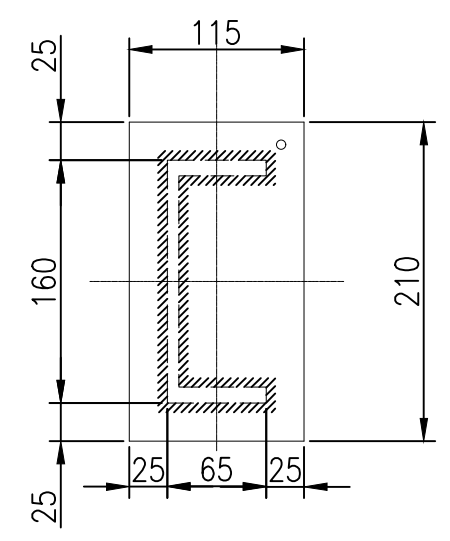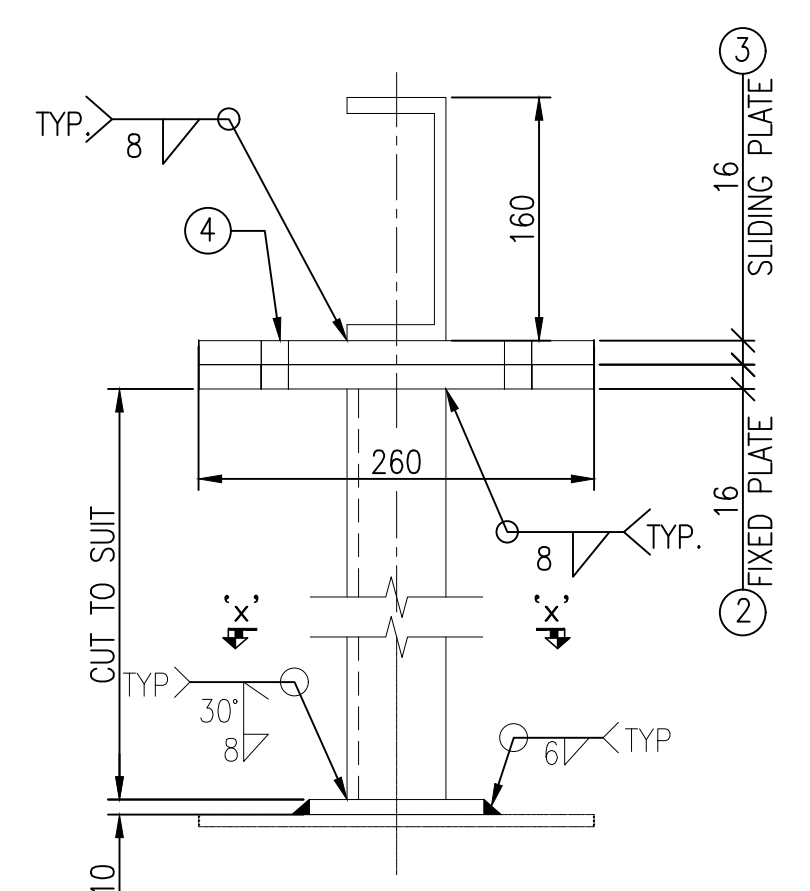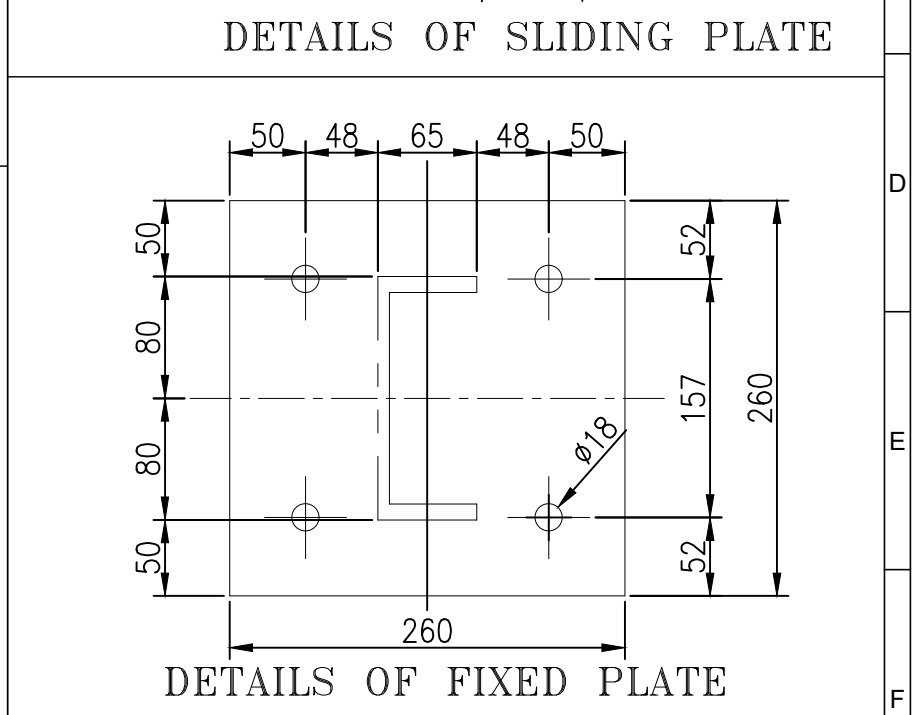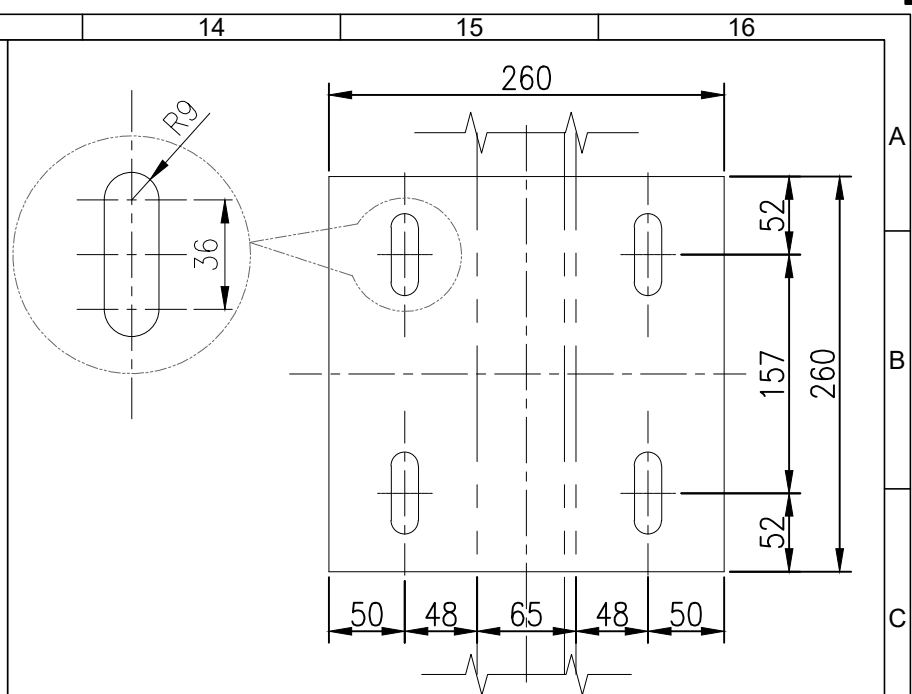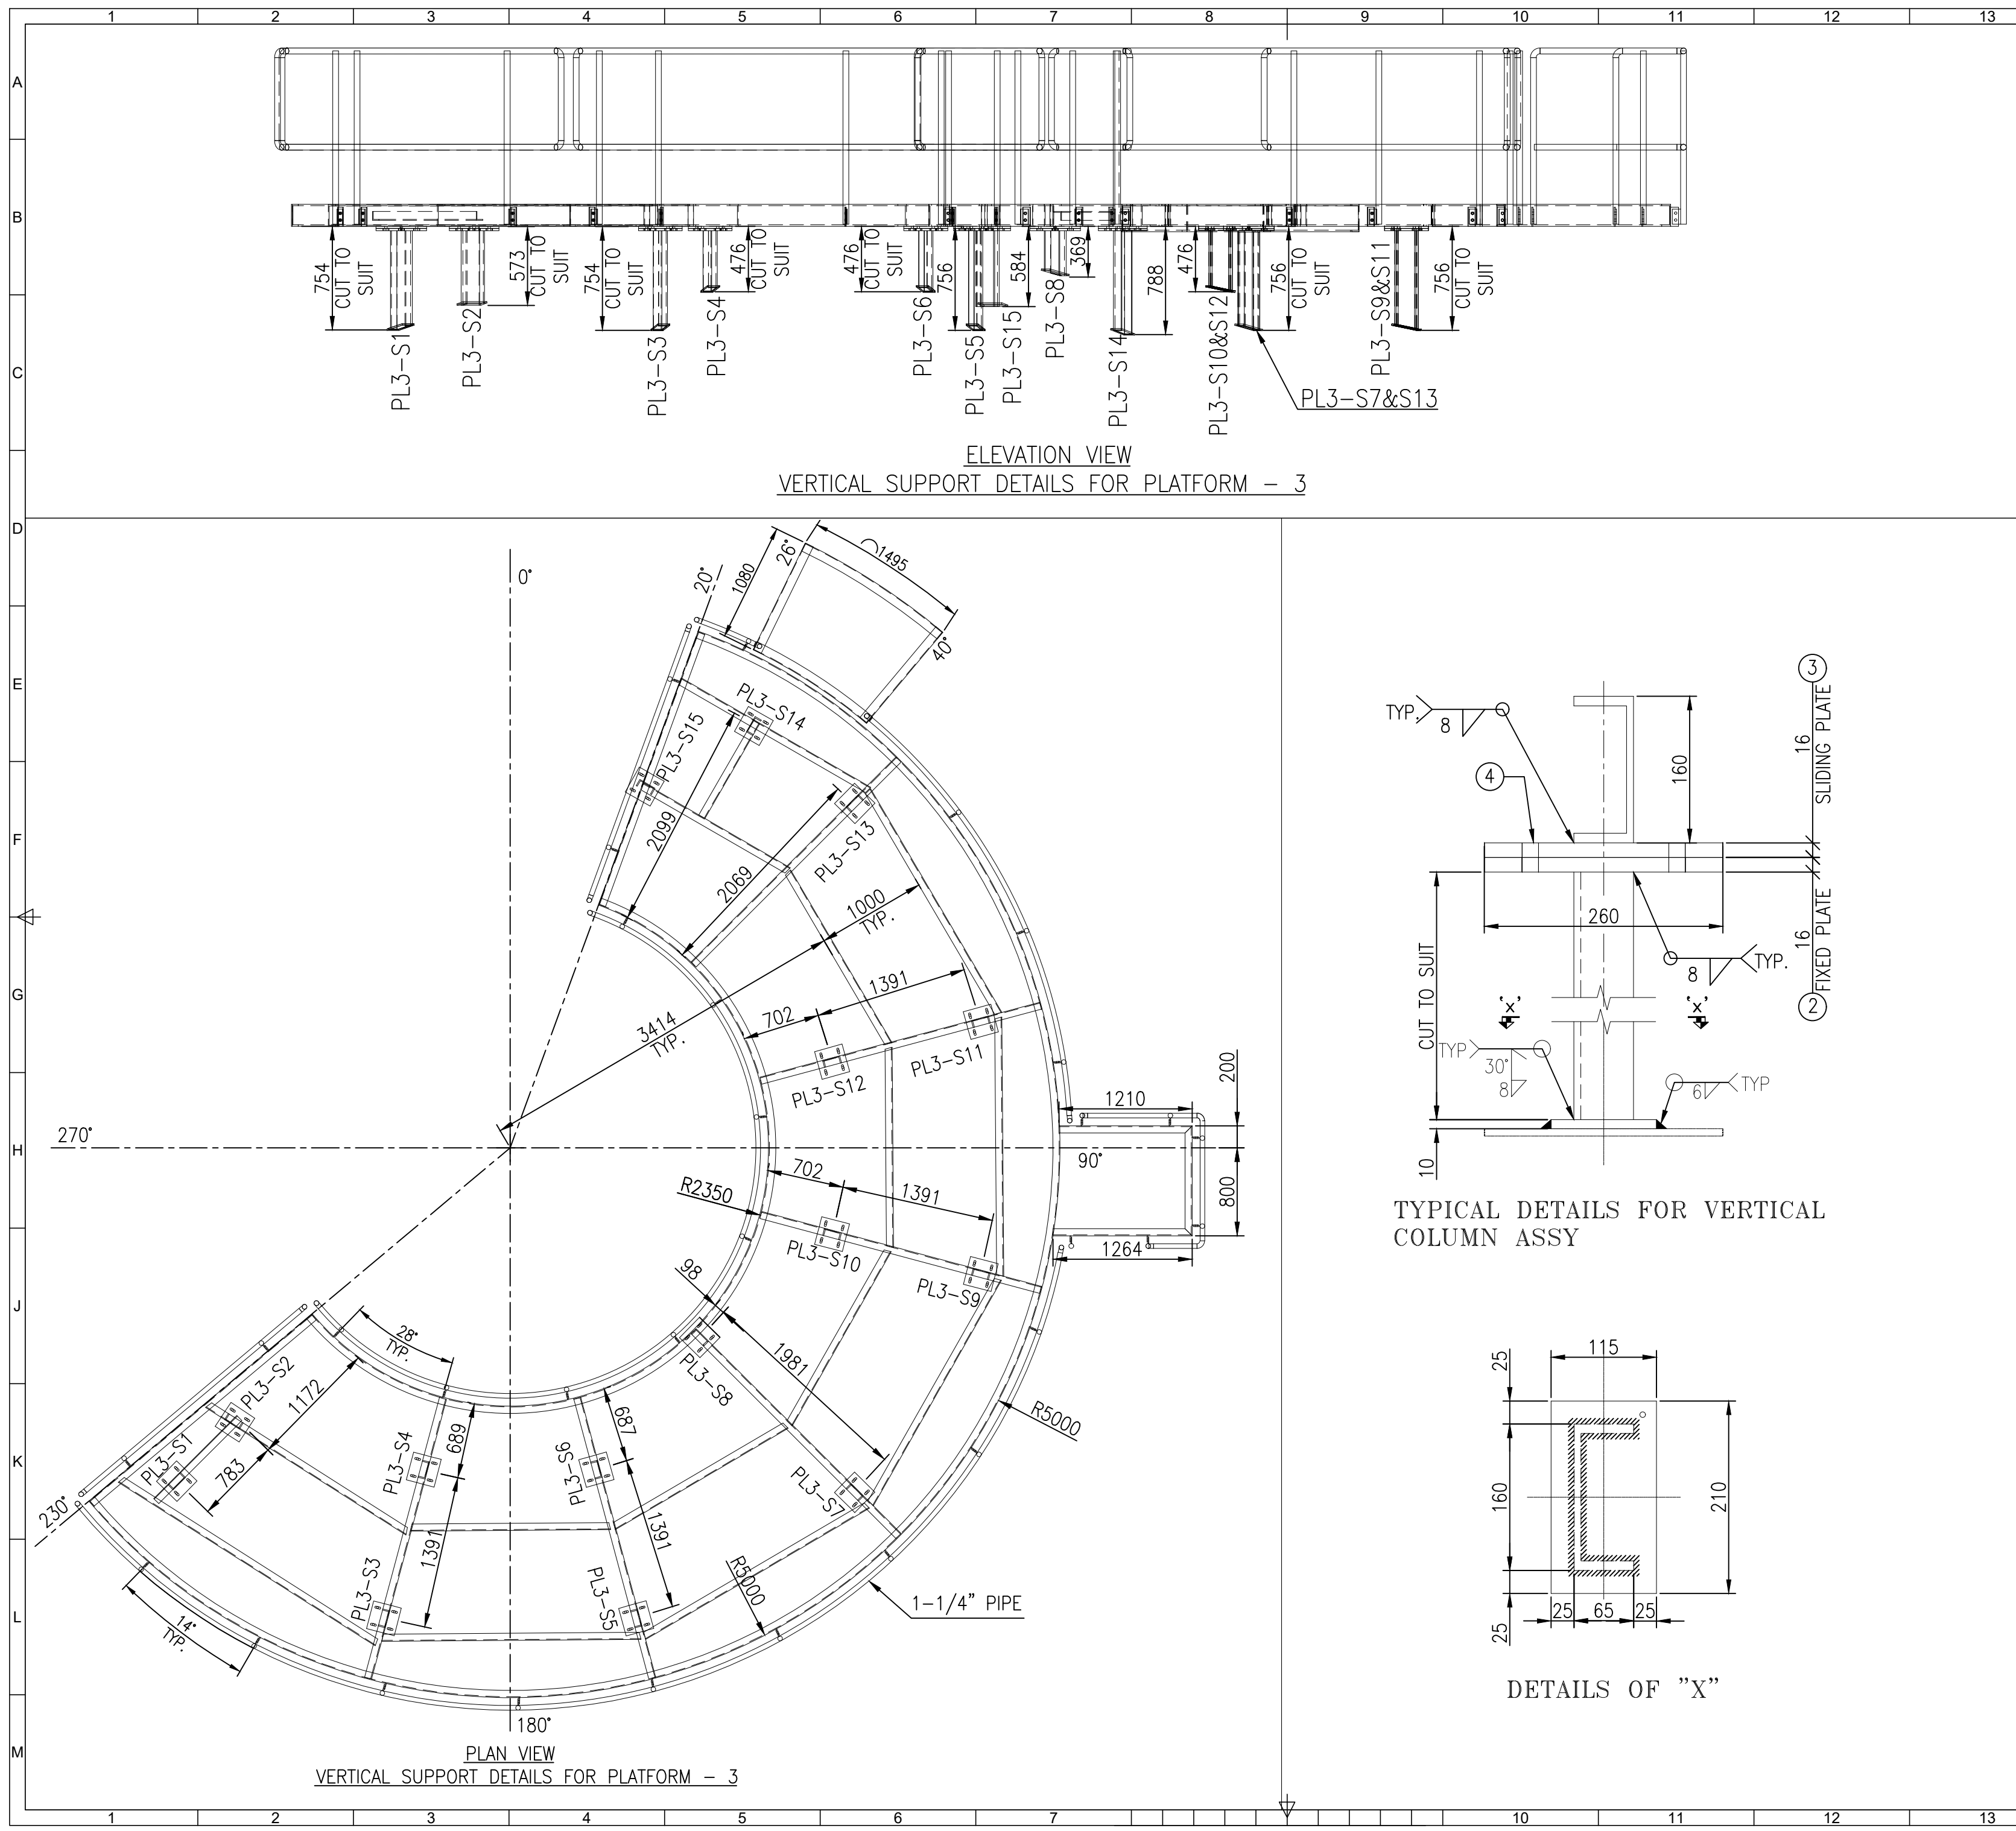


00	07/10/2025	IFR	ISSUED FOR REVIEW	SR	RJ	SP
Rev.	Date	Status	Revision Description	Iss.	Check.	Appr.
			PROJECT NAME & LOGO	CONTRACTOR NAME & LOGO		
				More in: www.ti.com/00009.com		
This document is the property of the TOTAL GROUP and it shall not be disclosed to third parties or reproduced without the express written permission of the TOTAL GROUP.						
This document has been generated by an Electronic Document Management System. When printed it shall be considered as "for information only". The controlled copy is the EDMS version and it is document holder's responsibility to make sure that latest version is in use.						
Affiliate: IRAQ		Site: AG1		Project Phase: DE		
CENTRAL PROCESSING FACILITIES						
ROOF WALKWAY WITH HANDRAIL DETAIL DRAWING FOR						
REJECT WATER TANK (TAG NO. B0-T-54-0006)						
Discipline:	PVV	Doc. Type:	GEA	Sector:	B0	System: 7/77
Company Doc. N°:		IQ-AG1-B0-MIC3-000042		Class:	2	Scale: 1:500
Contractor Doc. N°:		MIC-01009.10-DRG-028		Format:	A1	Folio: 2 of 6
14		15		16		

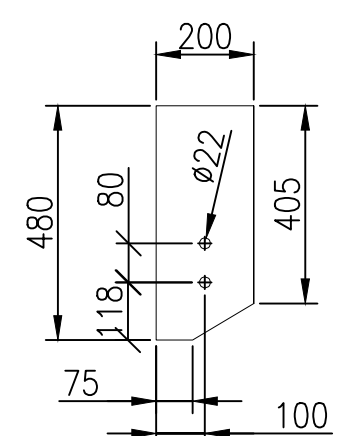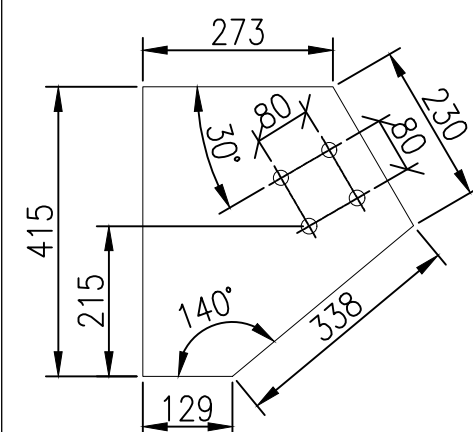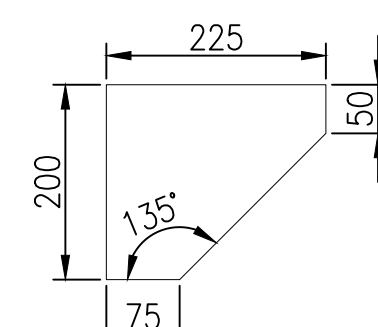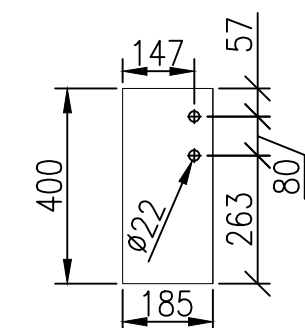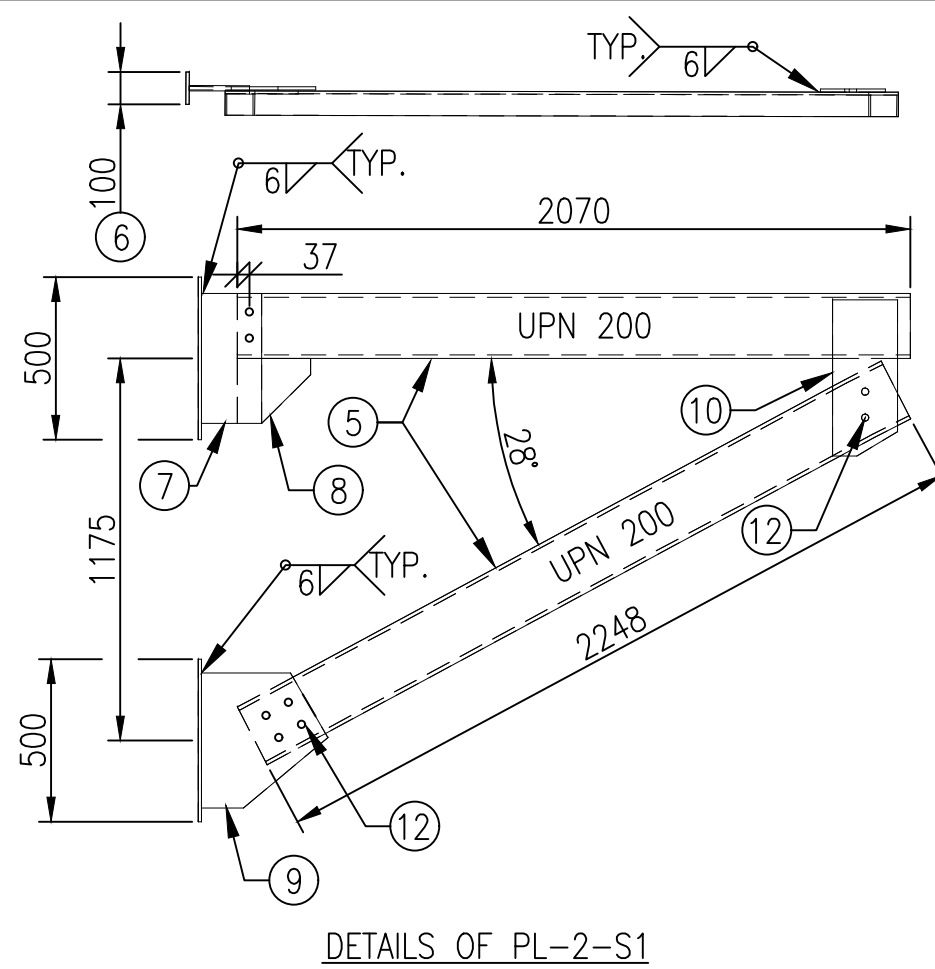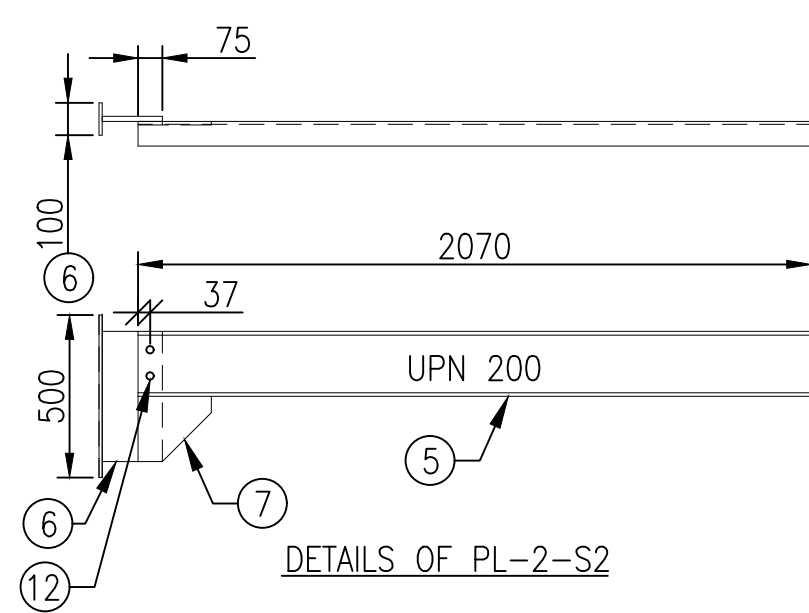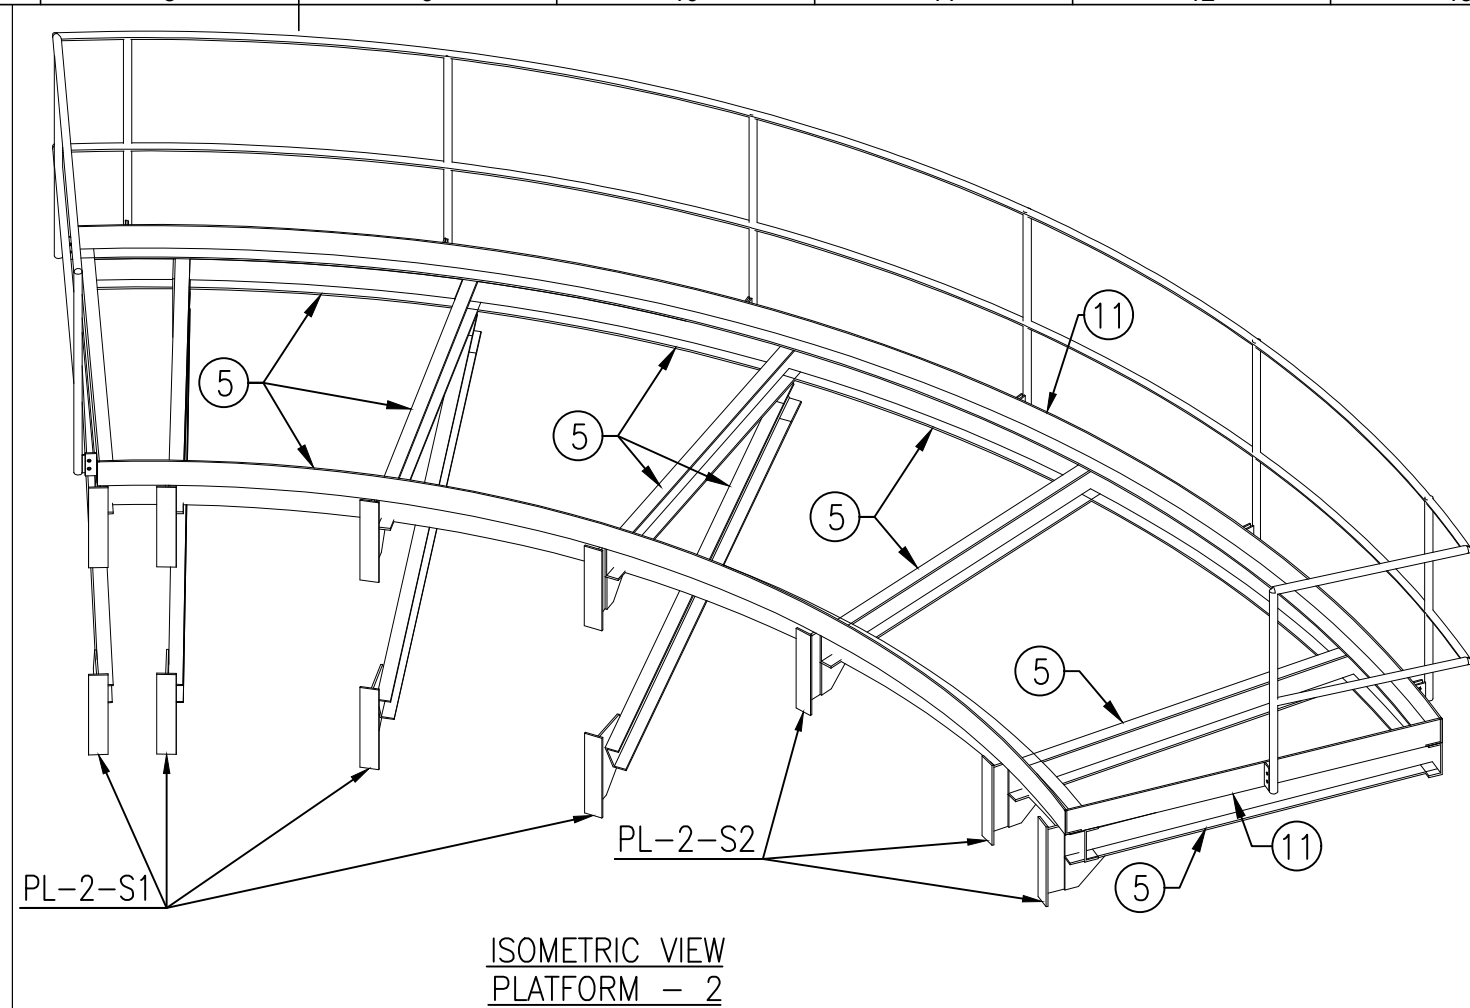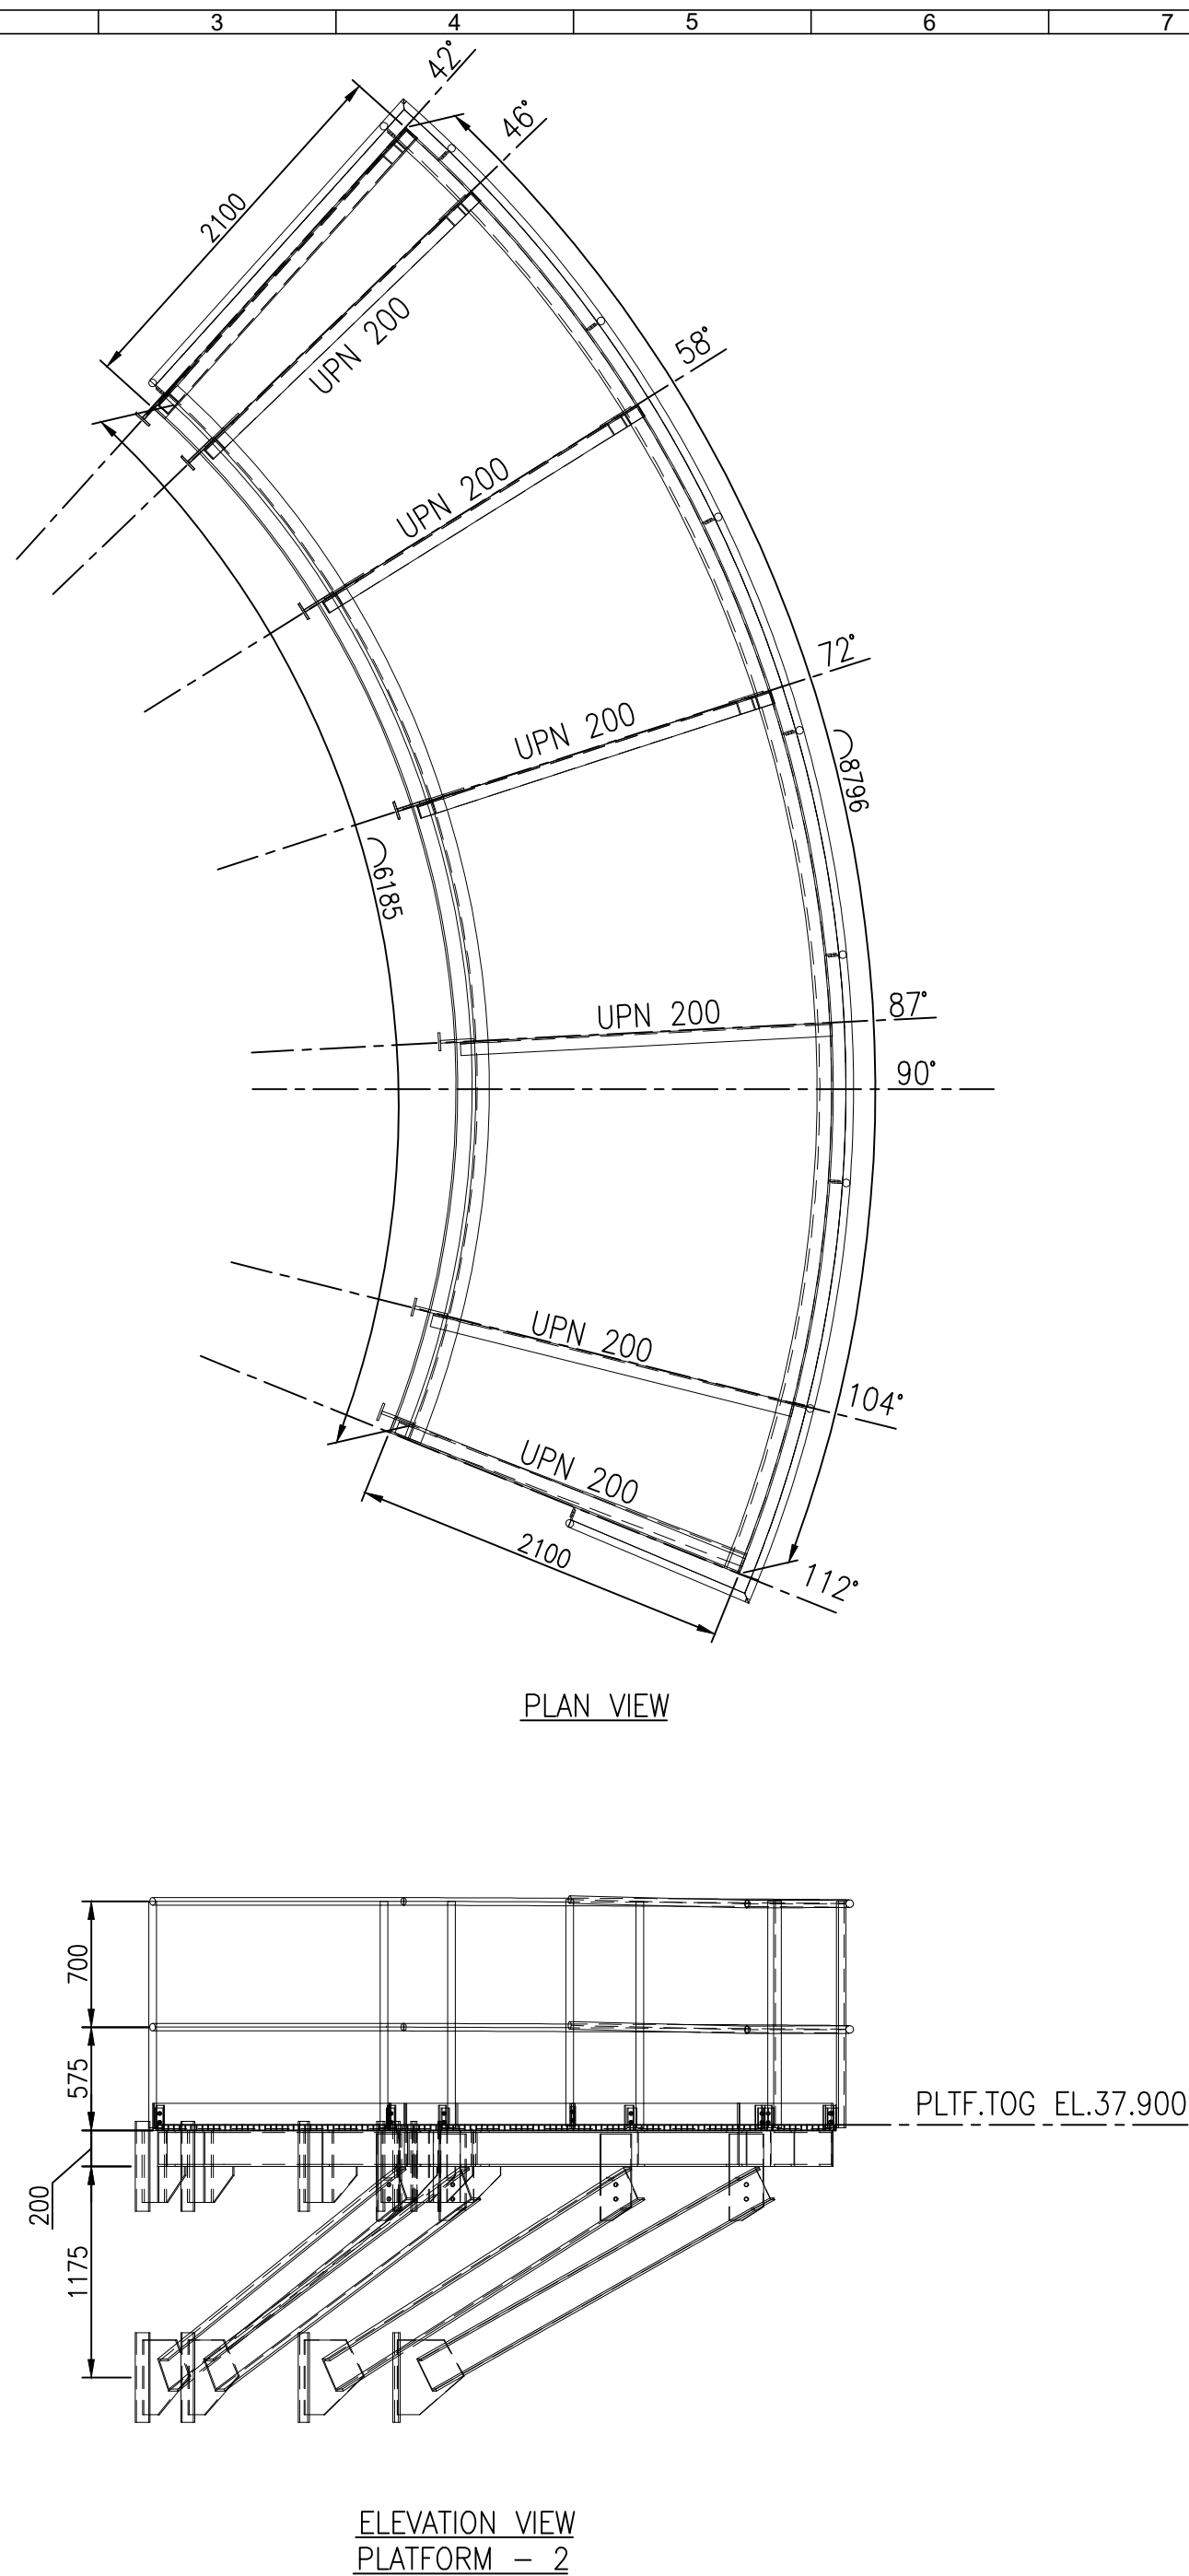

00	07/10/2025	IFR	ISSUED FOR REVIEW		SR	RJ	SP
Rev.	Date	Status	Revision Description		Iss.	Check.	Appr.
This document is the property of the TOTAL GROUP and it shall not be disclosed to third parties or reproduced without the express written permission of the TOTAL GROUP. This document has been generated by an Electronic Document Management System. When printed it shall be considered as "for information only". The controlled copy is the EDMS version and it is document holder's responsibility to make sure that latest version is in use.							
Affiliate:		IRAQ	Site:	AG1	Project Phase:	DE	
CENTRAL PROCESSING FACILITIES							
ROOF WALKWAY WITH HANDRAIL DETAIL DRAWING FOR							
REJECT WATER TANK (TAG NO. B0-T-54-0006)							
Discipline:	PVV	Doc. Type:	GEA	Sector:	B0	System:	7/77
Company Doc. N°:	IQ-AG1-B0-MIC3-000042			Class:	2	Scale:	1:500
Contractor Doc. N°:	MIC-01009.10-DRG-028			Format:	A1	Folio:	3 of 6
		14			15		
						16	

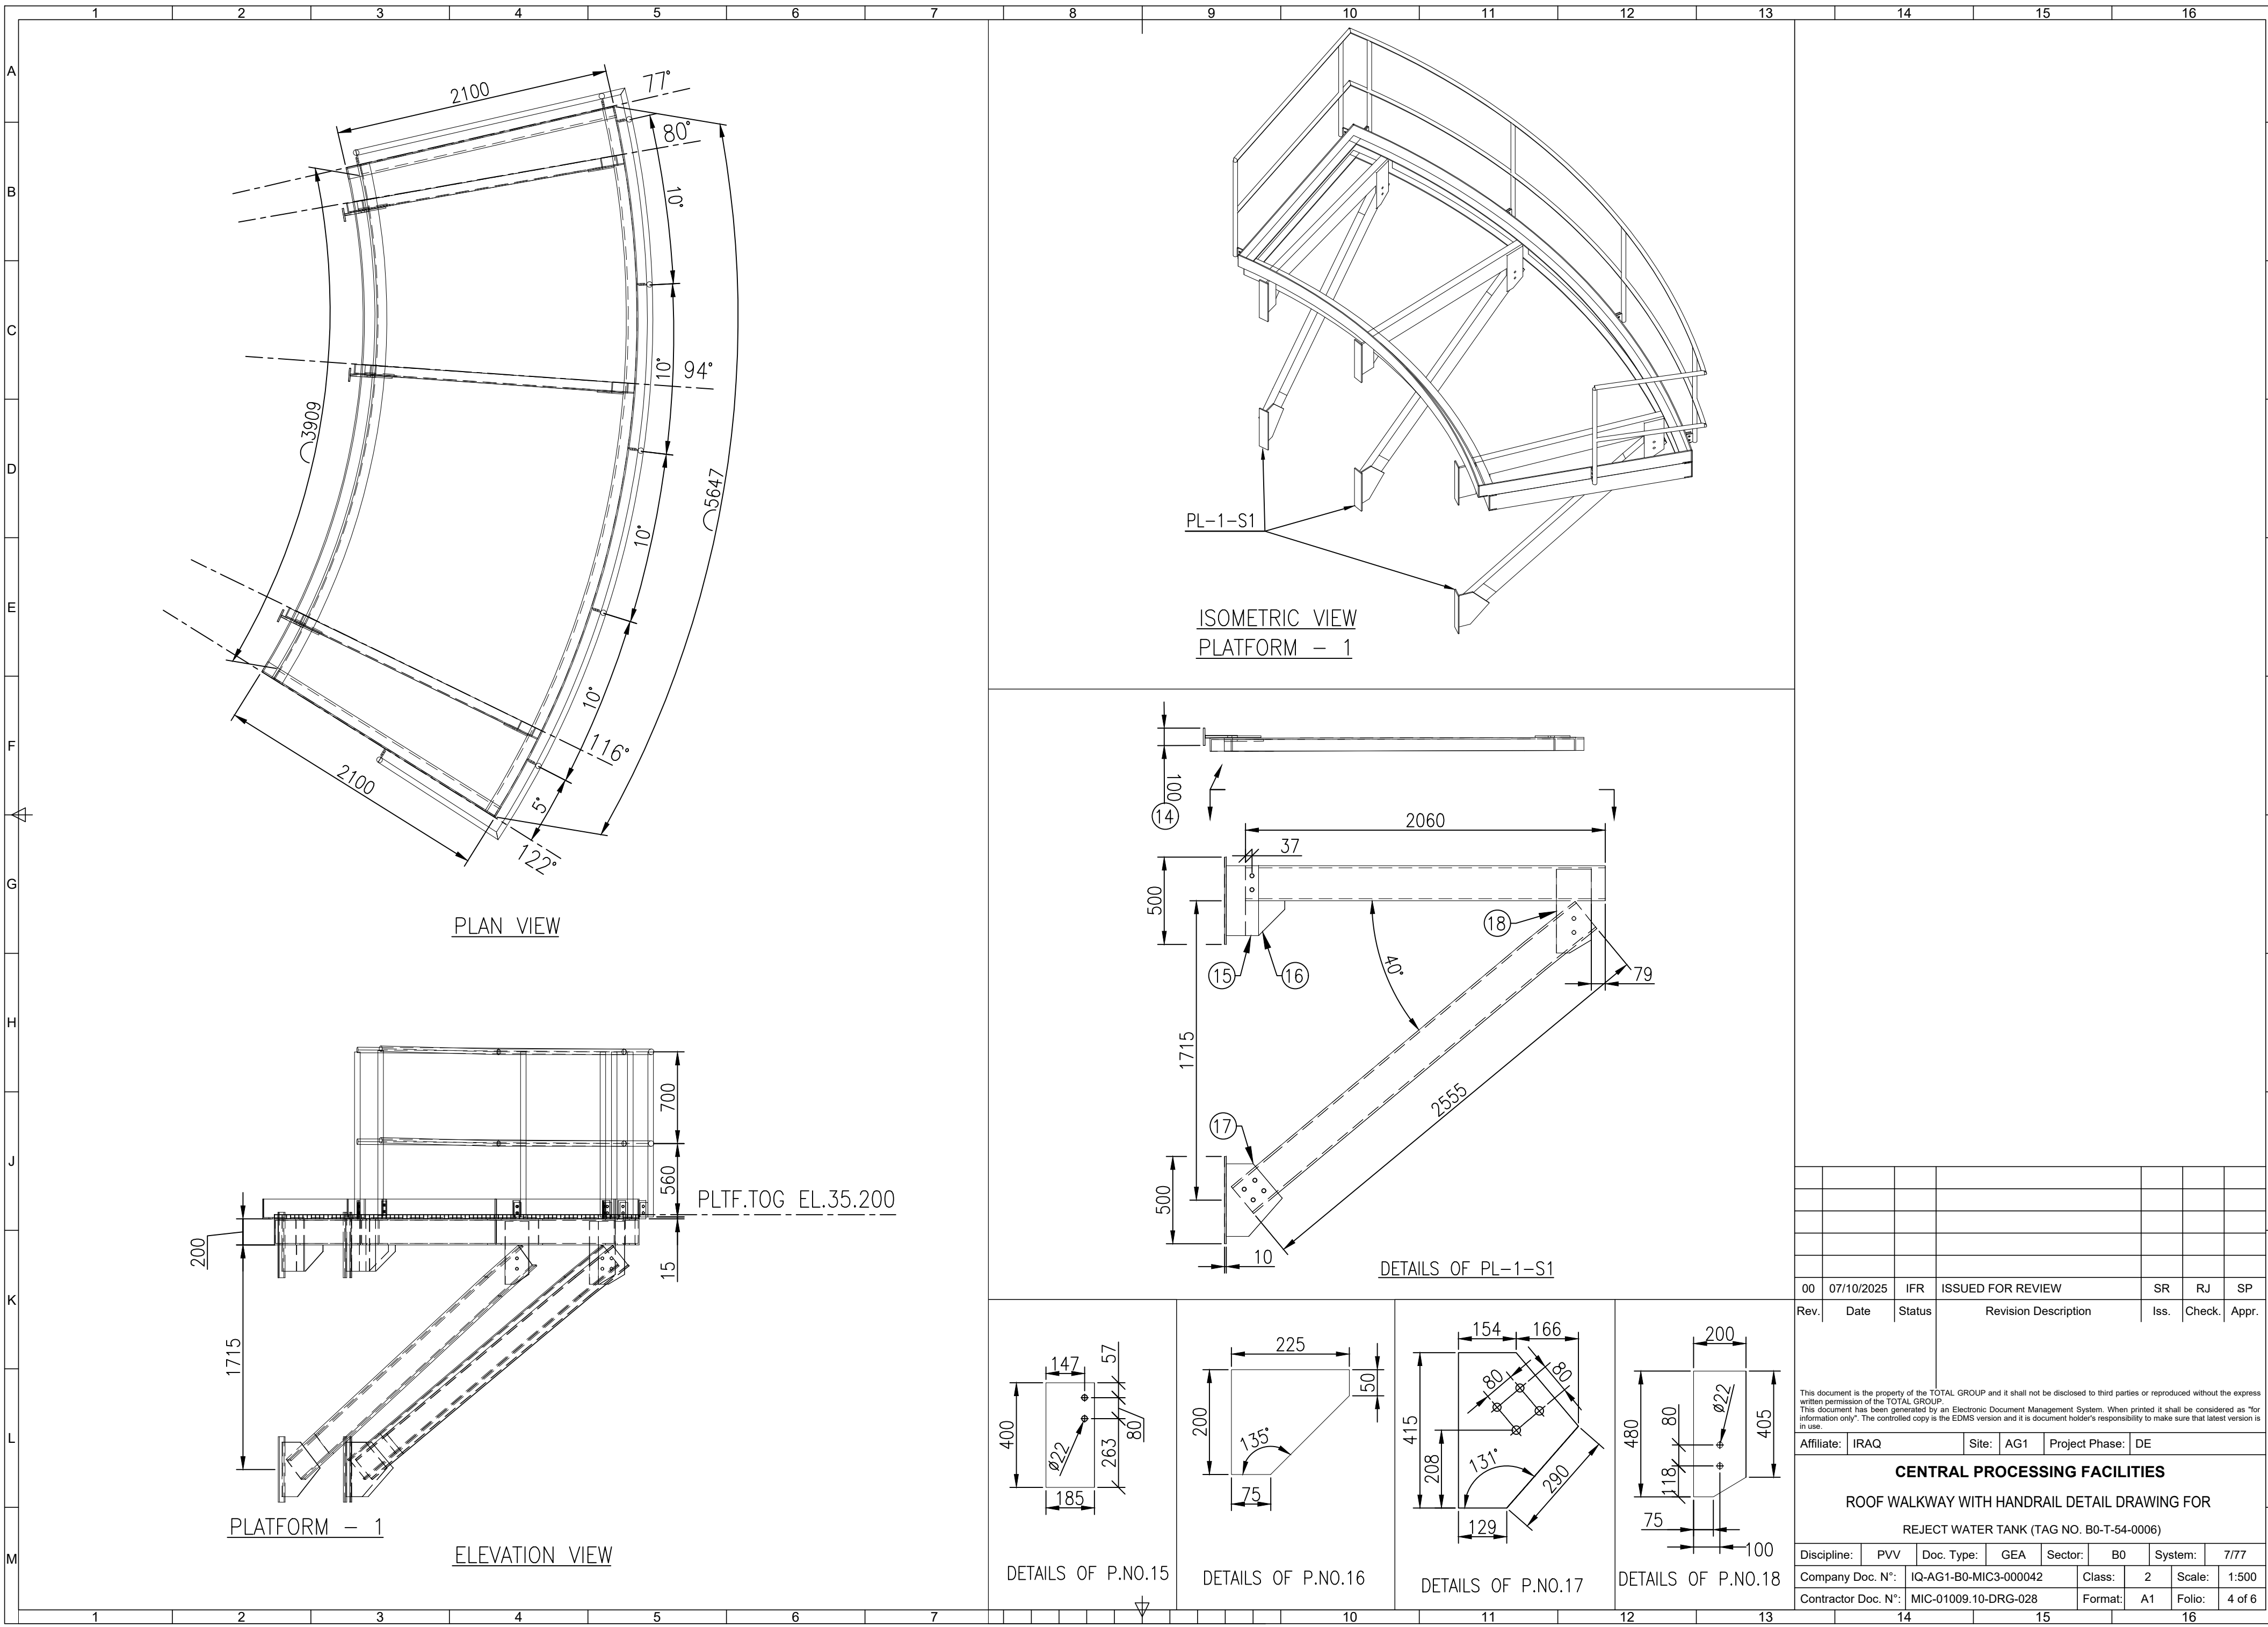

00	07/10/2025	IFR	ISSUED FOR REVIEW	SR	RJ	SP
Rev.	Date	Status	Revision Description	Iss.	Check.	Appr.
This document is the property of the TOTAL GROUP and it shall not be disclosed to third parties or reproduced without the express written permission of the TOTAL GROUP. This document has been generated by an Electronic Document Management System. When printed it shall be considered as "for information only". The controlled copy is the EDMS version and it is document holder's responsibility to make sure that latest version is in use.						
Affiliate:	IRAQ	Site:	AG1	Project Phase:	DE	
CENTRAL PROCESSING FACILITIES						
ROOF WALKWAY WITH HANDRAIL DETAIL DRAWING FOR						
REJECT WATER TANK (TAG NO. B0-T-54-0006)						
Discipline:	PVV	Doc. Type:	GEA	Sector:	B0	System:
Company Doc. N°:	IQ-AG1-B0-MIC3-000042	Class:	2	Scale:	1:500	7/77
Contractor Doc. N°:	MIC-01009.10-DRG-028	Format:	A1	Folio:	4 of 6	

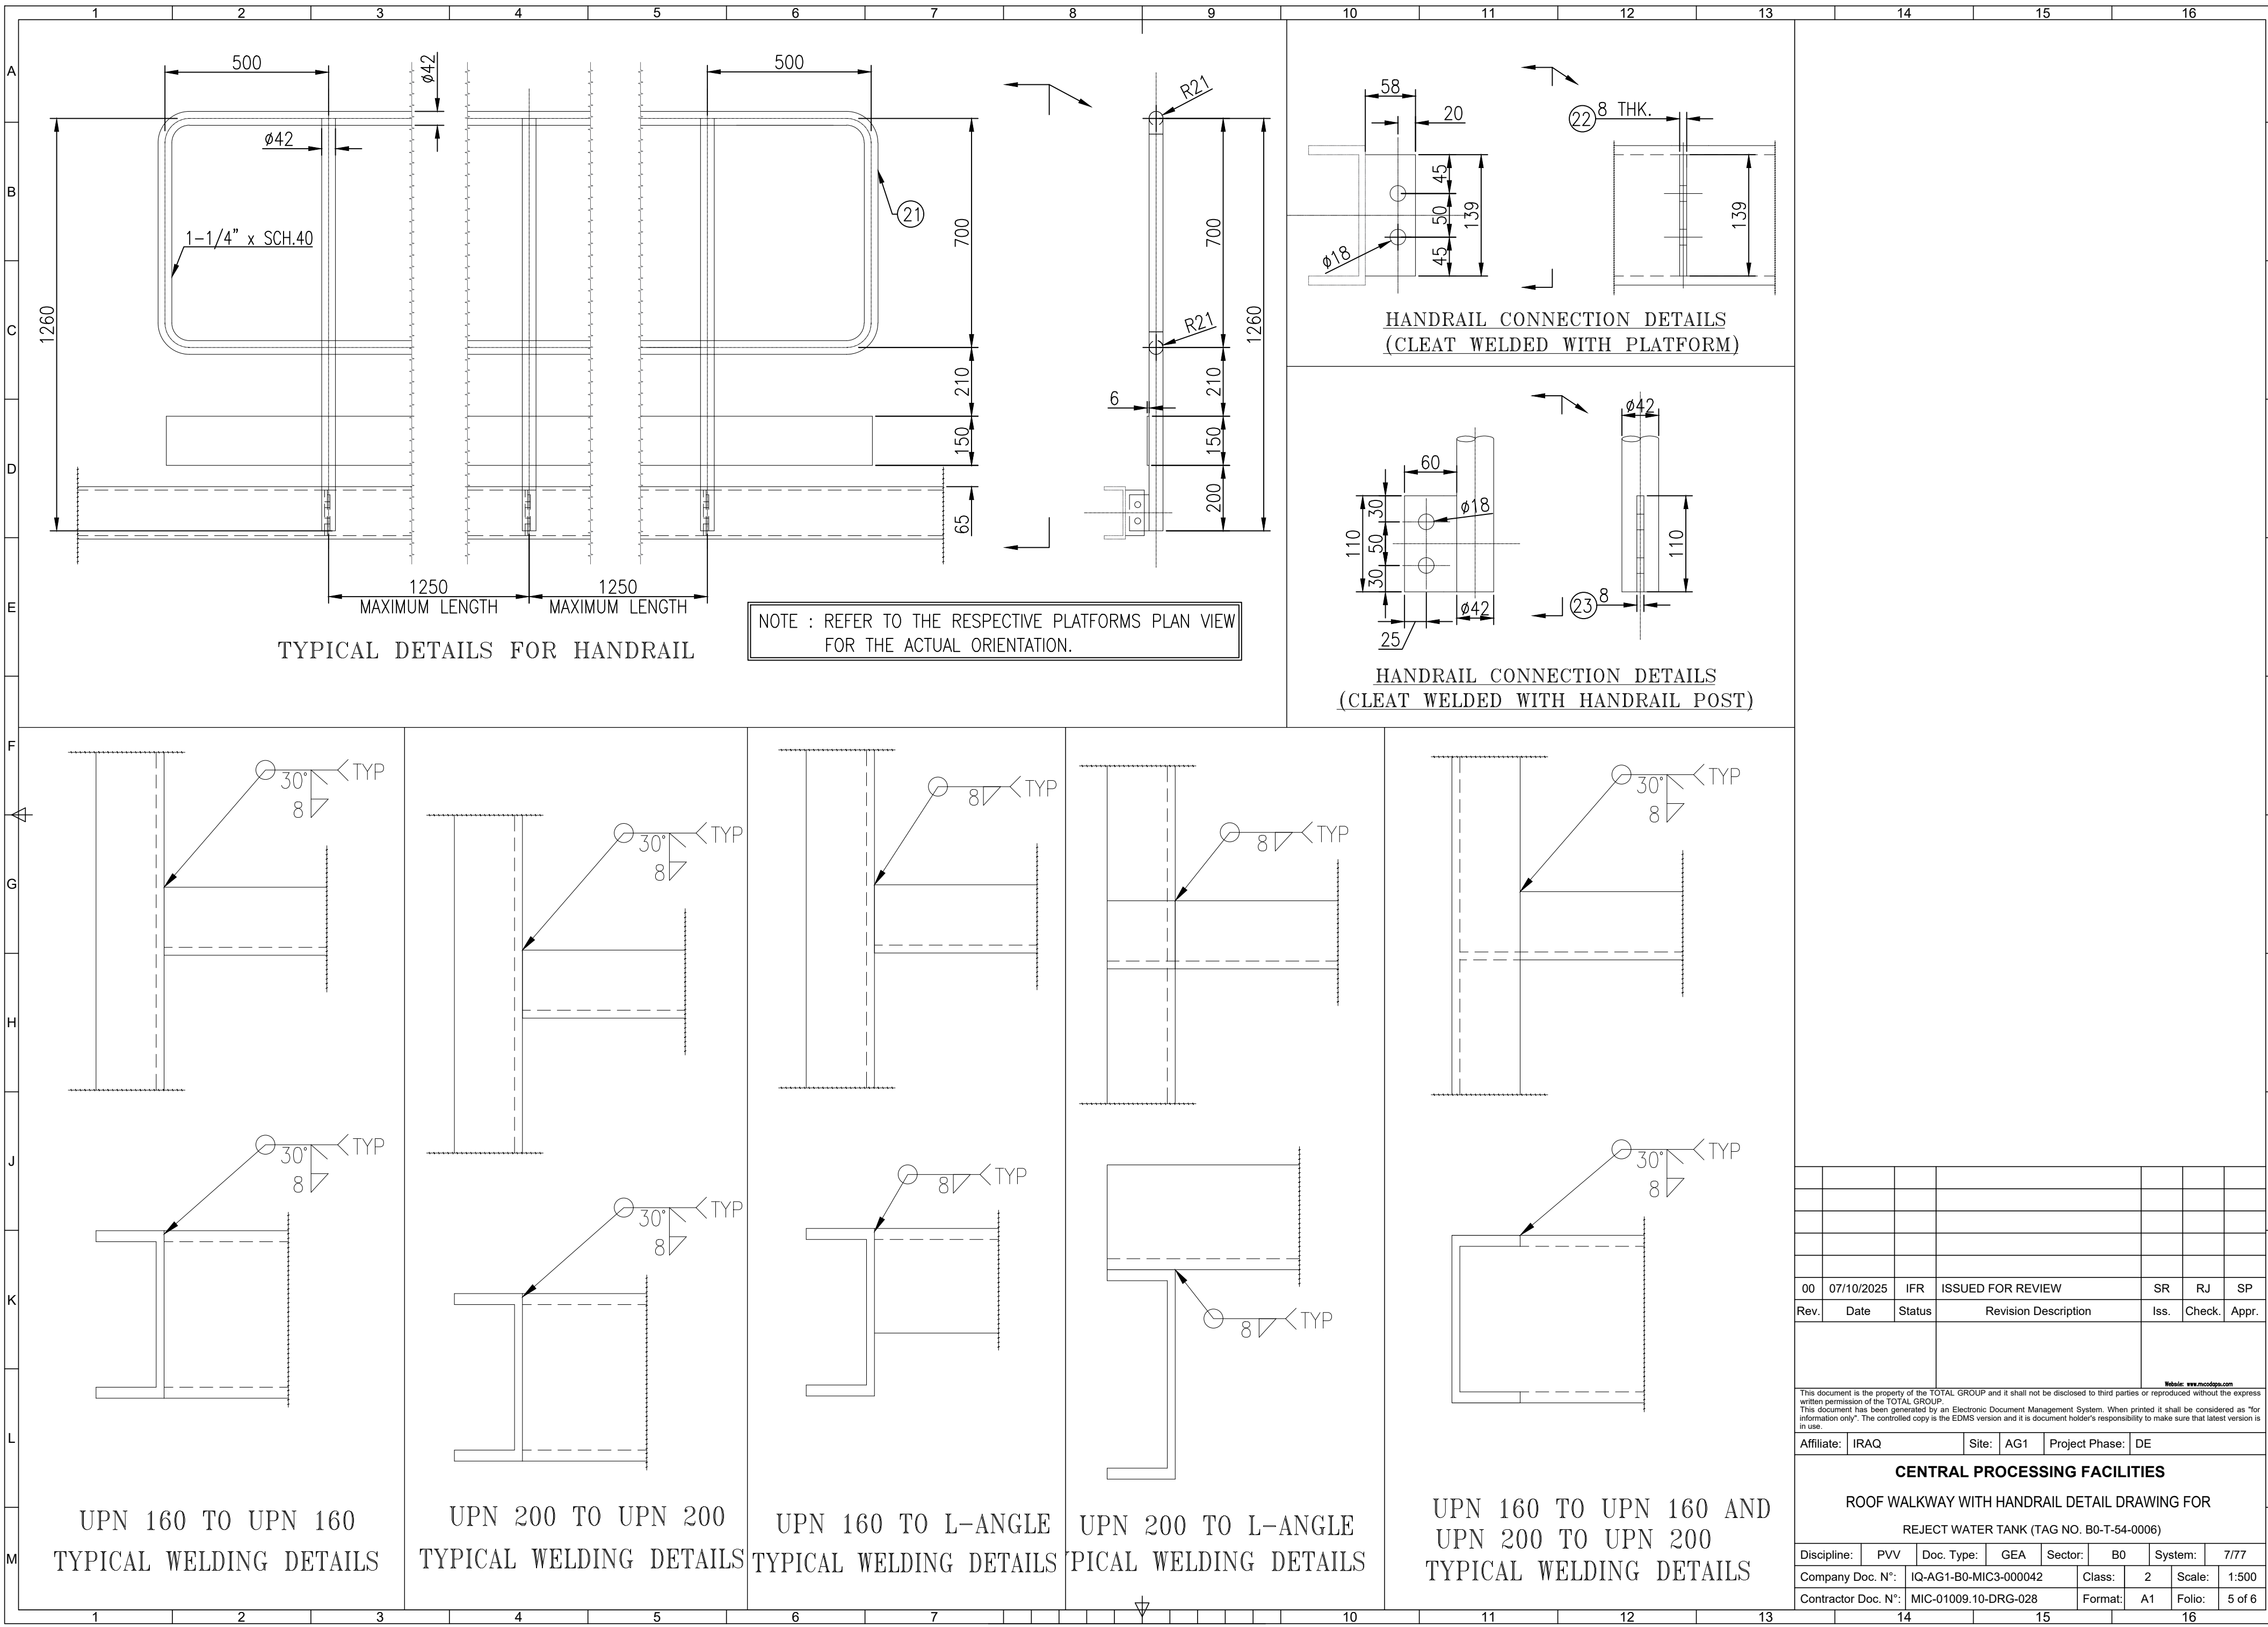

00	07/10/2025	IFR	ISSUED FOR REVIEW		SR	RJ	SP
Rev.	Date	Status	Revision Description		Iss.	Check.	Appr.
					Website: www.mccodgsa.com		
This document is the property of the TOTAL GROUP and it shall not be disclosed to third parties or reproduced without the express written permission of the TOTAL GROUP. This document has been generated by an Electronic Document Management System. When printed it shall be considered as "for information only". The controlled copy is the EDMS version and it is document holder's responsibility to make sure that latest version is in use.							
Affiliate:		IRAQ	Site:	AG1	Project Phase:	DE	
CENTRAL PROCESSING FACILITIES ROOF WALKWAY WITH HANDRAIL DETAIL DRAWING FOR REJECT WATER TANK (TAG NO. B0-T-54-0006)							
Discipline:		PVV	Doc. Type:	GEA	Sector:	B0	System: 7/77
Company Doc. N°:		IQ-AG1-B0-MIC3-000042			Class:	2	Scale: 1:500
Contractor Doc. N°:		MIC-01009.10-DRG-028			Format:	A1	Folio: 5 of 6

[illegible]