




GR-1

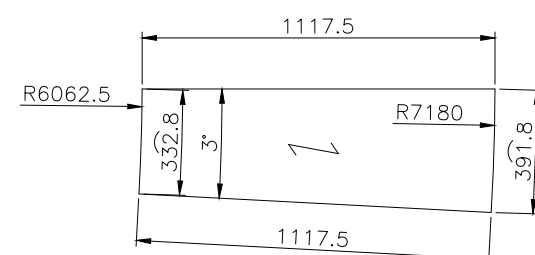


GR-2

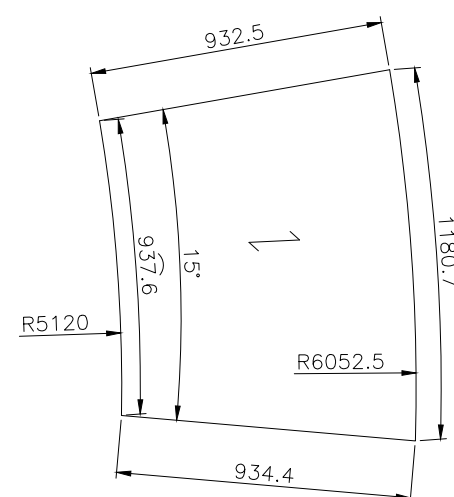


GR-3

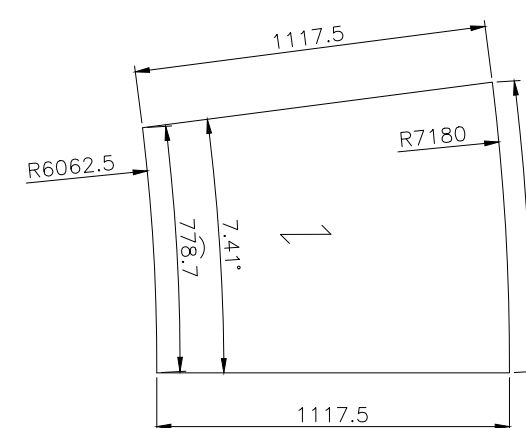


GR-4

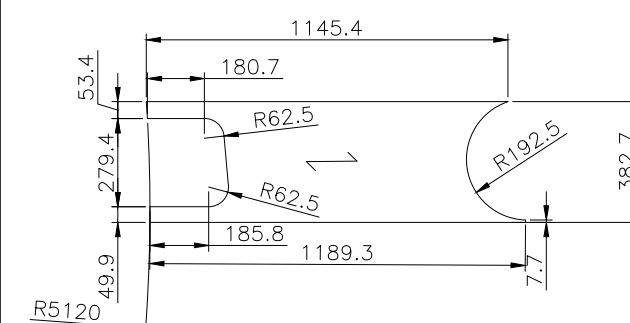


GR-5

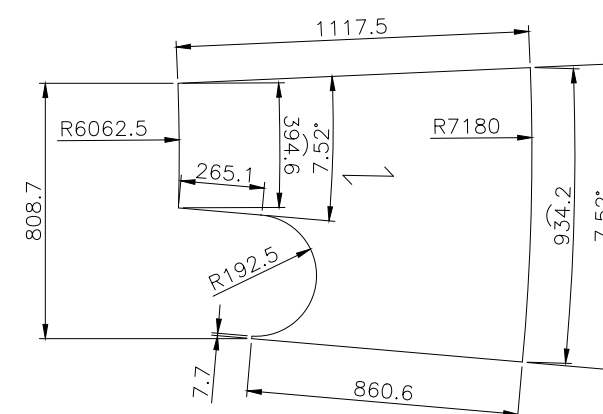


GR-6

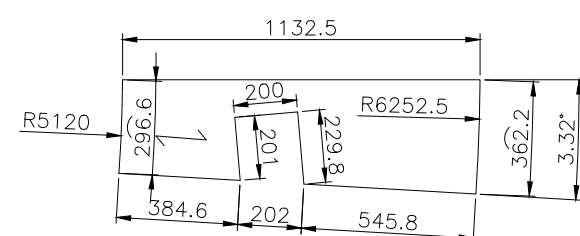


GR-7

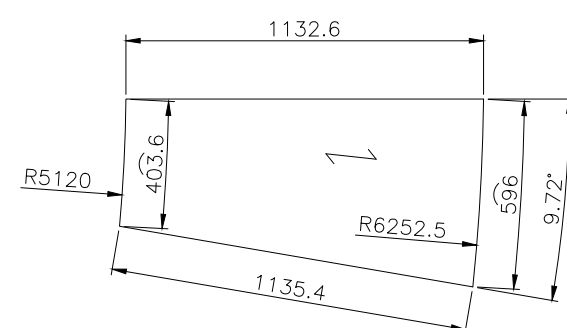


GR-8

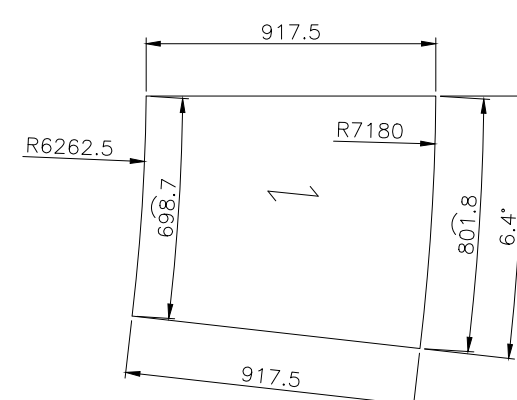


GR-9

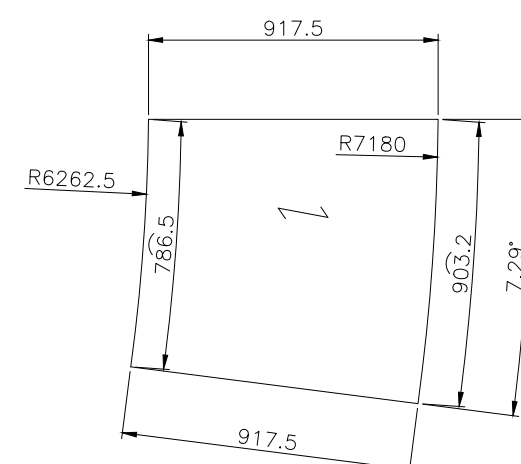


GR-10

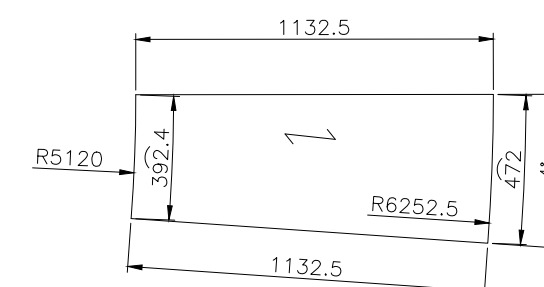


GR-11

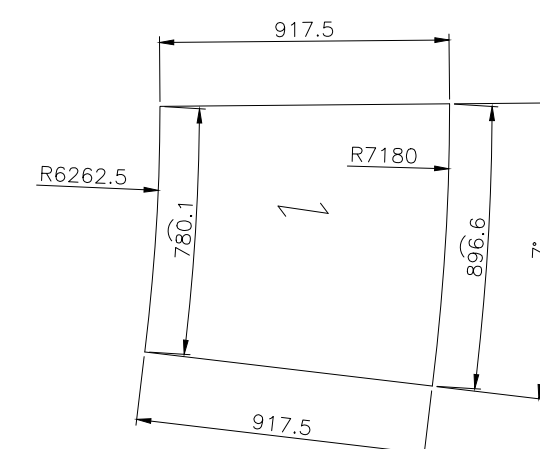


GR-12

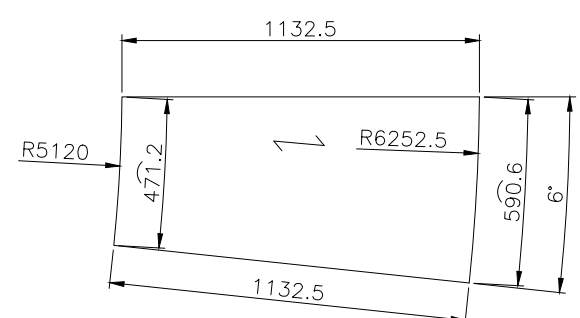


GR-13

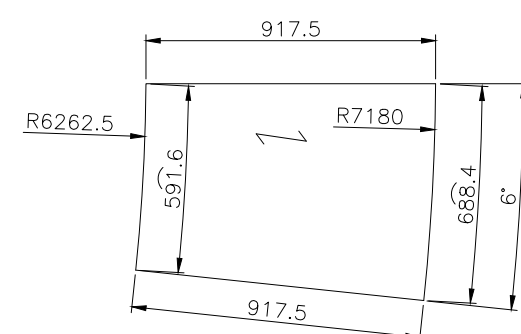


GR-14

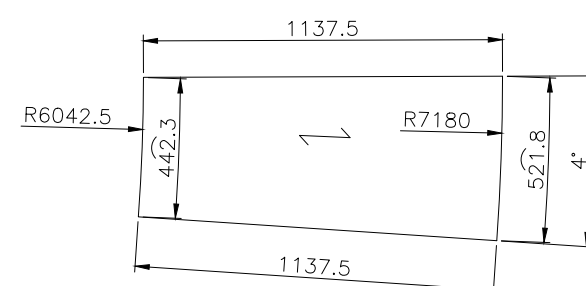


GR-15

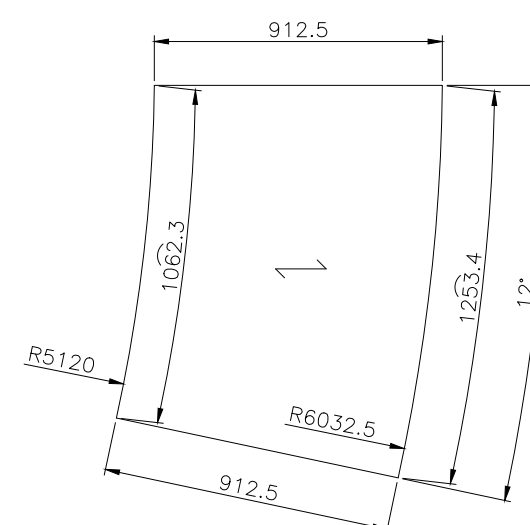


GR-16

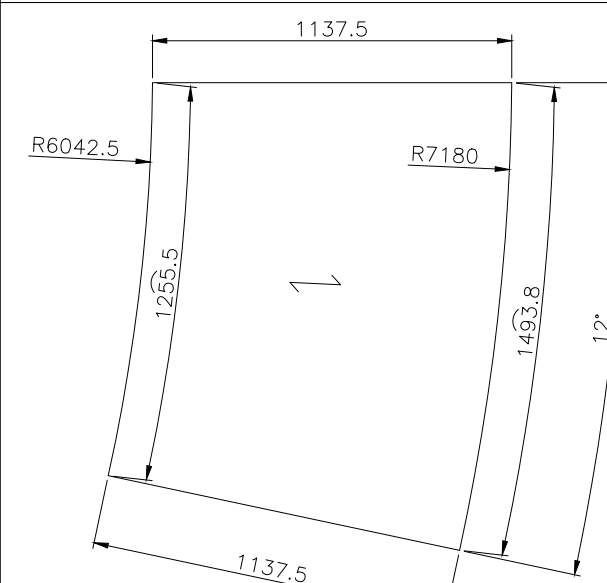


GR-17

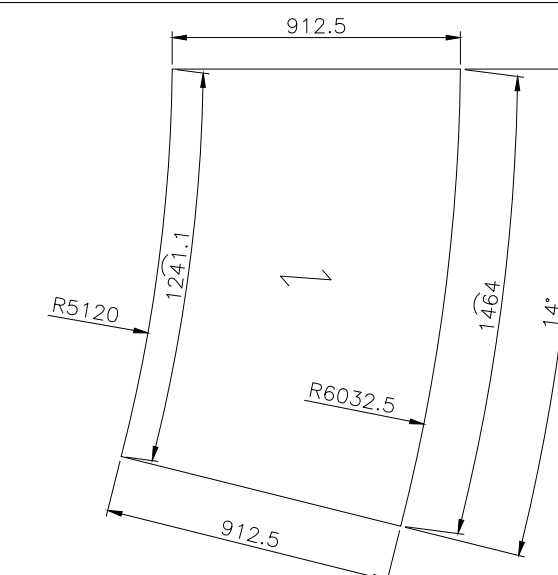


GR-18

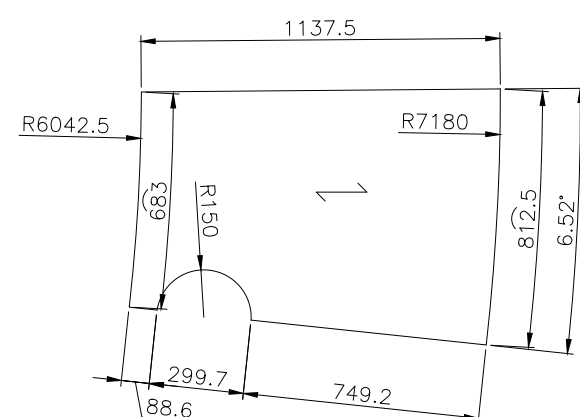


GR-19

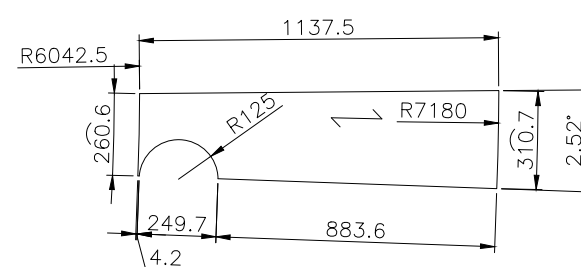

GR-20

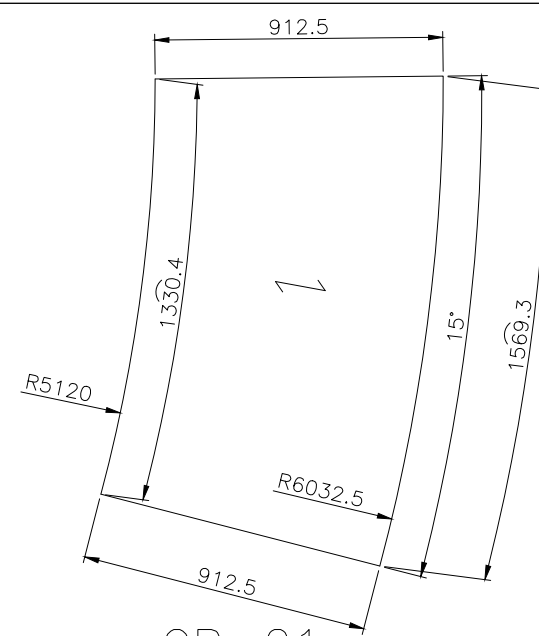


GR-21

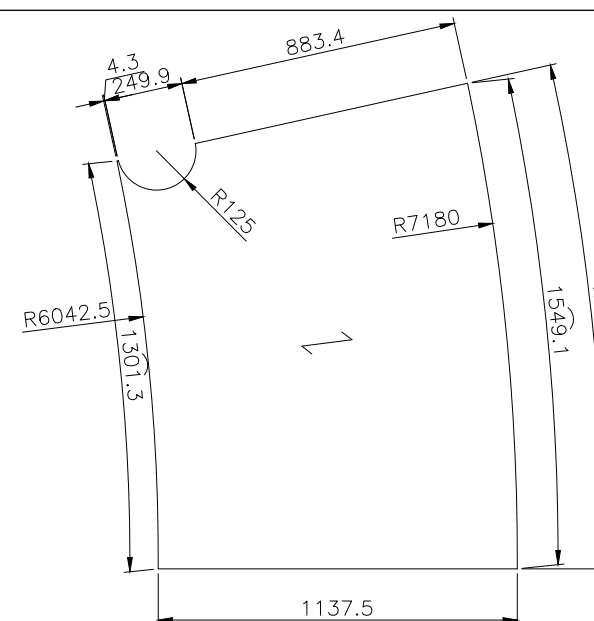


GR-22

01	14/11/2025	IFC	ISSUED FOR CONSTRUCTION				CK	RJ	SP
00	07/10/2025	IFR	ISSUED FOR REVIEW				SR	RJ	SP
Rev.	Date	Status	Revision Description				Iss.	Check.	Appr.
PROJECT NAME & LOGO						CONTRACTOR NAME & LOGO			
This document is the property of the TOTAL GROUP and it shall not be disclosed to third parties or reproduced without the express written permission of the TOTAL GROUP. This document has been generated by an Electronic Document Management System. When printed it shall be considered as "Information only". The controlled copy is the EDMS version and it is document holder's responsibility to make sure that latest version in use.									
Affiliate:	IRAQ		Site:	AG1	Project Phase:	DE			
CENTRAL PROCESSING FACILITIES									
ROOF TANK WITH HANDRAIL DETAIL DRAWING FOR REJECT WATER TANK (TAG NO. B0-T-54-0006)									
Discipline:	PVV	Doc. Type:	GEA	Sector:	B0	System:	7/77		
Company Doc. N°:	IQ-AG1-B0-MIC3-000042				Class:	2	Scale:	1:500	
Contractor Doc. N°:	MIC-01009.10-DRG-028				Format:	A1	Folio:	2 OF	

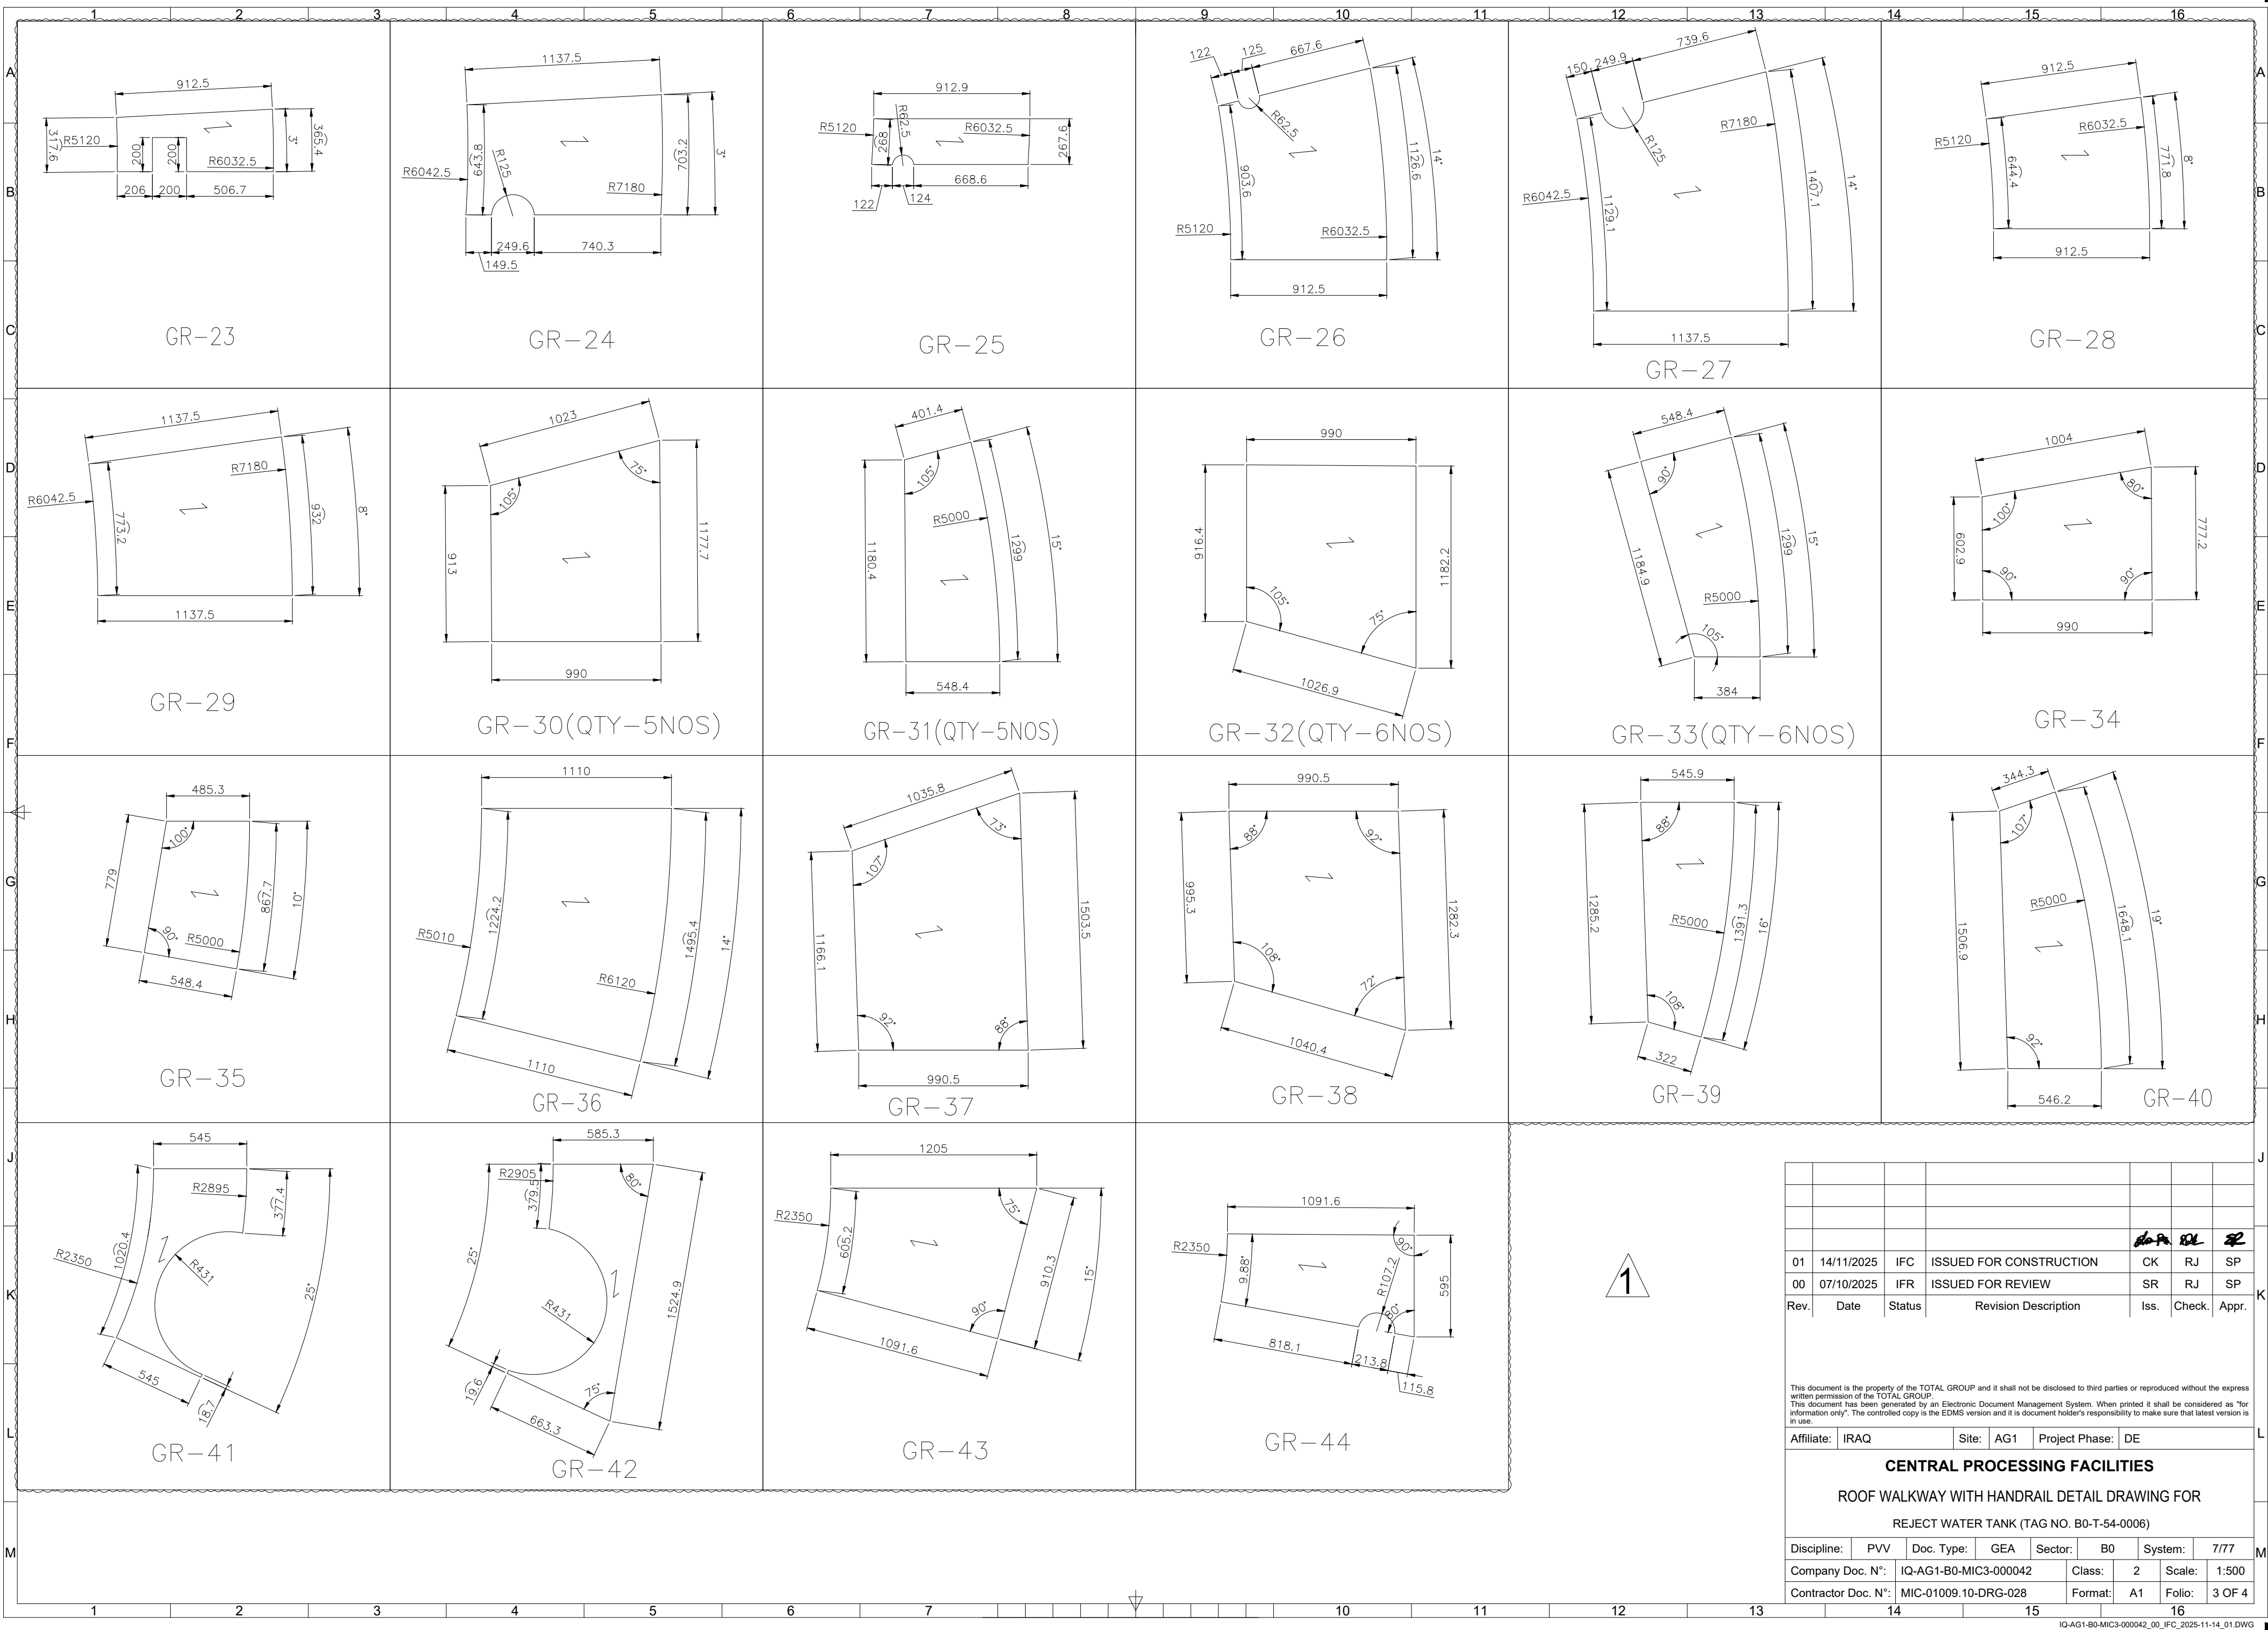

01	14/11/2025	IFC	ISSUED FOR CONSTRUCTION	CK	RJ	SP
00	07/10/2025	IFR	ISSUED FOR REVIEW	SR	RJ	SP
Rev.	Date	Status	Revision Description	Iss.	Check.	Appr.
This document is the property of the TOTAL GROUP and it shall not be disclosed to third parties or reproduced without the express written permission of the TOTAL GROUP. This document has been generated by an Electronic Document Management System. When printed it shall be considered as "for information only". The controlled copy is the EDMS version and it is document holder's responsibility to make sure that latest version is in use.						
Affiliate:	IRAQ	Site:	AG1	Project Phase:	DE	
CENTRAL PROCESSING FACILITIES						
ROOF WALKWAY WITH HANDRAIL DETAIL DRAWING FOR						
REJECT WATER TANK (TAG NO. B0-T-54-0006)						
Discipline:	PVV	Doc. Type:	GEA	Sector:	B0	System: 7/77
Company Doc. N°:	IQ-AG1-B0-MIC3-000042			Class:	2	Scale: 1:500
Contractor Doc. N°:	MIC-01009.10-DRG-028			Format:	A1	Folio: 3 OF 4

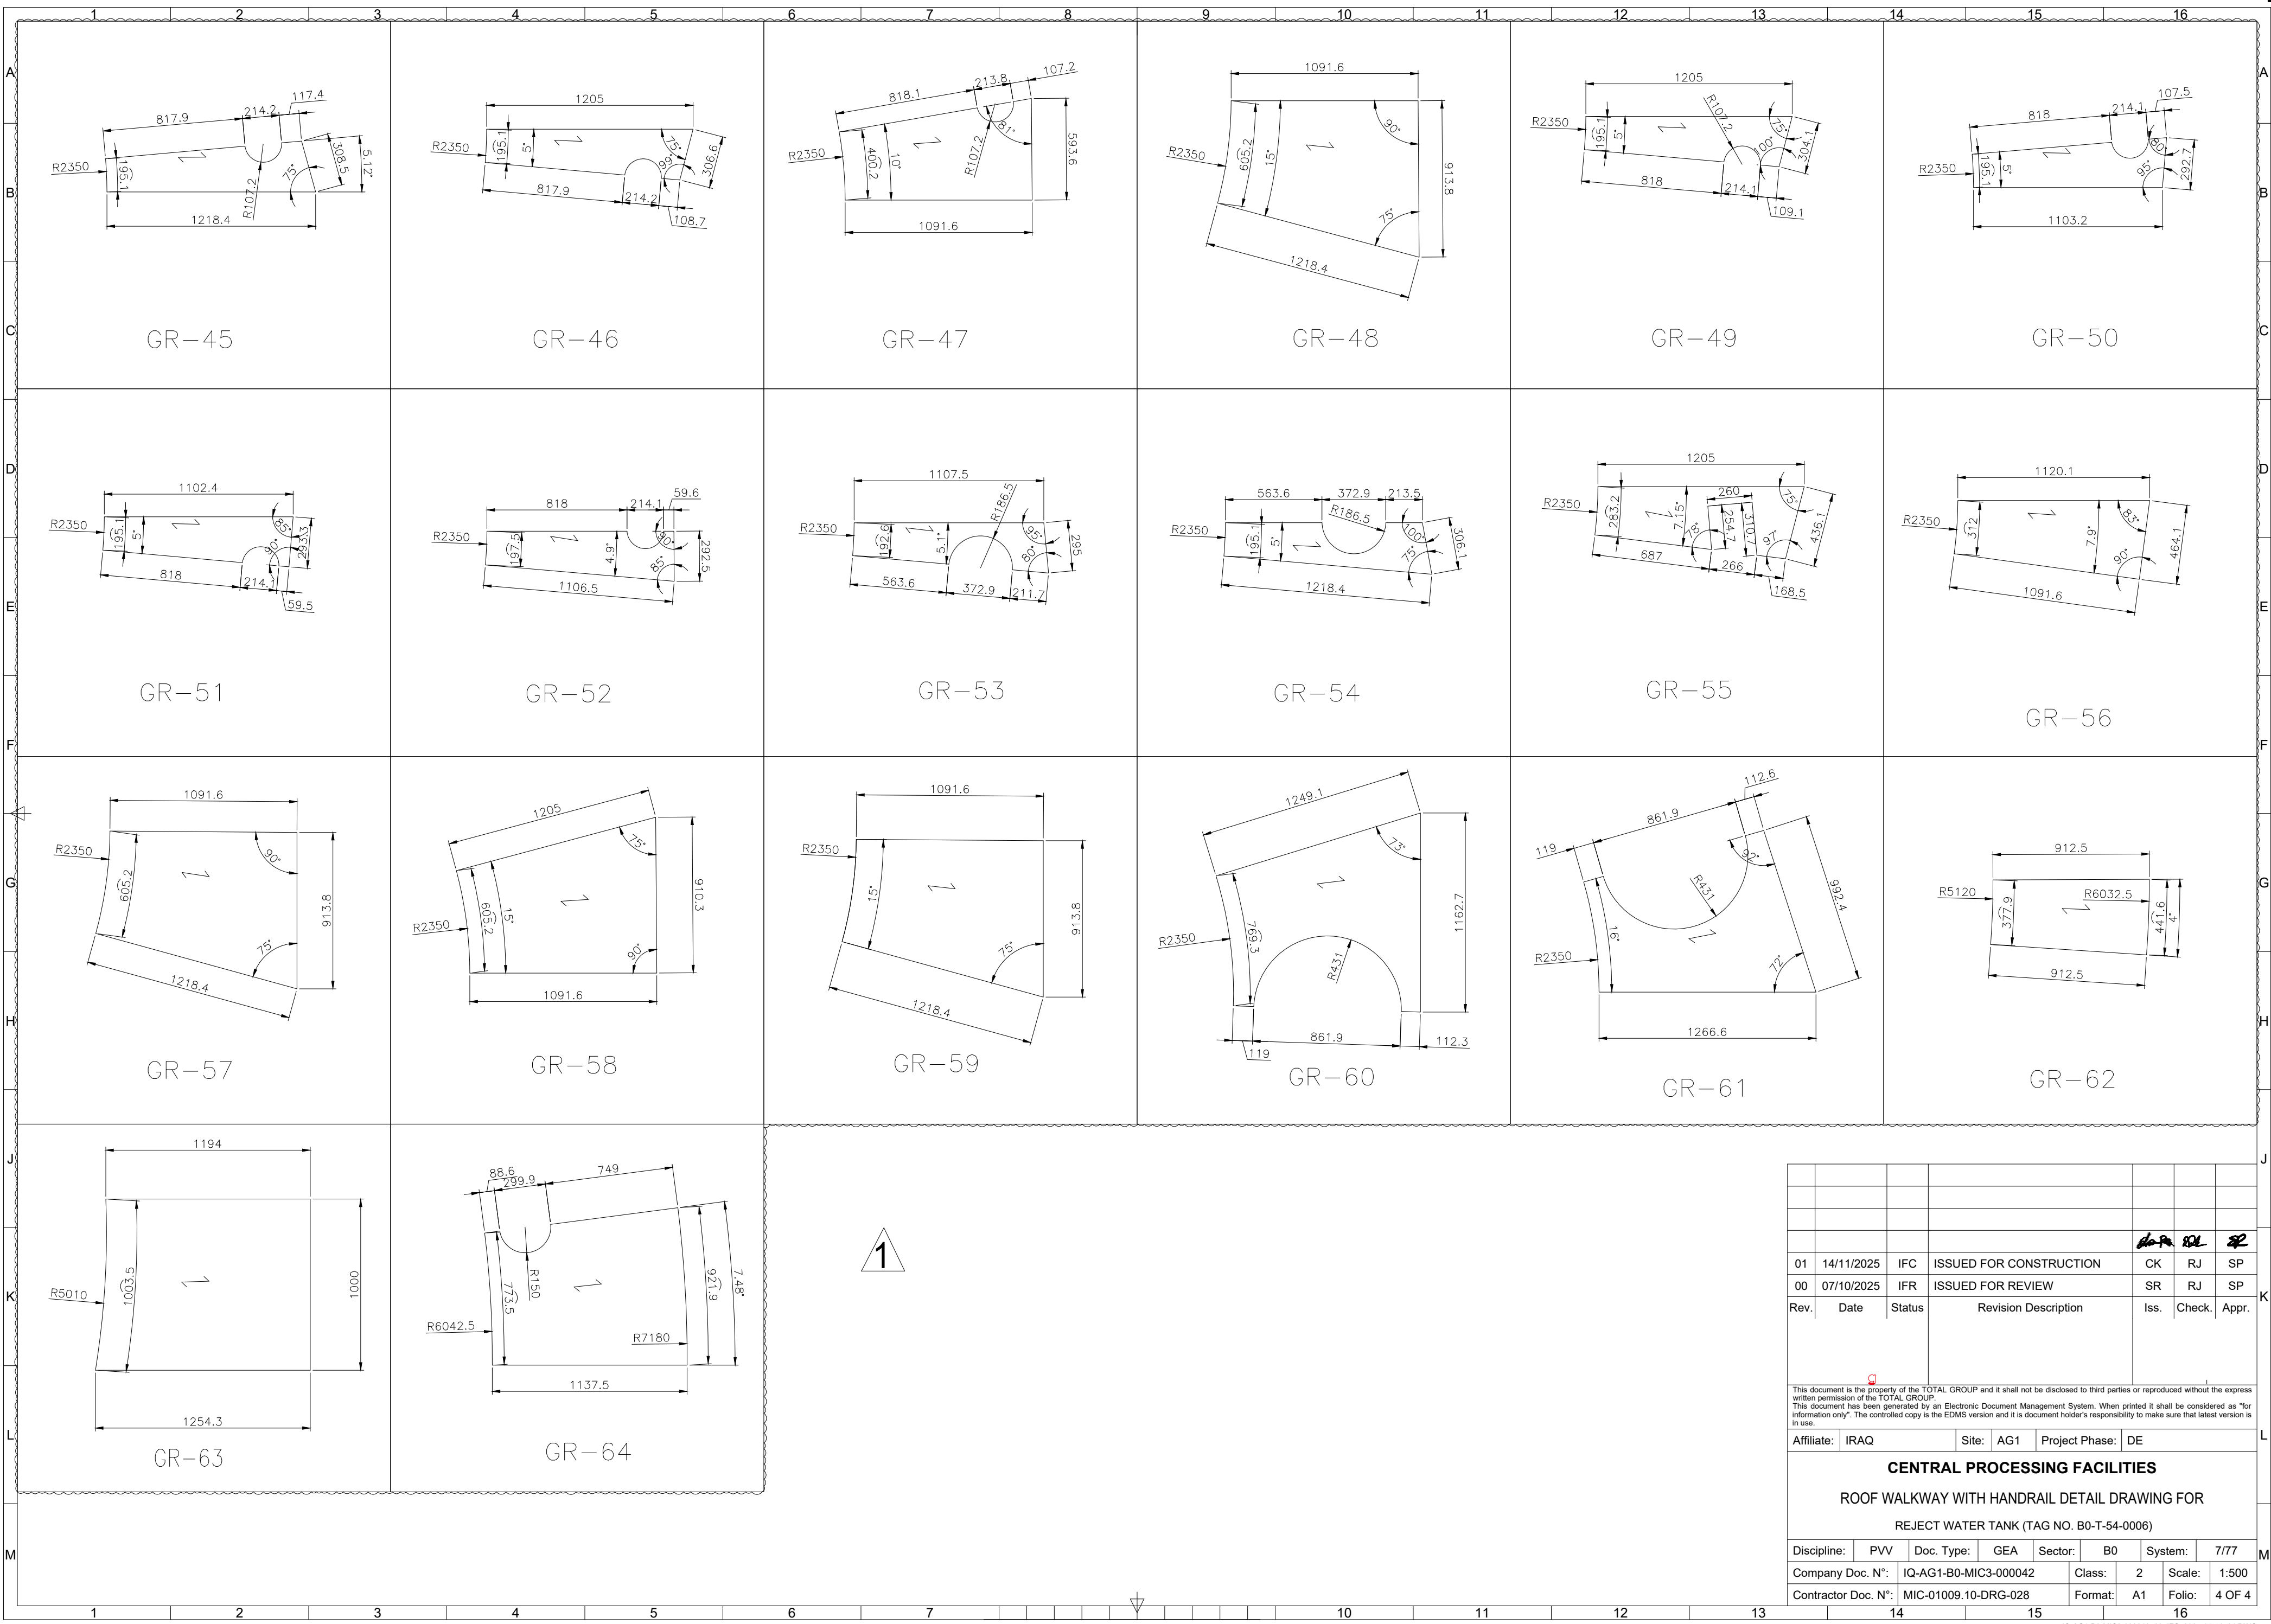

01	14/11/2025	IFC	ISSUED FOR CONSTRUCTION	CK	RJ	SP
00	07/10/2025	IFR	ISSUED FOR REVIEW	SR	RJ	SP
Rev.	Date	Status	Revision Description	Iss.	Check.	Appr.