


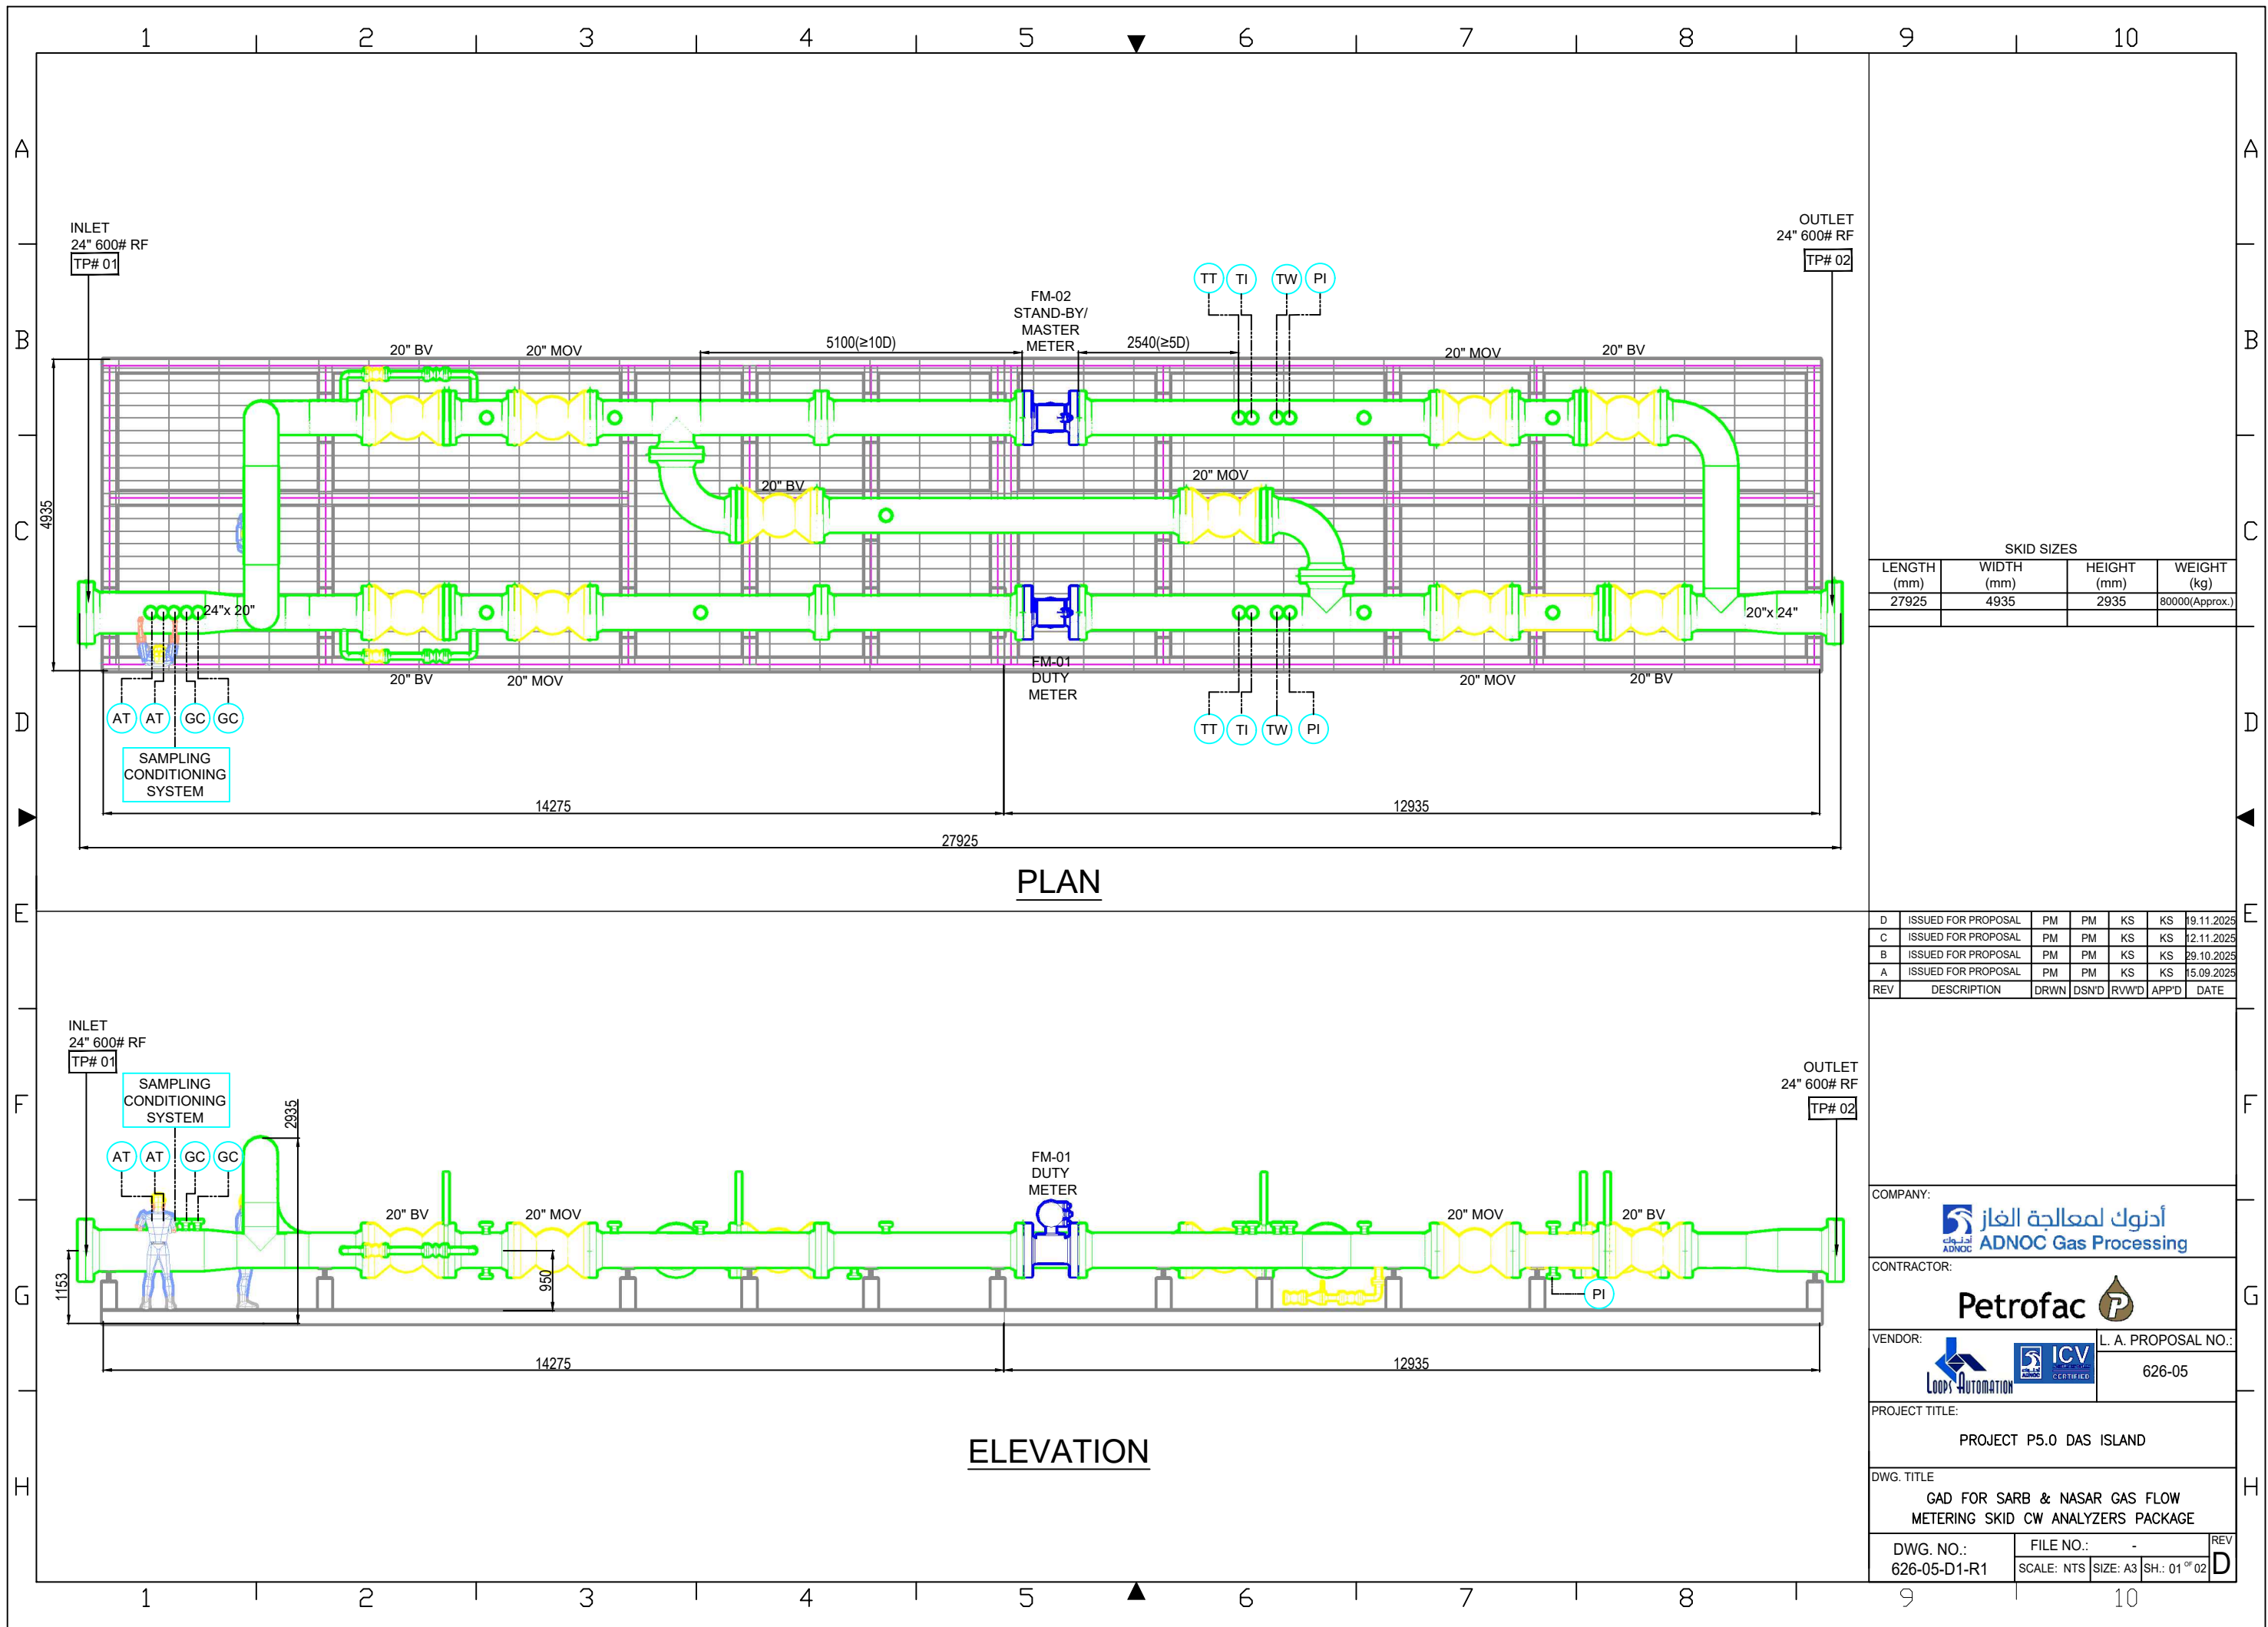

PLAN

ELEVATION

SKID SIZES			
LENGTH (mm)	WIDTH (mm)	HEIGHT (mm)	WEIGHT (kg)
27925	4935	2935	80000(Approx.)

REV	DESCRIPTION	DRWN	DSND	RWVD	APPD	DATE
D	ISSUED FOR PROPOSAL	PM	PM	KS	KS	19.11.2025
C	ISSUED FOR PROPOSAL	PM	PM	KS	KS	12.11.2025
B	ISSUED FOR PROPOSAL	PM	PM	KS	KS	29.10.2025
A	ISSUED FOR PROPOSAL	PM	PM	KS	KS	15.09.2025

COMPANY:		 أدنوك لمعالجة الغاز ADNOC Gas Processing	
CONTRACTOR:		 Petrofac	
VENDOR:		 ICV L.A. PROPOSAL NO.: 626-05	
PROJECT TITLE: PROJECT P5.0 DAS ISLAND			
DWG. TITLE: GAD FOR SARB & NASAR GAS FLOW METERING SKID CW ANALYZERS PACKAGE			
DWG. NO.: 626-05-D1-R1	FILE NO.: -	SCALE: NTS	REV D

