

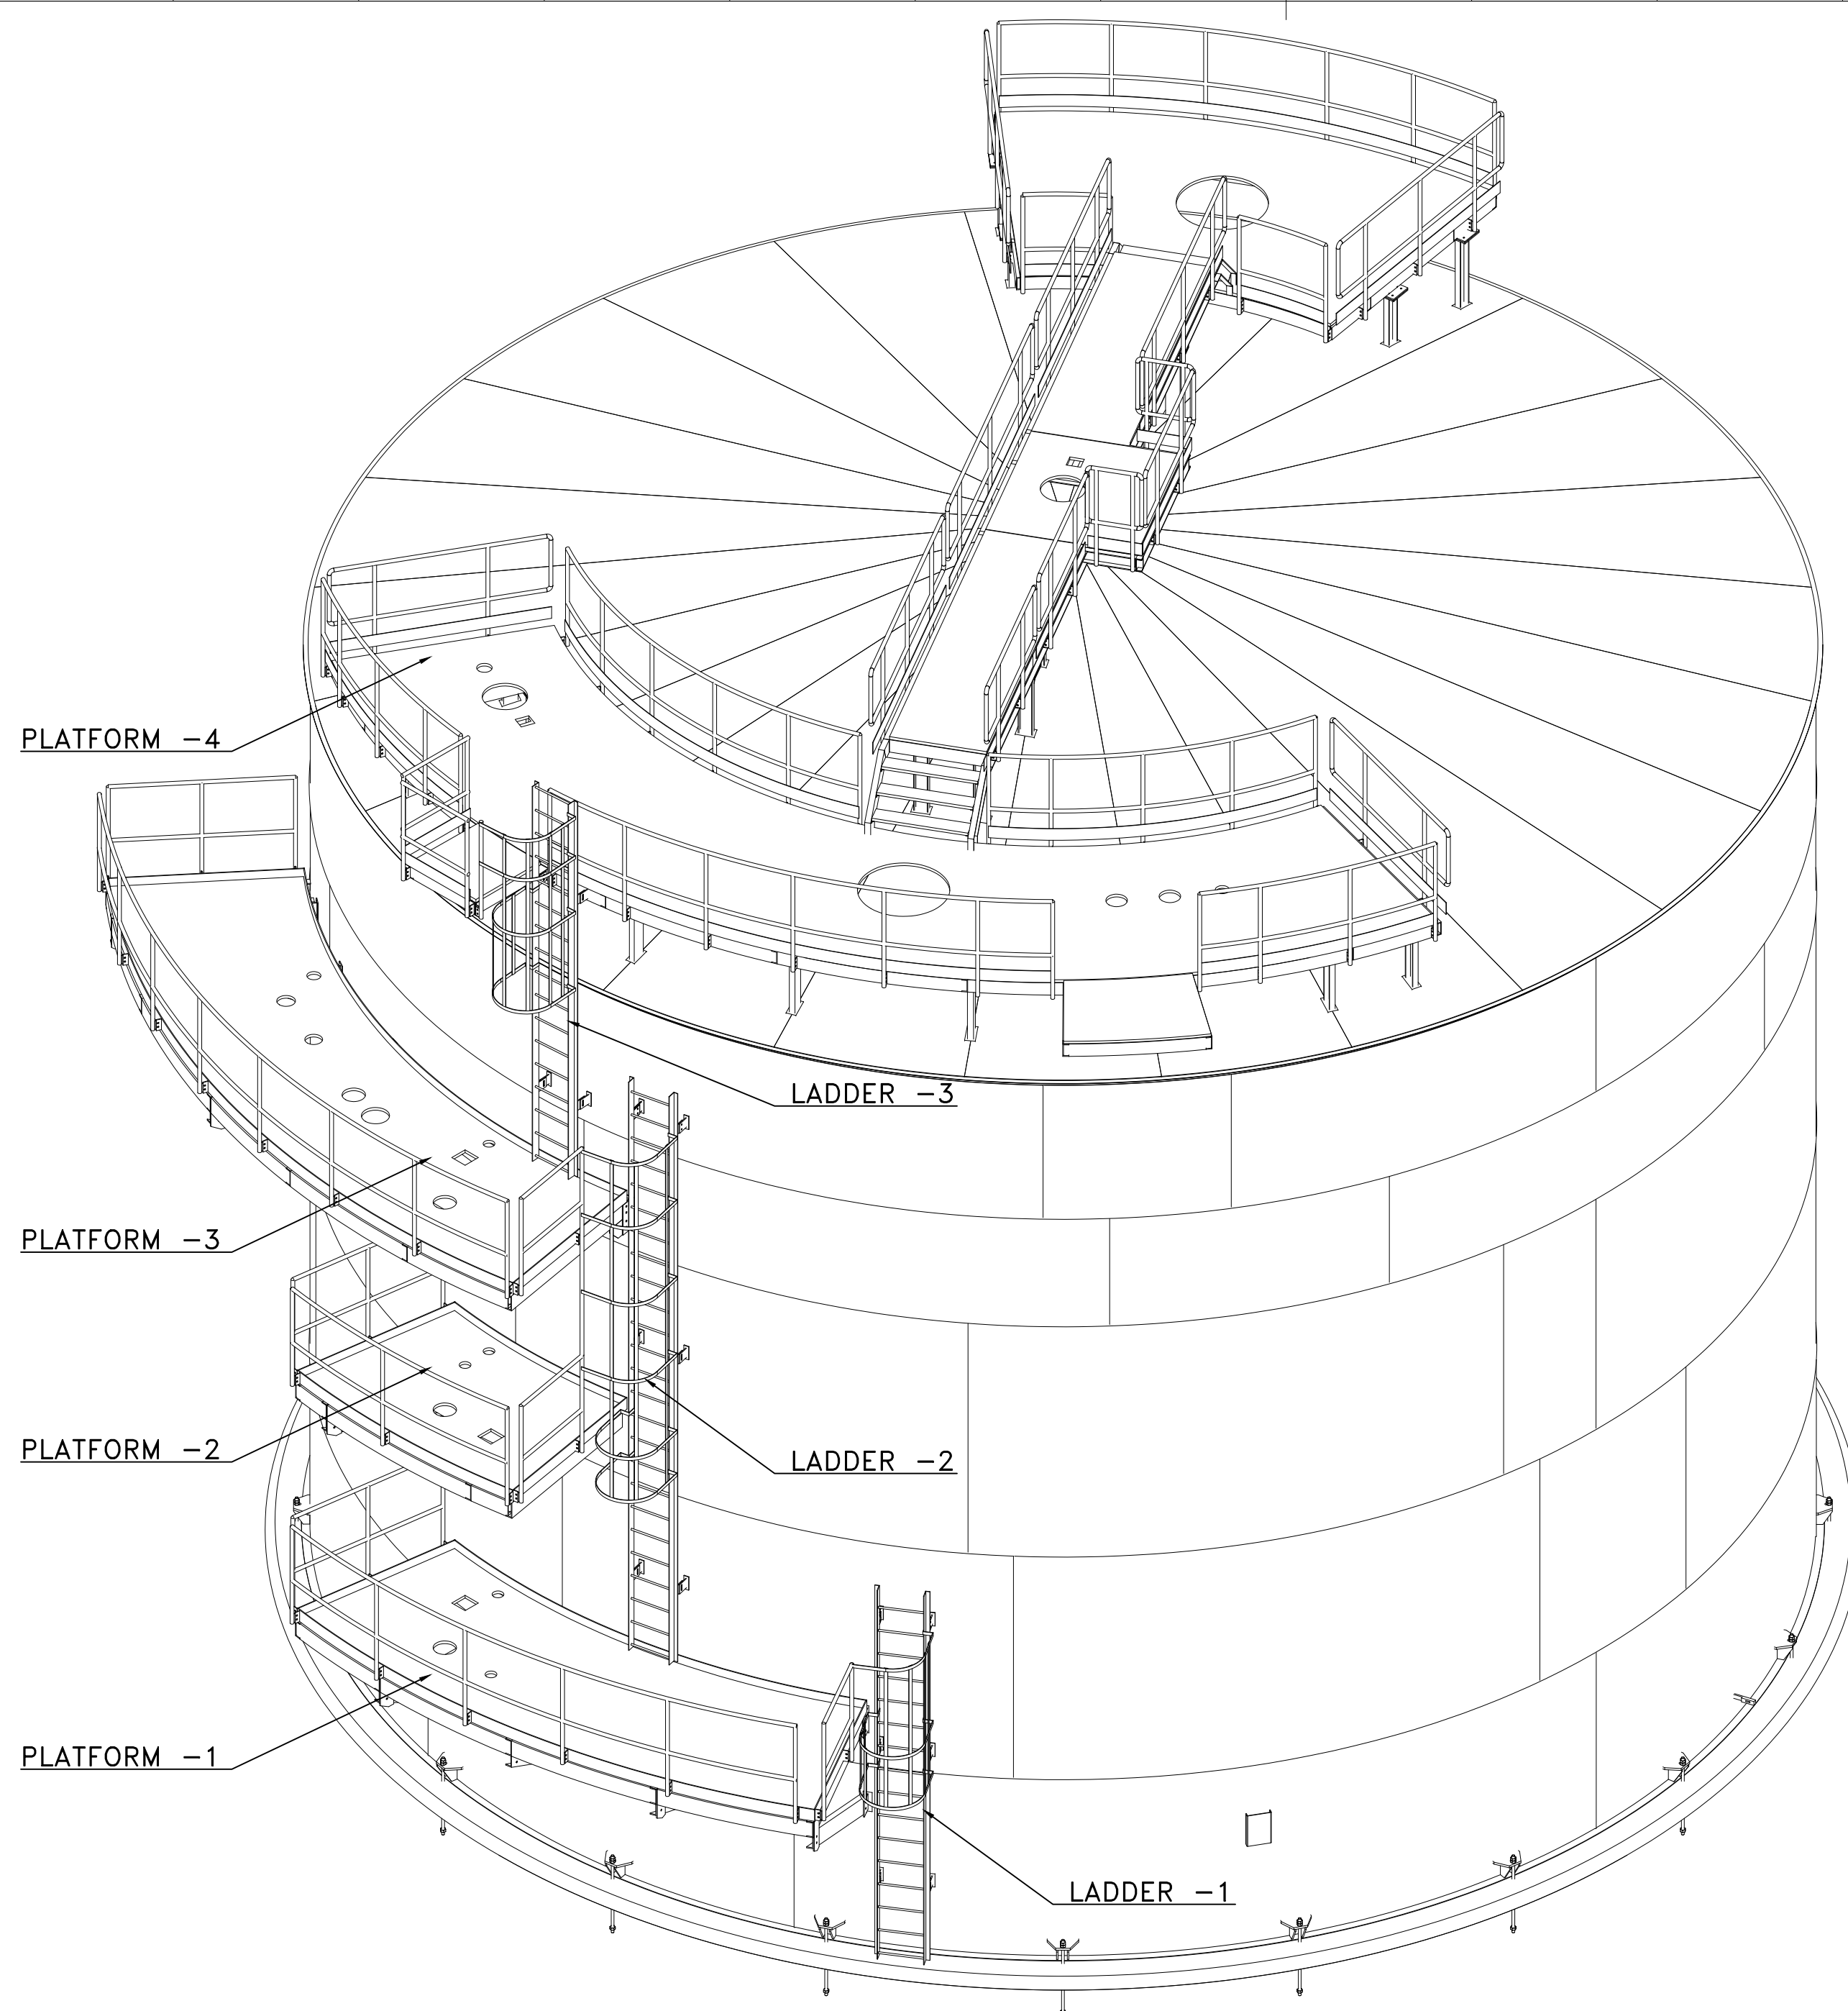
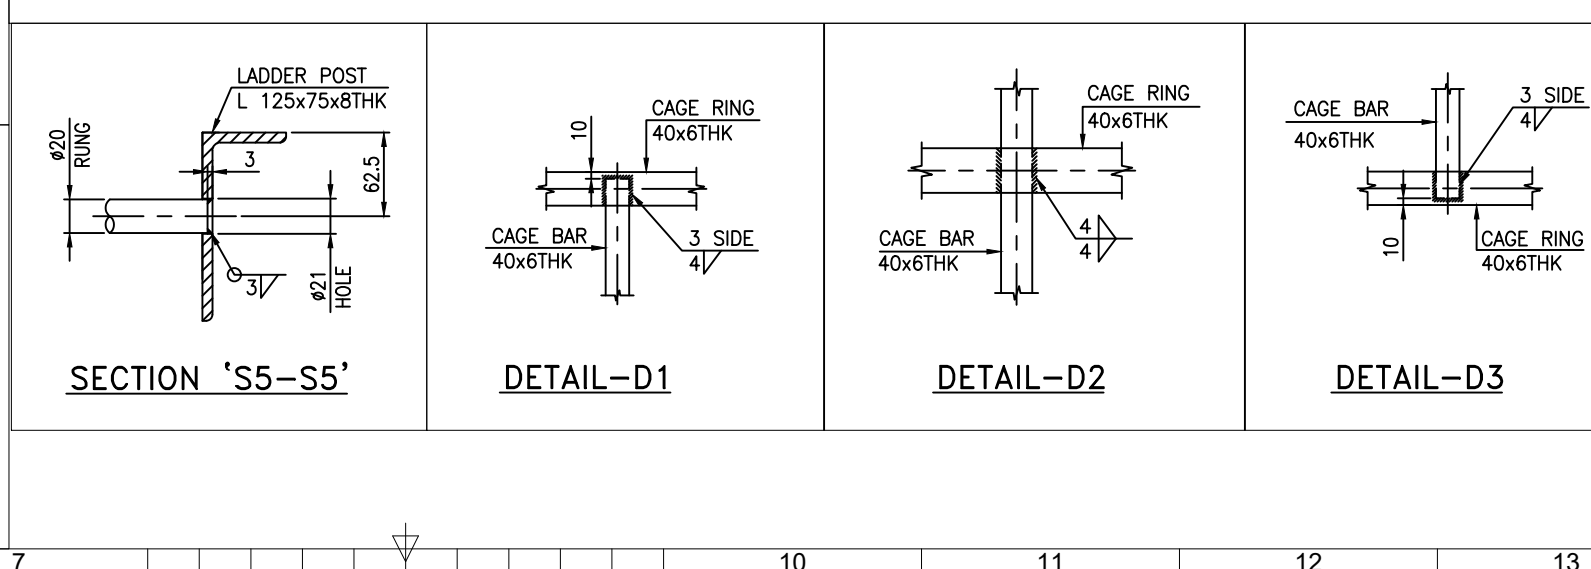
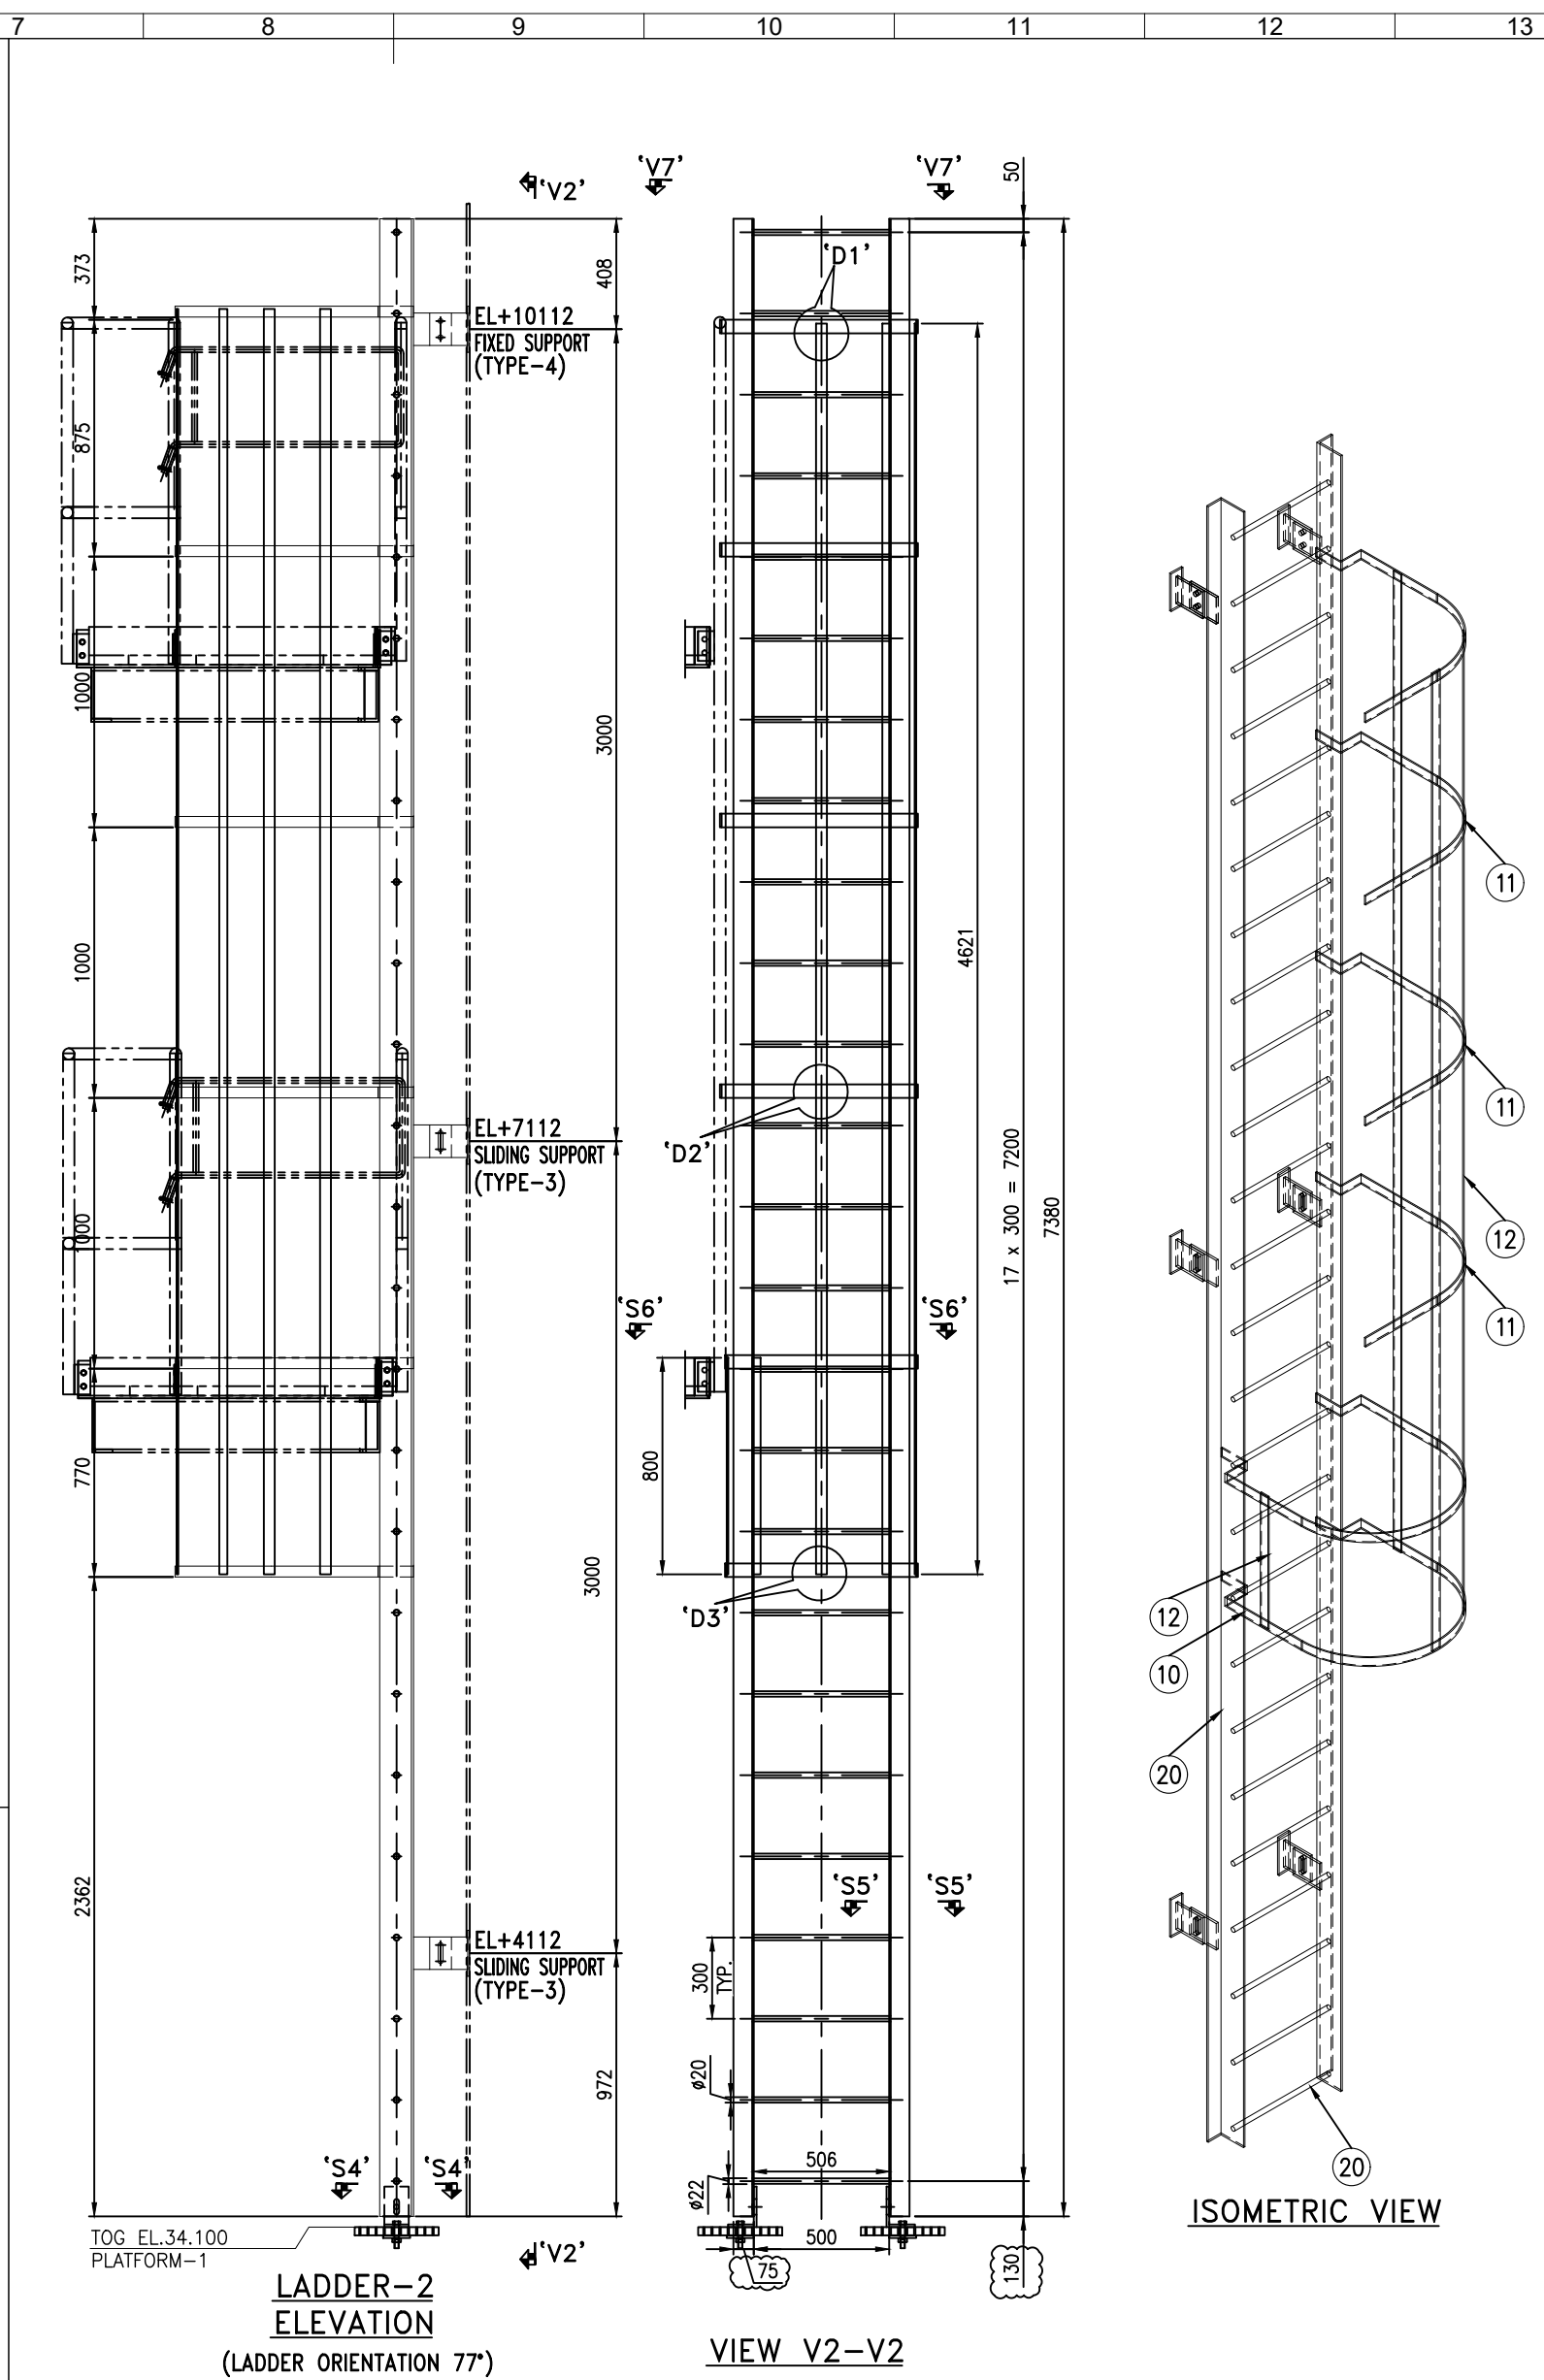


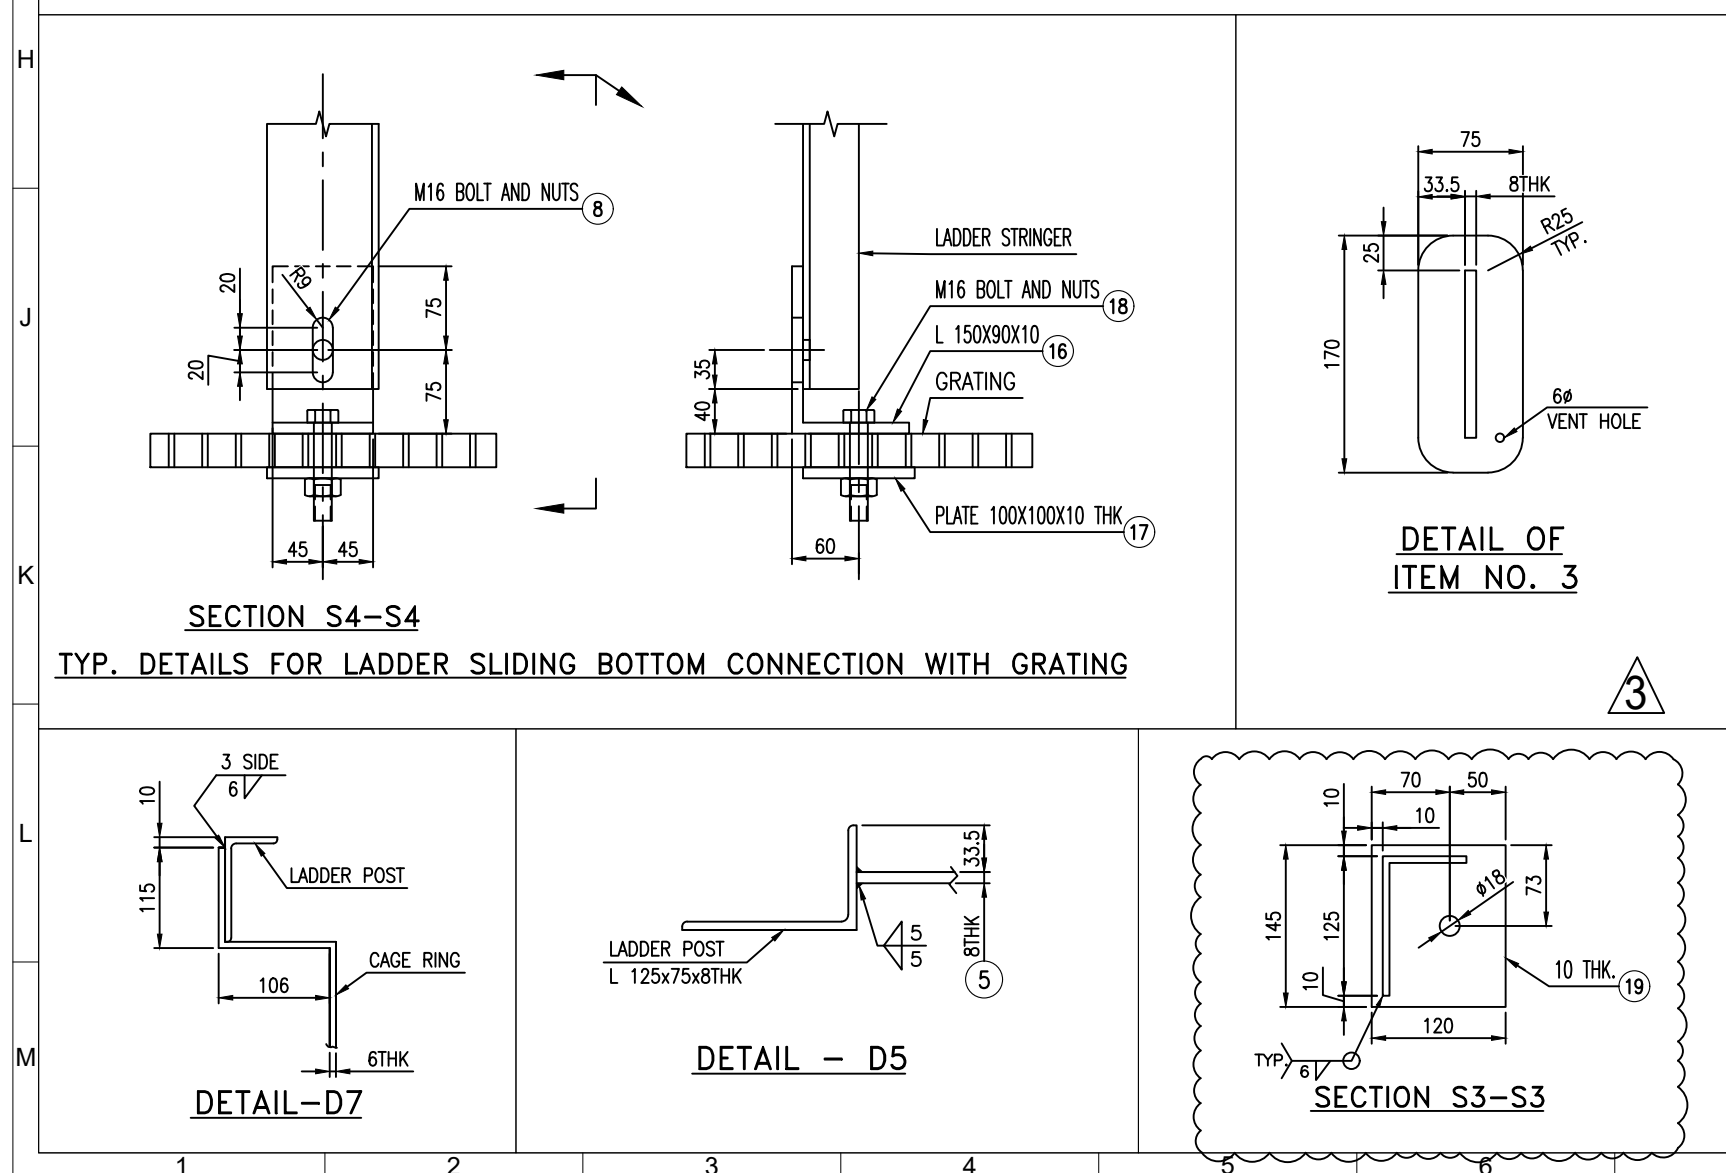

ISOMETRIC VIEW
ASSEMBLY DETAILS FOR LADDER CONNECTION

[illegible]

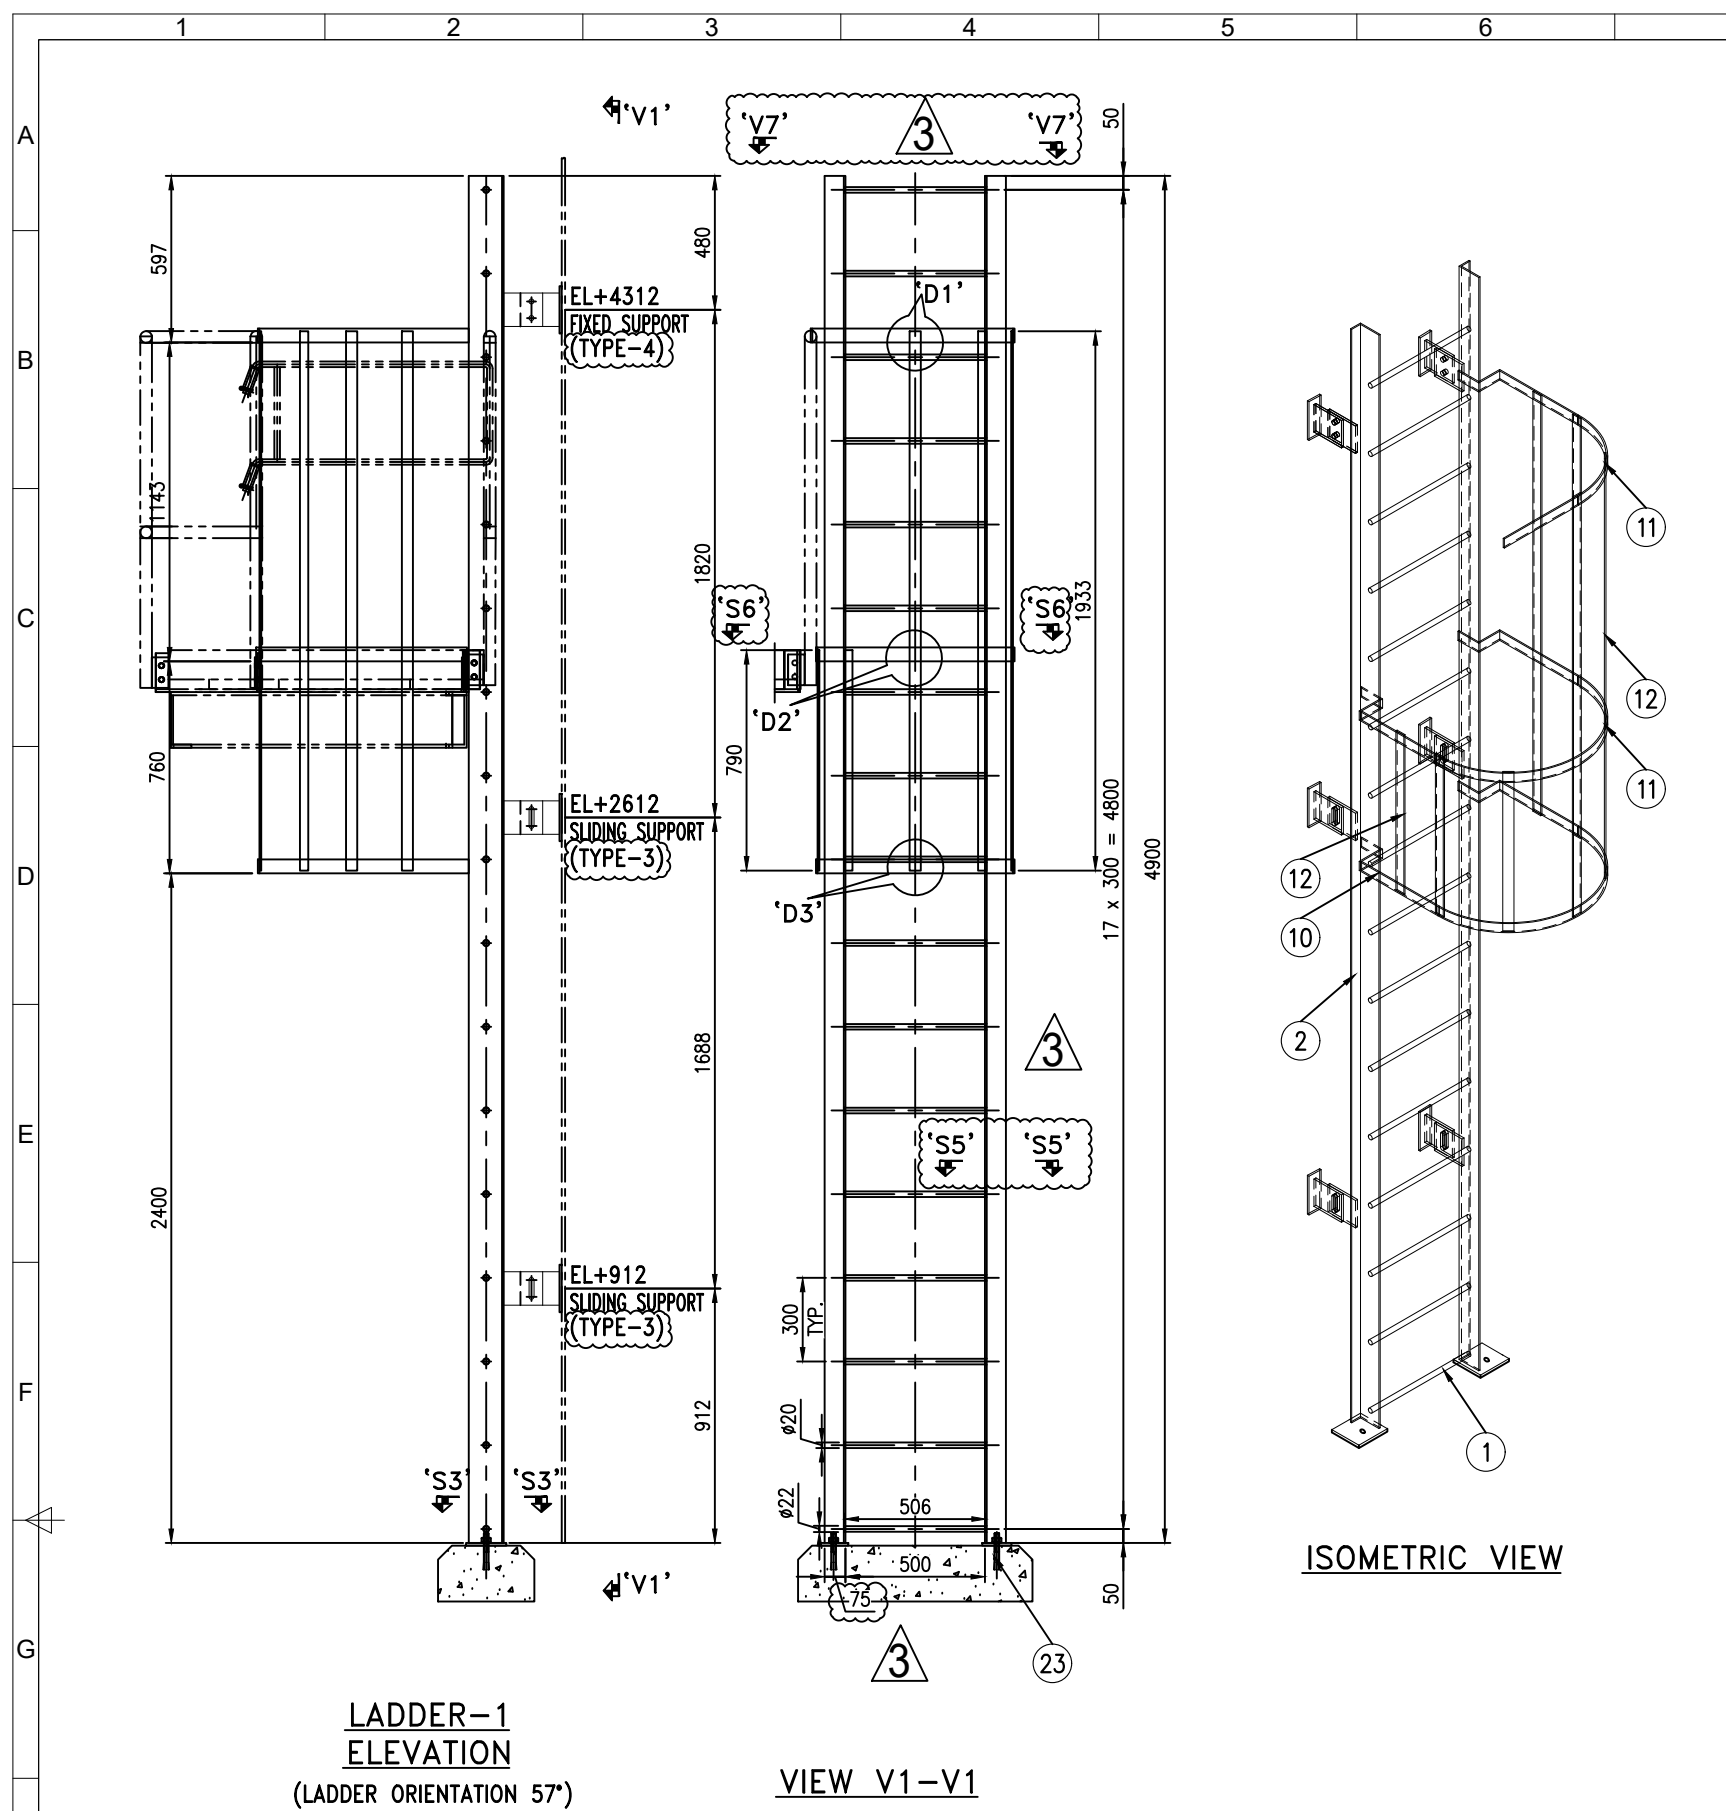

NOTES:

1. ALL DIMENSIONS ARE IN MILLIMETERS UNLESS NOTED OTHERWISE.

2. ALL FILLET WELDS SHALL BE 6MM UNLESS OTHERWISE SPECIFIED.

3. ALL SHARP EDGES SHALL BE ROUNDED OFF.

4. PROJECT REFERENCE STANDARD DRAWING NO : IQ-AG1-A0-GHB1-133011 FOLLOWED BY MICODA.

REFERENCE DOCUMENT NUMBER

S.NO	CLIENT DOC. NO.	DOCUMENT NAME
1	IQ-AG1-B0-MIC3-000005	MECHANICAL DESIGN CALCULATION FOR HYGIENE WATER STORAGE TANK (TAG NO. B0-T-50-0005)
2	IQ-AG1-B0-MIC3-000007	MECHANICAL DATA SHEET FOR HYGIENE WATER STORAGE TANK (TAG NO. B0-T-50-0005)
3	IQ-AG1-B0-MIC3-000009	GENERAL ARRANGEMENT DRAWING FOR HYGIENE WATER STORAGE TANK (TAG NO. B0-T-50-0005)
4	IQ-AG1-B0-MIC3-000013	SHELL DEVELOPMENT DRAWING FOR HYGIENE WATER STORAGE TANK (TAG NO. B0-T-50-0005)
5	IQ-AG1-B0-MIC3-000021	ROOF NOZZLE DETAIL DRAWING INCLUDES INTERNAL DIP PIPE AND ITS SUPPORTING ARRANGEMENTS FOR HYGIENE WATER STORAGE TANK (TAG NO. B0-T-50-0005)
6	IQ-AG1-B0-MIC3-000025	FOUNDATION / FOOTPRINT DRAWING ALONG WITH FOUNDATION LOADING DATA FOR HYGIENE WATER STORAGE TANK (TAG NO. B0-T-50-0005)
7	IQ-AG1-B0-MIC3-000037	NAME PLATE & BRACKET DRAWING FOR HYGIENE WATER STORAGE TANK (TAG NO. B0-T-50-0005)
8	IQ-AG1-B0-MIC3-000078	CATHODIC PROTECTION DRAWINGS HYGIENE WATER STORAGE TANK (TAG NO. B0-T-50-0005)

--	--	

[illegible]