


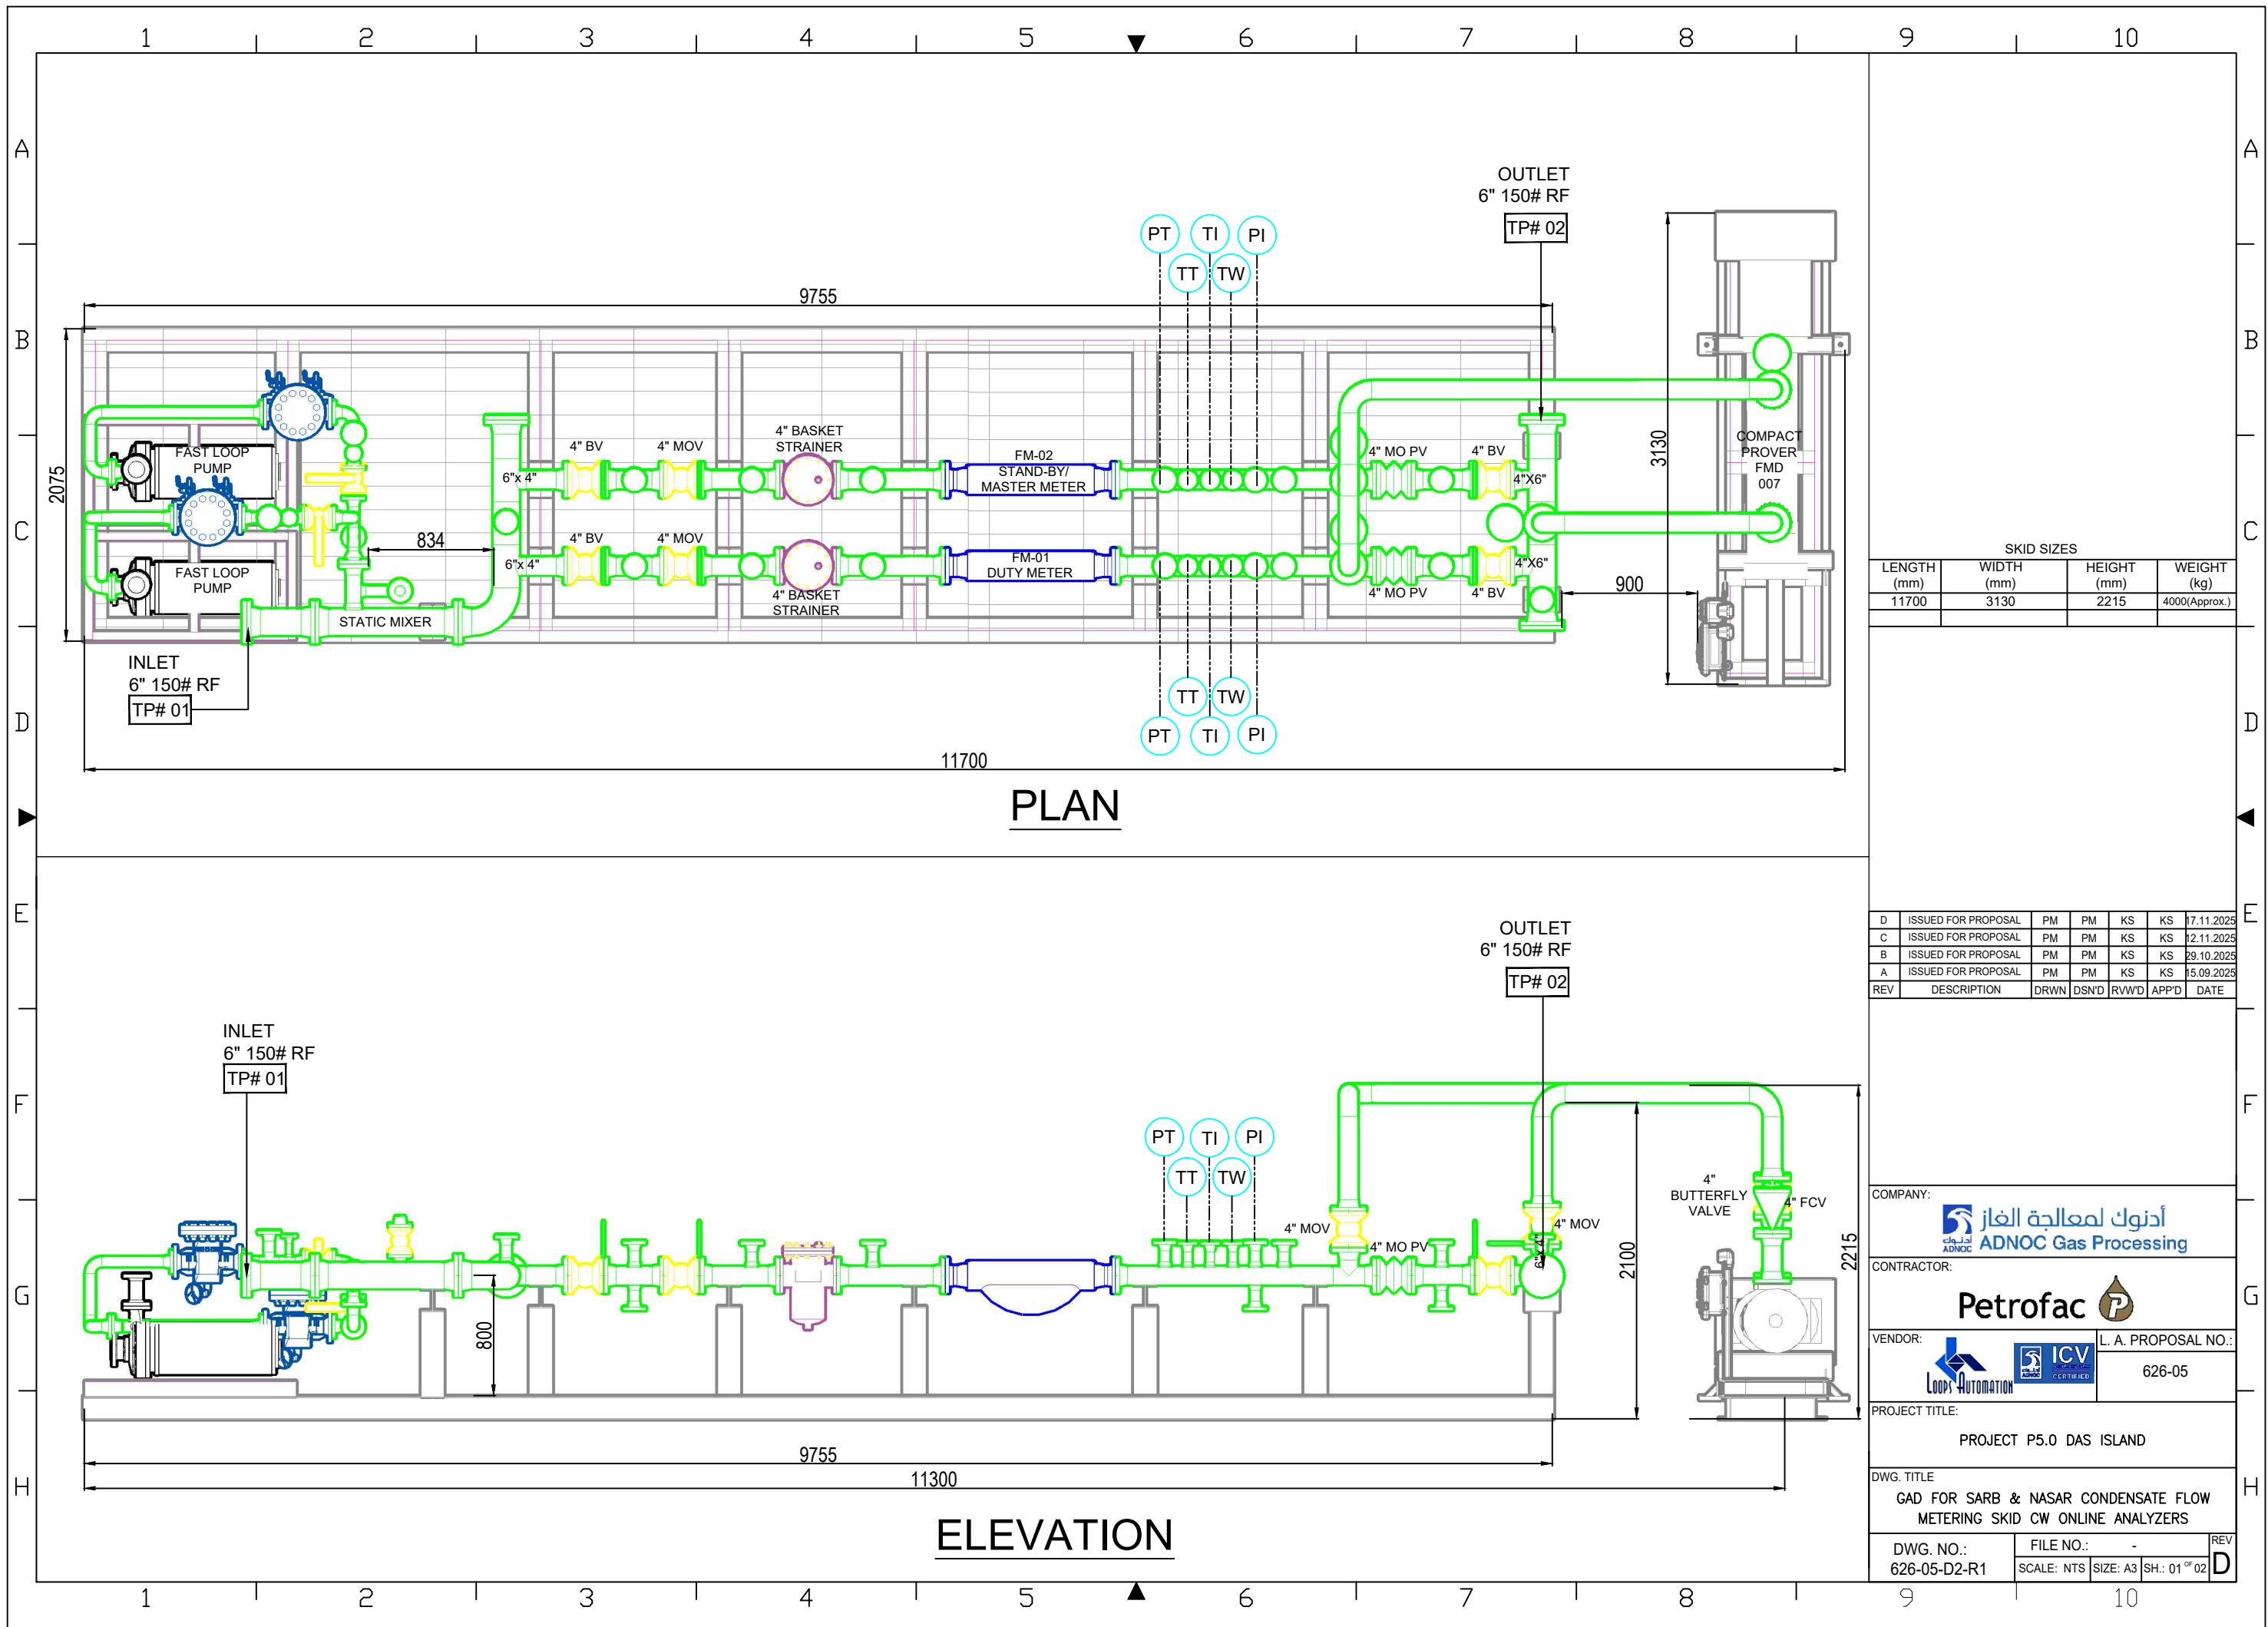


PLAN

ELEVATION

SKID SIZES			
LENGTH (mm)	WIDTH (mm)	HEIGHT (mm)	WEIGHT (kg)
11700	3130	2215	4000(Approx.)

REV	DESCRIPTION	DRWN	DSND	RVWD	APPD	DATE
D	ISSUED FOR PROPOSAL	PM	PM	KS	KS	17.11.2025
C	ISSUED FOR PROPOSAL	PM	PM	KS	KS	12.11.2025
B	ISSUED FOR PROPOSAL	PM	PM	KS	KS	29.10.2025
A	ISSUED FOR PROPOSAL	PM	PM	KS	KS	15.09.2025

COMPANY:		أدنوك لمعالجة الغاز ADNOC Gas Processing	
CONTRACTOR:		Petrofac	
VENDOR:		L. A. PROPOSAL NO.: 626-05	
PROJECT TITLE:		PROJECT P5.0 DAS ISLAND	
DWG. TITLE		GAD FOR SARB & NASAR CONDENSATE FLOW METERING SKID CW ONLINE ANALYZERS	
DWG. NO.:	FILE NO.:	REV	
626-05-D2-R1	SCALE: NTS	SIZE: A3	SH: 01 OF 02

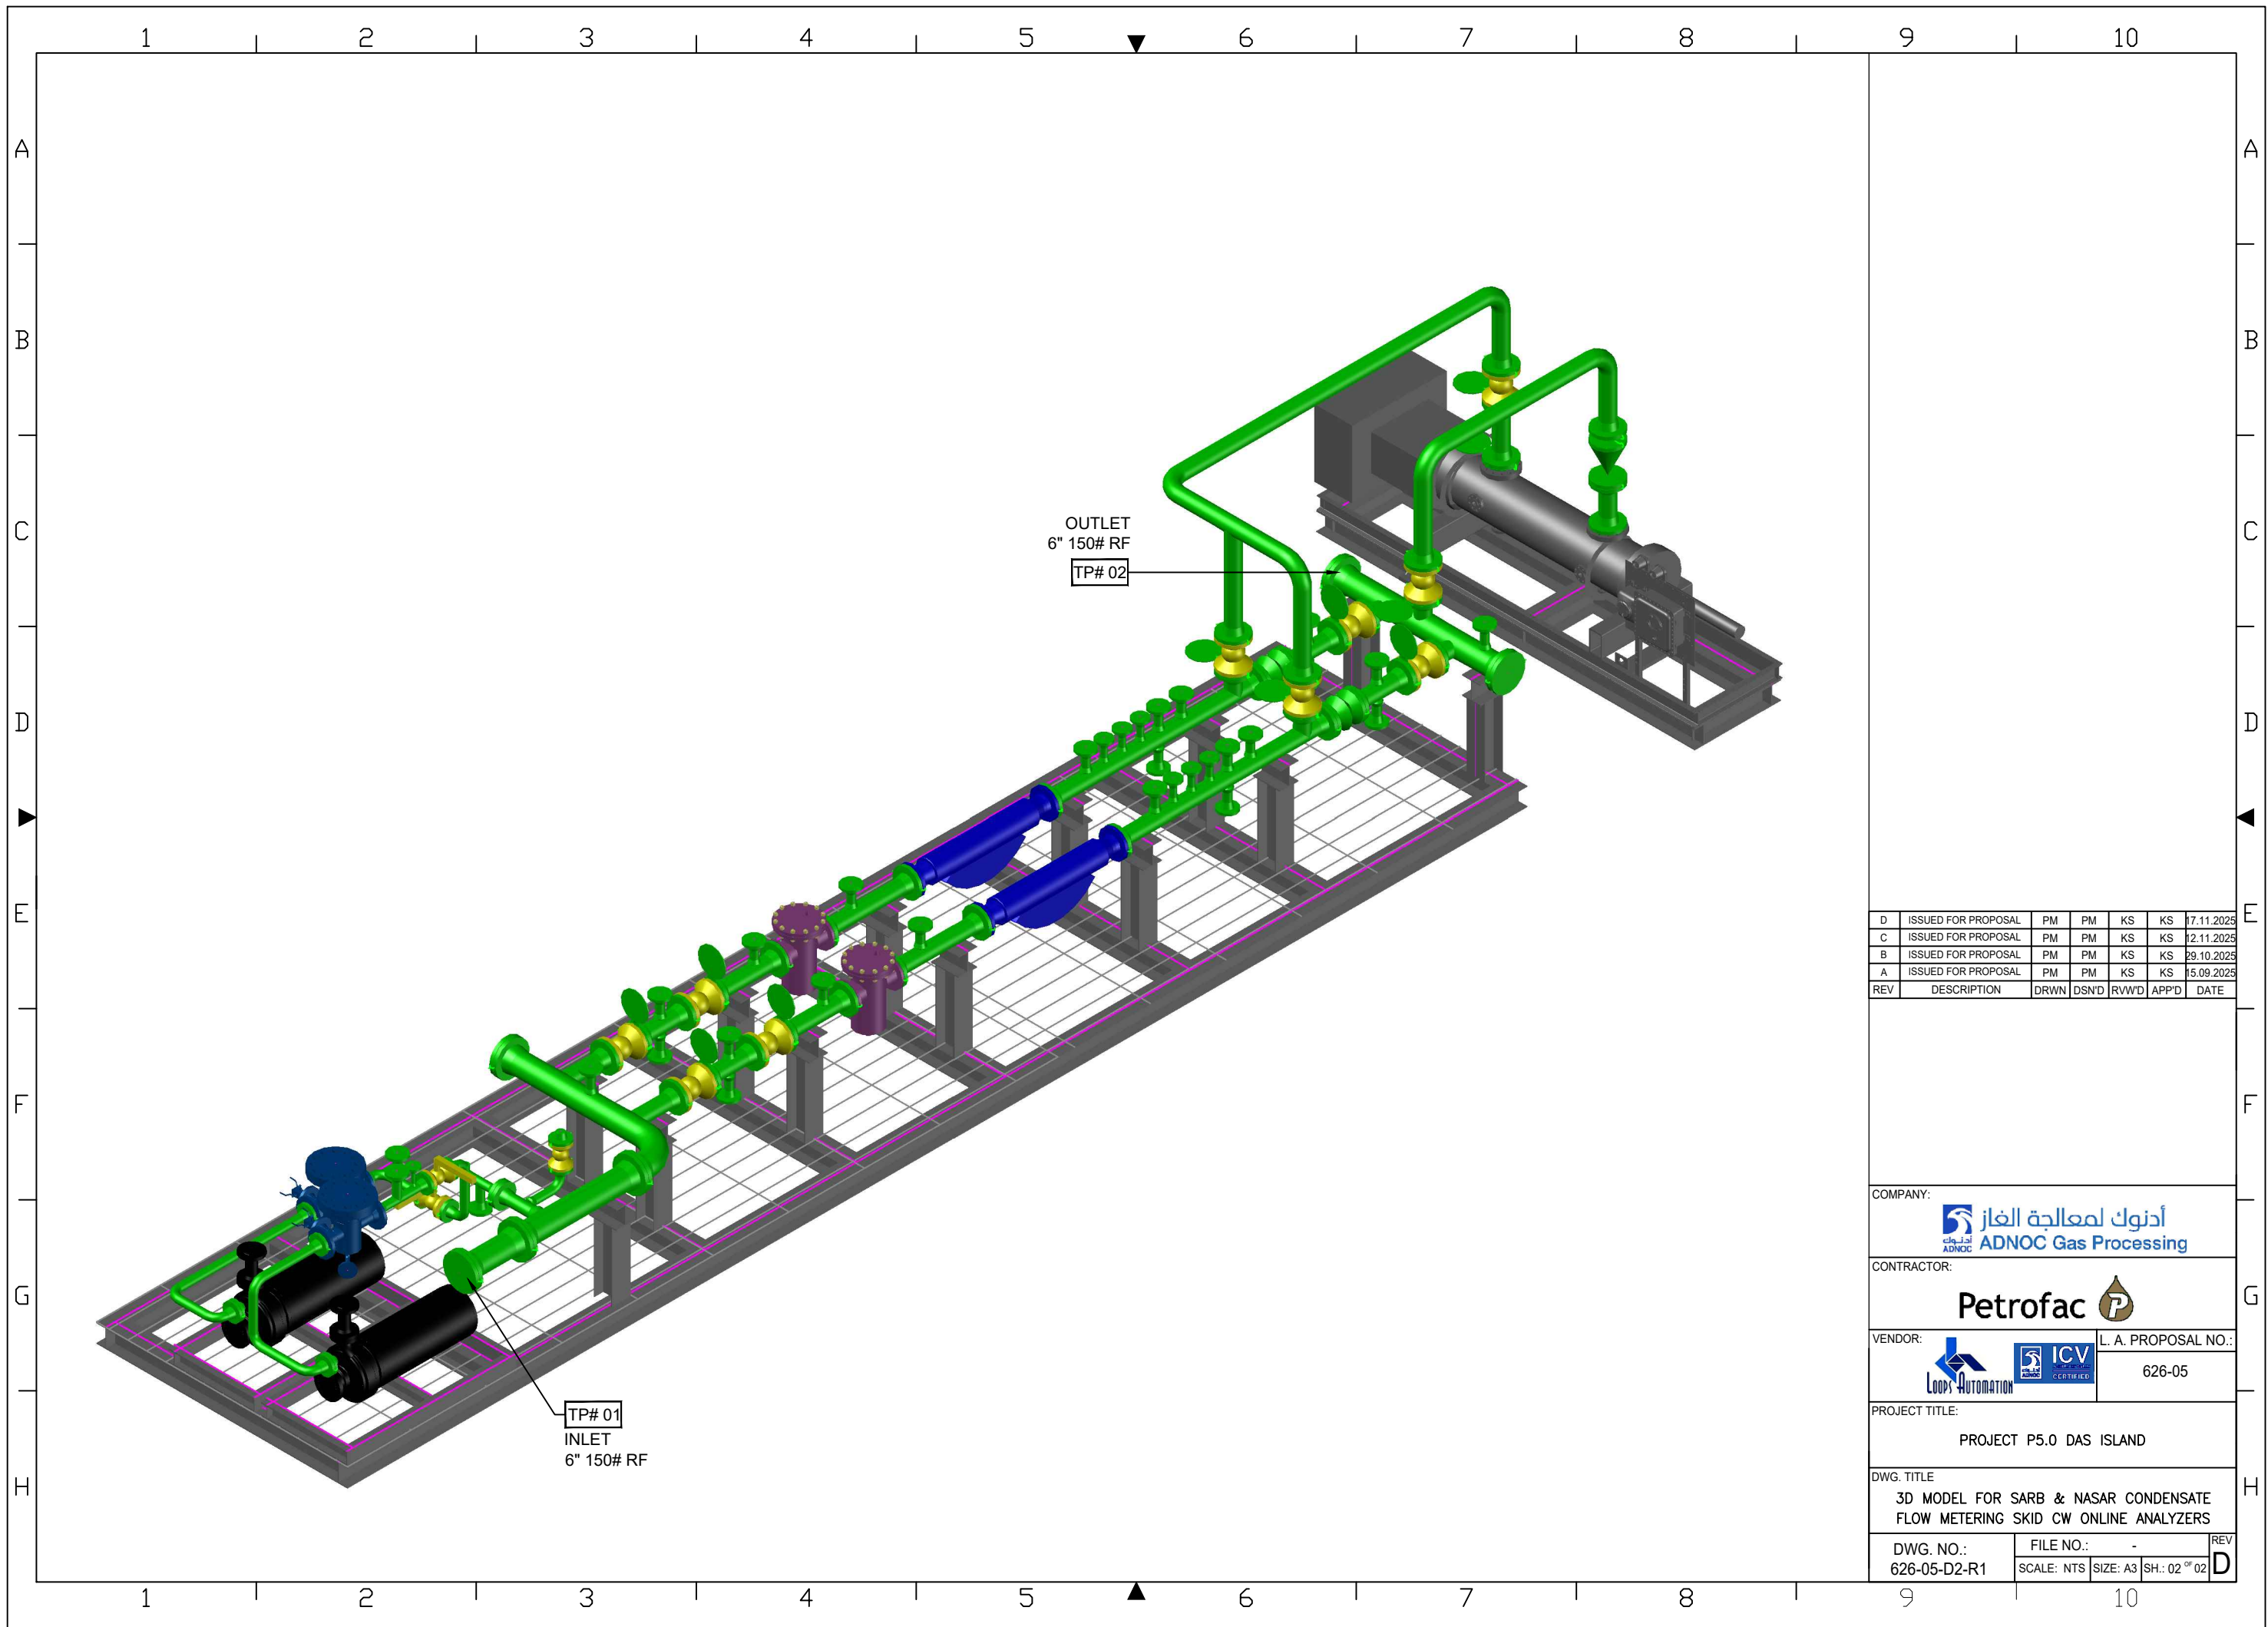

D	ISSUED FOR PROPOSAL	PM	PM	KS	KS	17.11.2025
C	ISSUED FOR PROPOSAL	PM	PM	KS	KS	12.11.2025
B	ISSUED FOR PROPOSAL	PM	PM	KS	KS	29.10.2025
A	ISSUED FOR PROPOSAL	PM	PM	KS	KS	15.09.2025
REV	DESCRIPTION	DRWN	DSND	RVWD	APPD	DATE

COMPANY:		 أدنوك لمعالجة الغاز ADNOC 	
CONTRACTOR:			
			
VENDOR:		L. A. PROPOSAL NO.:	
 		626-05	
PROJECT TITLE:			
PROJECT P5.0 DAS ISLAND			
DWG. TITLE			
3D MODEL FOR SARB & NASAR CONDENSATE FLOW METERING SKID CW ONLINE ANALYZERS			
DWG. NO.:		FILE NO.:	
626-05-D2-R1		-	
SCALE: NTS		SIZE: A3	
		SH.: 02 OF 02	
		REV	
		D	